

**MRT PUTRAJAYA LINE**  
**(PREVIOUSLY KNOWN AS SG BULOH – SERDANG – PUTRAJAYA)**



**KERAJAAN MALAYSIA**

**REVISED RAILWAY SCHEME SUBMISSION**

**STATION SITE CONTEXT PLAN**

SUPERVISING AGENCY:



PROJECT AND ASSET OWNER:



MASS RAPID TRANSIT  
CORPORATION SDN BHD


**MRT PUTRAJAYA LINE**  
**(PREVIOUSLY KNOWN AS SG BULOH – SERDANG – PUTRAJAYA)**



**KERAJAAN MALAYSIA**

**STATION SITE CONTEXT PLAN  
(NORTHERN)**


SUPERVISING AGENCY:

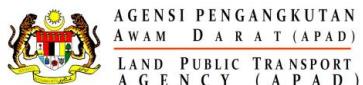

PROJECT AND ASSET OWNER:



MASS RAPID TRANSIT  
CORPORATION SDN BHD

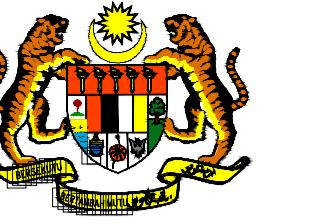

KERAJAAN MALAYSIA

PROJECT TITLE:  
PROJEK MASS RAPID TRANSIT LALUAN 2:  
PUTRAJAYA LINE  
(formerly known as PROJEK MRT LALUAN 2:  
SG BULOH - SERDANG - PUTRAJAYA (SSP))


PROJECT PACKAGE:  
ELEVATED NORTH

SUPERVISING AGENCY :  
**AGENSI PENGANGKUTAN AWAM DARAT (APAD)**  
LAND PUBLIC TRANSPORT AGENCY (APAD)


AGENSI PENGANGKUTAN AWAM DARAT (A.P.A.D.)

ARAS G, M DAN 20, MENARA TUN ISMAIL MOHAMED ALI,  
NO. 25, JALAN RAJA LAUT, 50350 KUALA LUMPUR,  
MALAYSIA.  
TEL (ARAS G): 603-2603 6700 / TEL (ARAS 20): 603-2603 6600

PROJECT OWNER :  
**MRT CORP**  
Mass Rapid Transit Corporation Sdn Bhd  
(902884-V)  
5th FLOOR MENARA I&P 1,  
JALAN DUNGUN, DAMANSARA HEIGHTS,  
50490 KUALA LUMPUR.

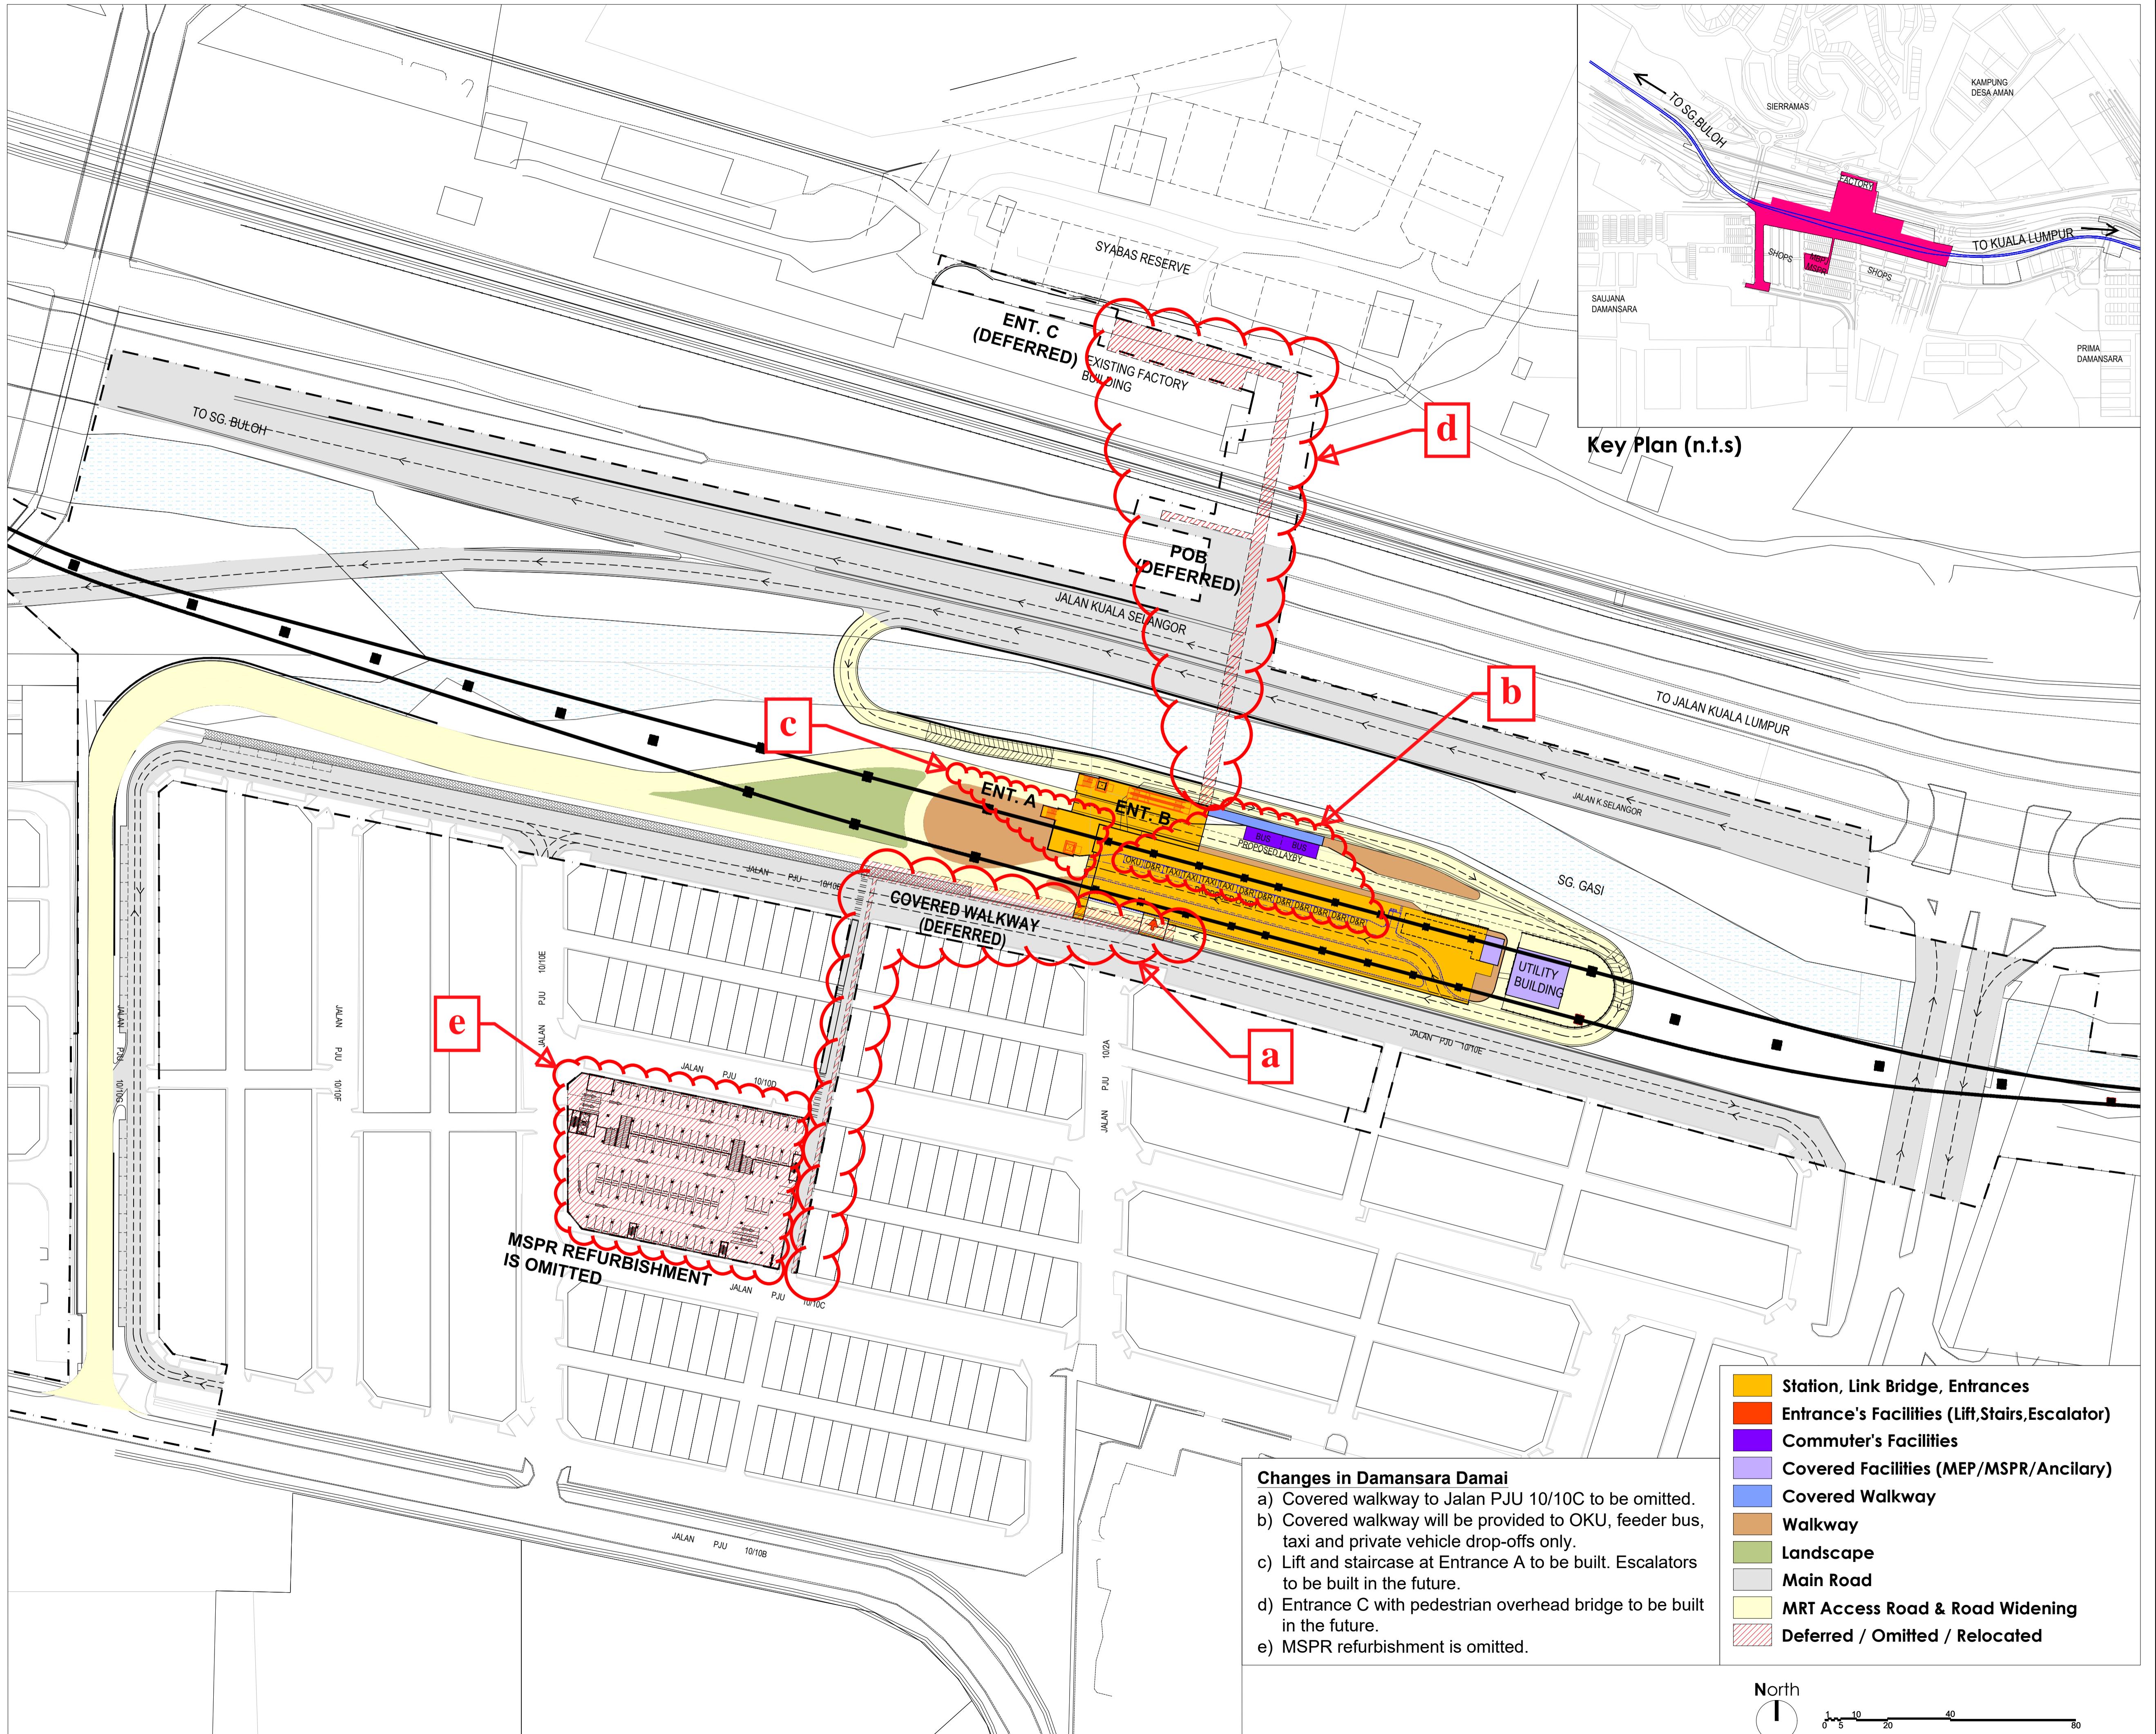

Drawing Title :  
S05  
DAMANSARA DAMAI

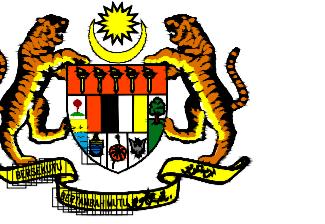

KERAJAAN MALAYSIA

PROJECT TITLE:  
PROJEK MASS RAPID TRANSIT LALUAN 2:  
PUTRAJAYA LINE  
(formerly known as PROJEK MRT LALUAN 2:  
SG BULOH - SERDANG - PUTRAJAYA (SSP))


PROJECT PACKAGE:  
ELEVATED NORTH

SUPERVISING AGENCY :  
AGENSI PENGANGKUTAN  
AWAM DARAT (APAD)  
LAND PUBLIC TRANSPORT  
A G E N C Y ( A P A D )

AGENSI PENGANGKUTAN AWAM DARAT  
(A.P.A.D.)

ARAS G, M DAN 20, MENARA TUN ISMAIL MOHAMED ALI,  
NO. 25, JALAN RAJA LAUT, 50350 KUALA LUMPUR,  
MALAYSIA.  
TEL (ARAS G): 603-2603 6700 / TEL (ARAS 20): 603-2603 6600

PROJECT OWNER :  
**MRT CORP**  
Mass Rapid Transit Corporation Sdn Bhd  
(902884-V)  
5th FLOOR MENARA I&P 1,  
JALAN DUNGUN, DAMANSARA HEIGHTS,  
50490 KUALA LUMPUR.

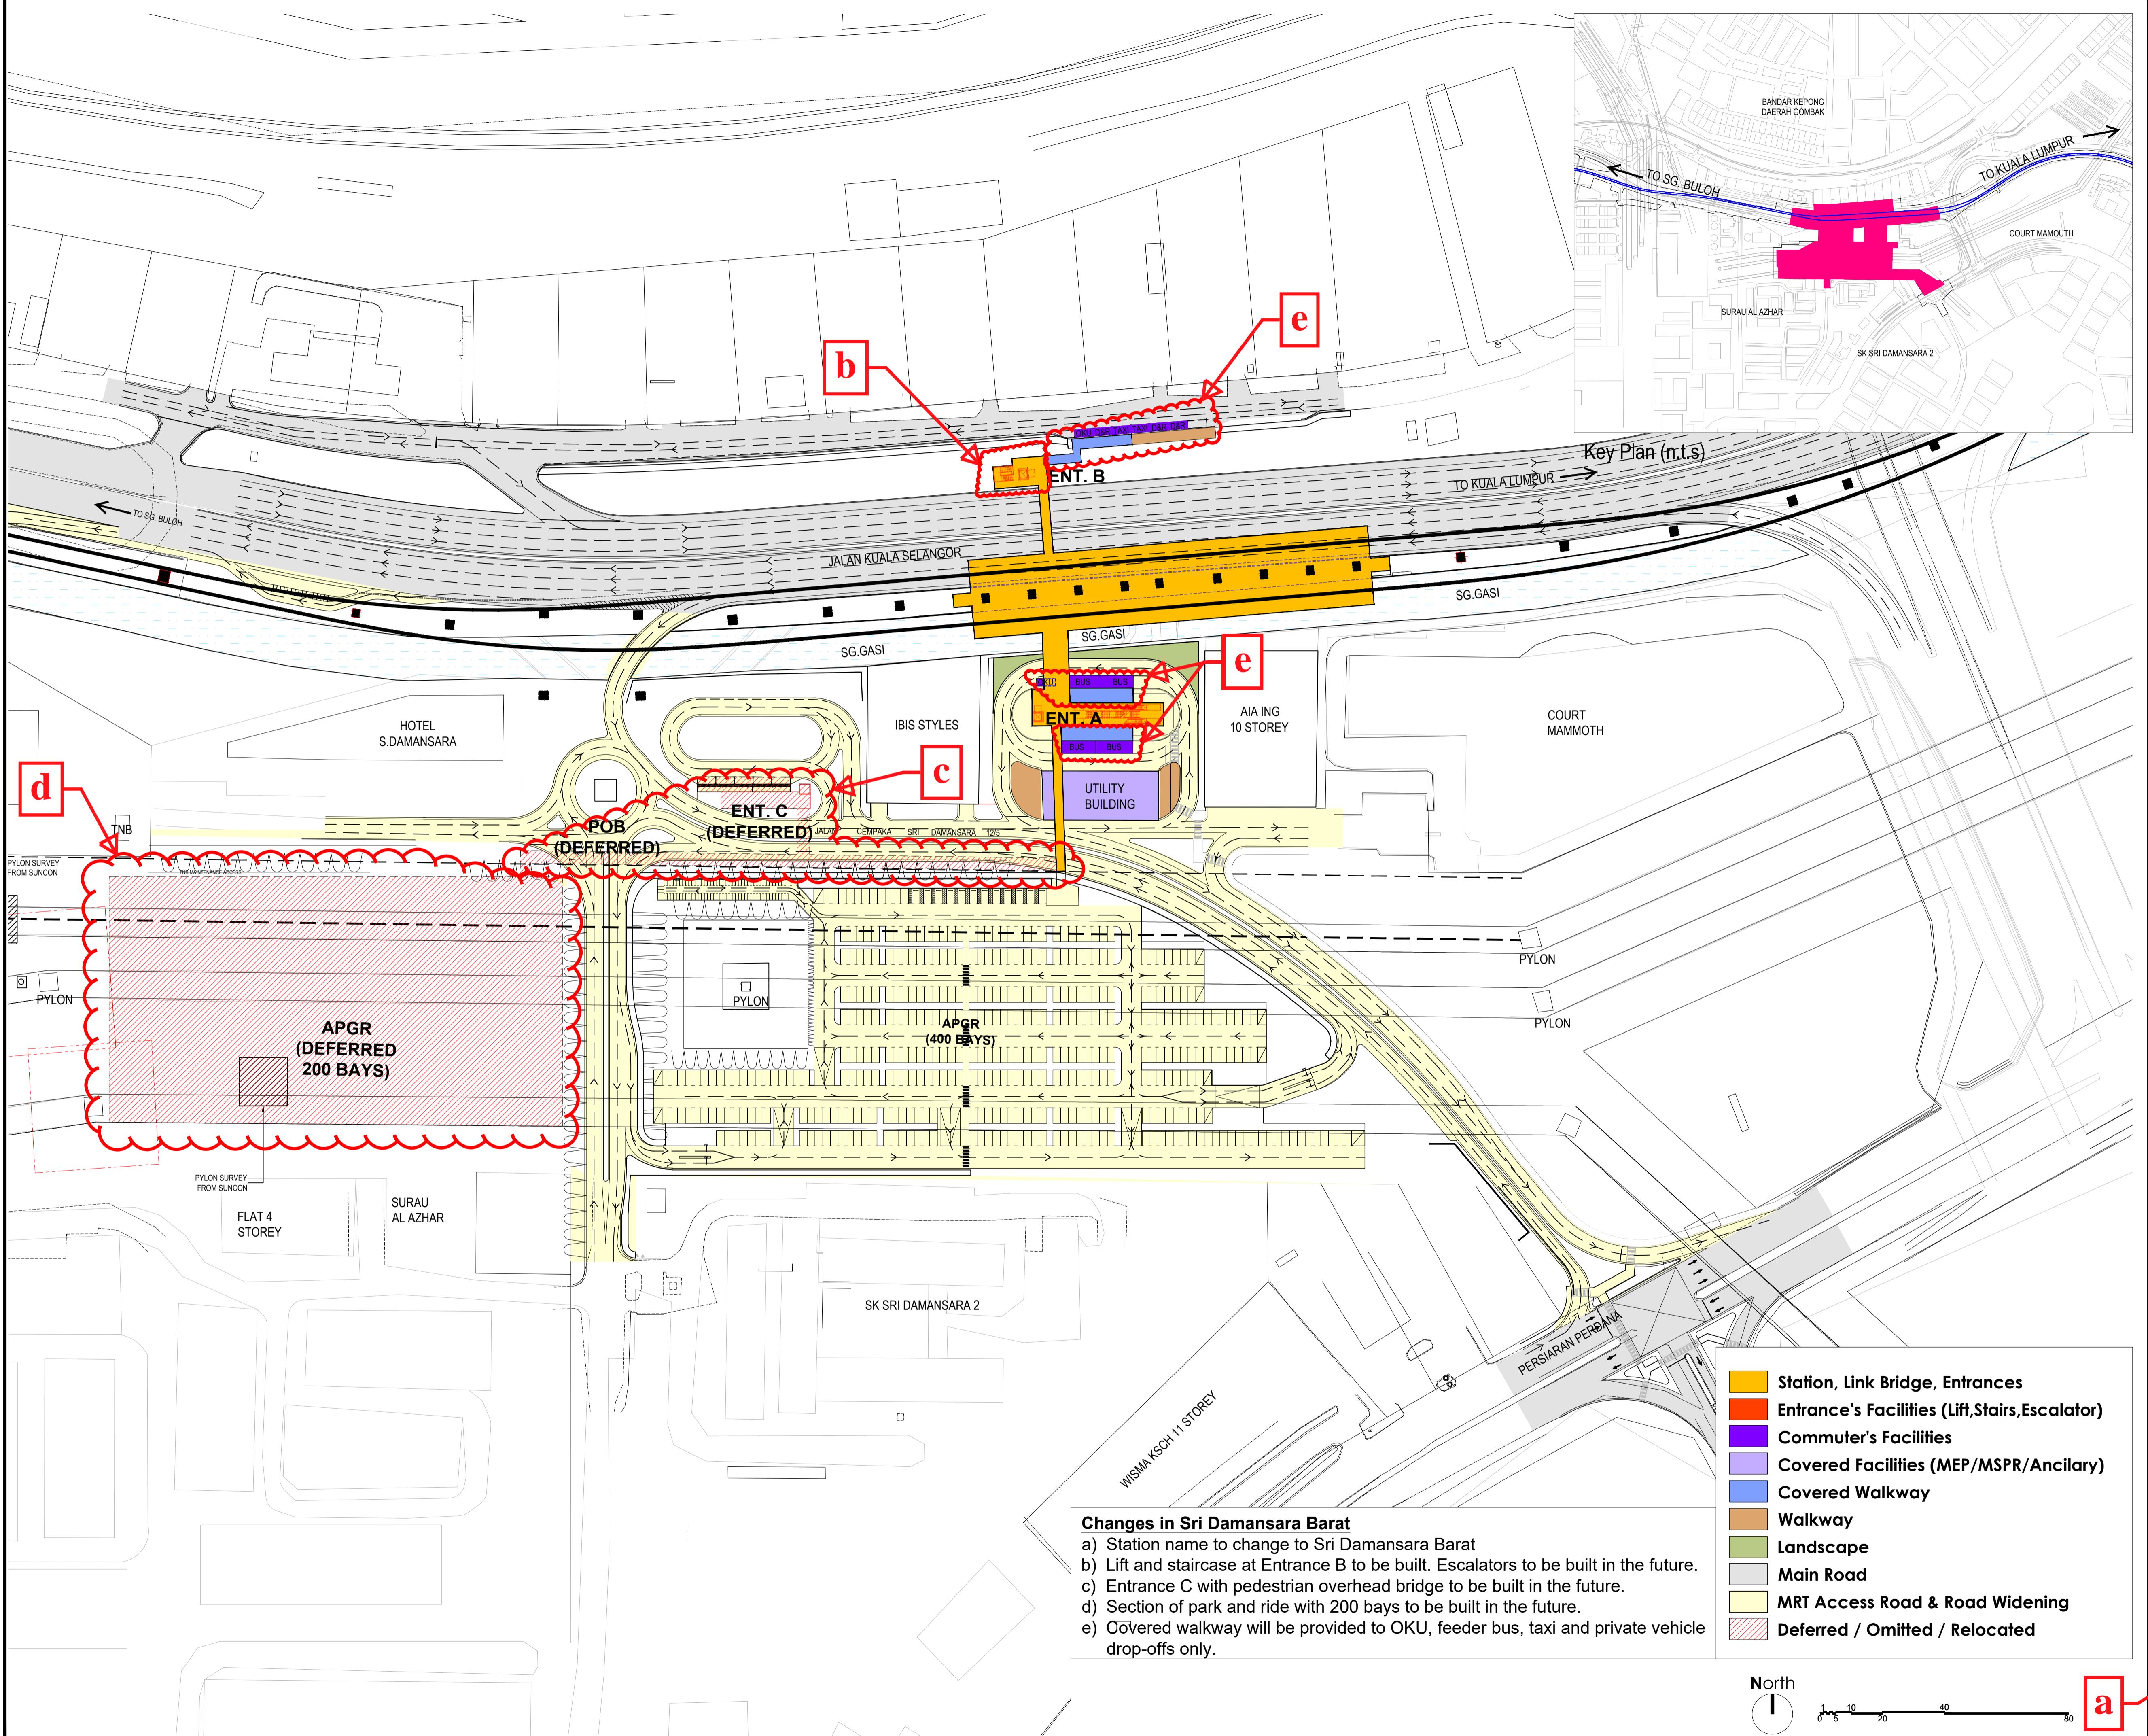

**Changes in Sri Damansara Barat**

- Station name to change to Sri Damansara Barat
- Lift and staircase at Entrance B to be built. Escalators to be built in the future.
- Entrance C with pedestrian overhead bridge to be built in the future.
- Section of park and ride with 200 bays to be built in the future.
- Covered walkway will be provided to OKU, feeder bus, taxi and private vehicle drop-offs only.


North



0 5 10 20 40 80

Drawing Title :

S06  
SRI DAMANSARA BARAT  
(PREVIOUSLY KNOWN AS  
SRI DAMANSARA WEST)

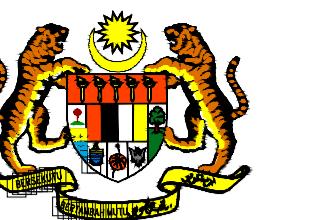

KERAJAAN MALAYSIA

PROJECT TITLE:  
PROJEK MASS RAPID TRANSIT LALUAN 2:  
PUTRAJAYA LINE  
(formerly known as PROJEK MRT LALUAN 2:  
SG BULOH - SERDANG - PUTRAJAYA (SSP))

PROJECT PACKAGE:


ELEVATED NORTH

SUPERVISING AGENCY :  
**AGENSI PENGANGKUTAN AWAM DARAT (APAD)**  
LAND PUBLIC TRANSPORT AGENCY (APAD)


**AGENSI PENGANGKUTAN AWAM DARAT (A.P.A.D.)**


ARAS G, M DAN 20, MENARA TUN ISMAIL MOHAMED ALI,  
NO. 25, JALAN RAJA LAUT, 50350 KUALA LUMPUR,  
MALAYSIA.  
TEL (ARAS G): 603-2603 6700 / TEL (ARAS 20): 603-2603 6600

PROJECT OWNER :  
**MRT CORP**  
Mass Rapid Transit Corporation Sdn Bhd  
(902884-V)  
5th FLOOR MENARA I&P 1,  
JALAN DUNGUN, DAMANSARA HEIGHTS,  
50490 KUALA LUMPUR.

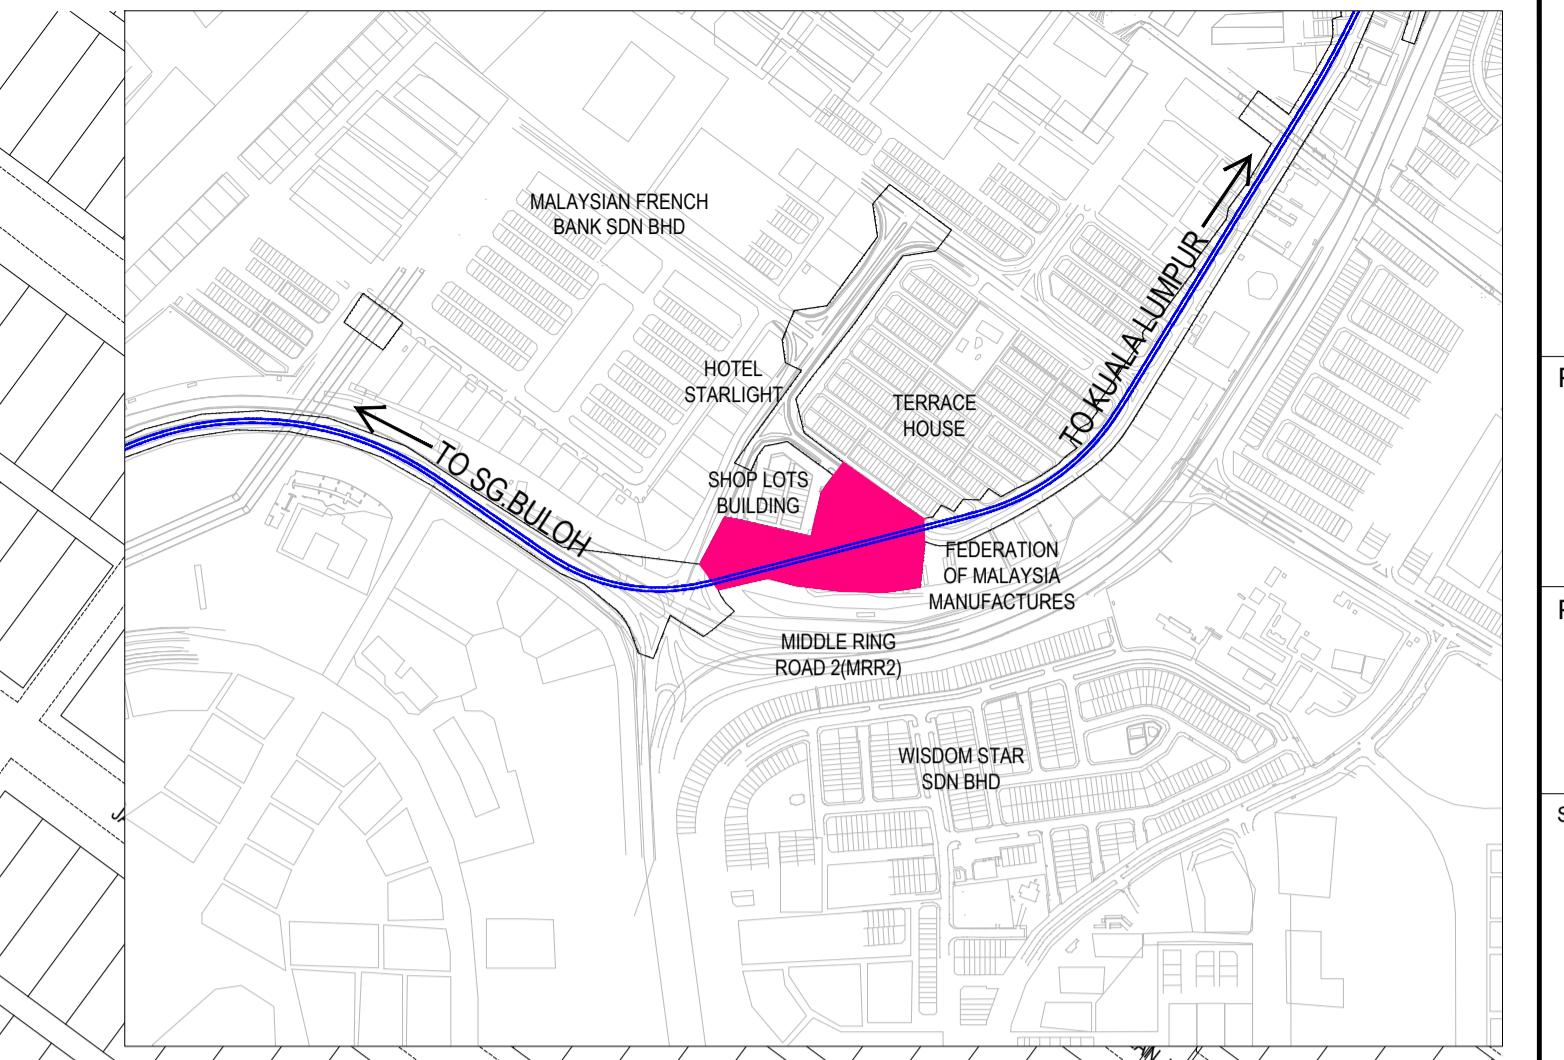

Key Plan (n.t.s)

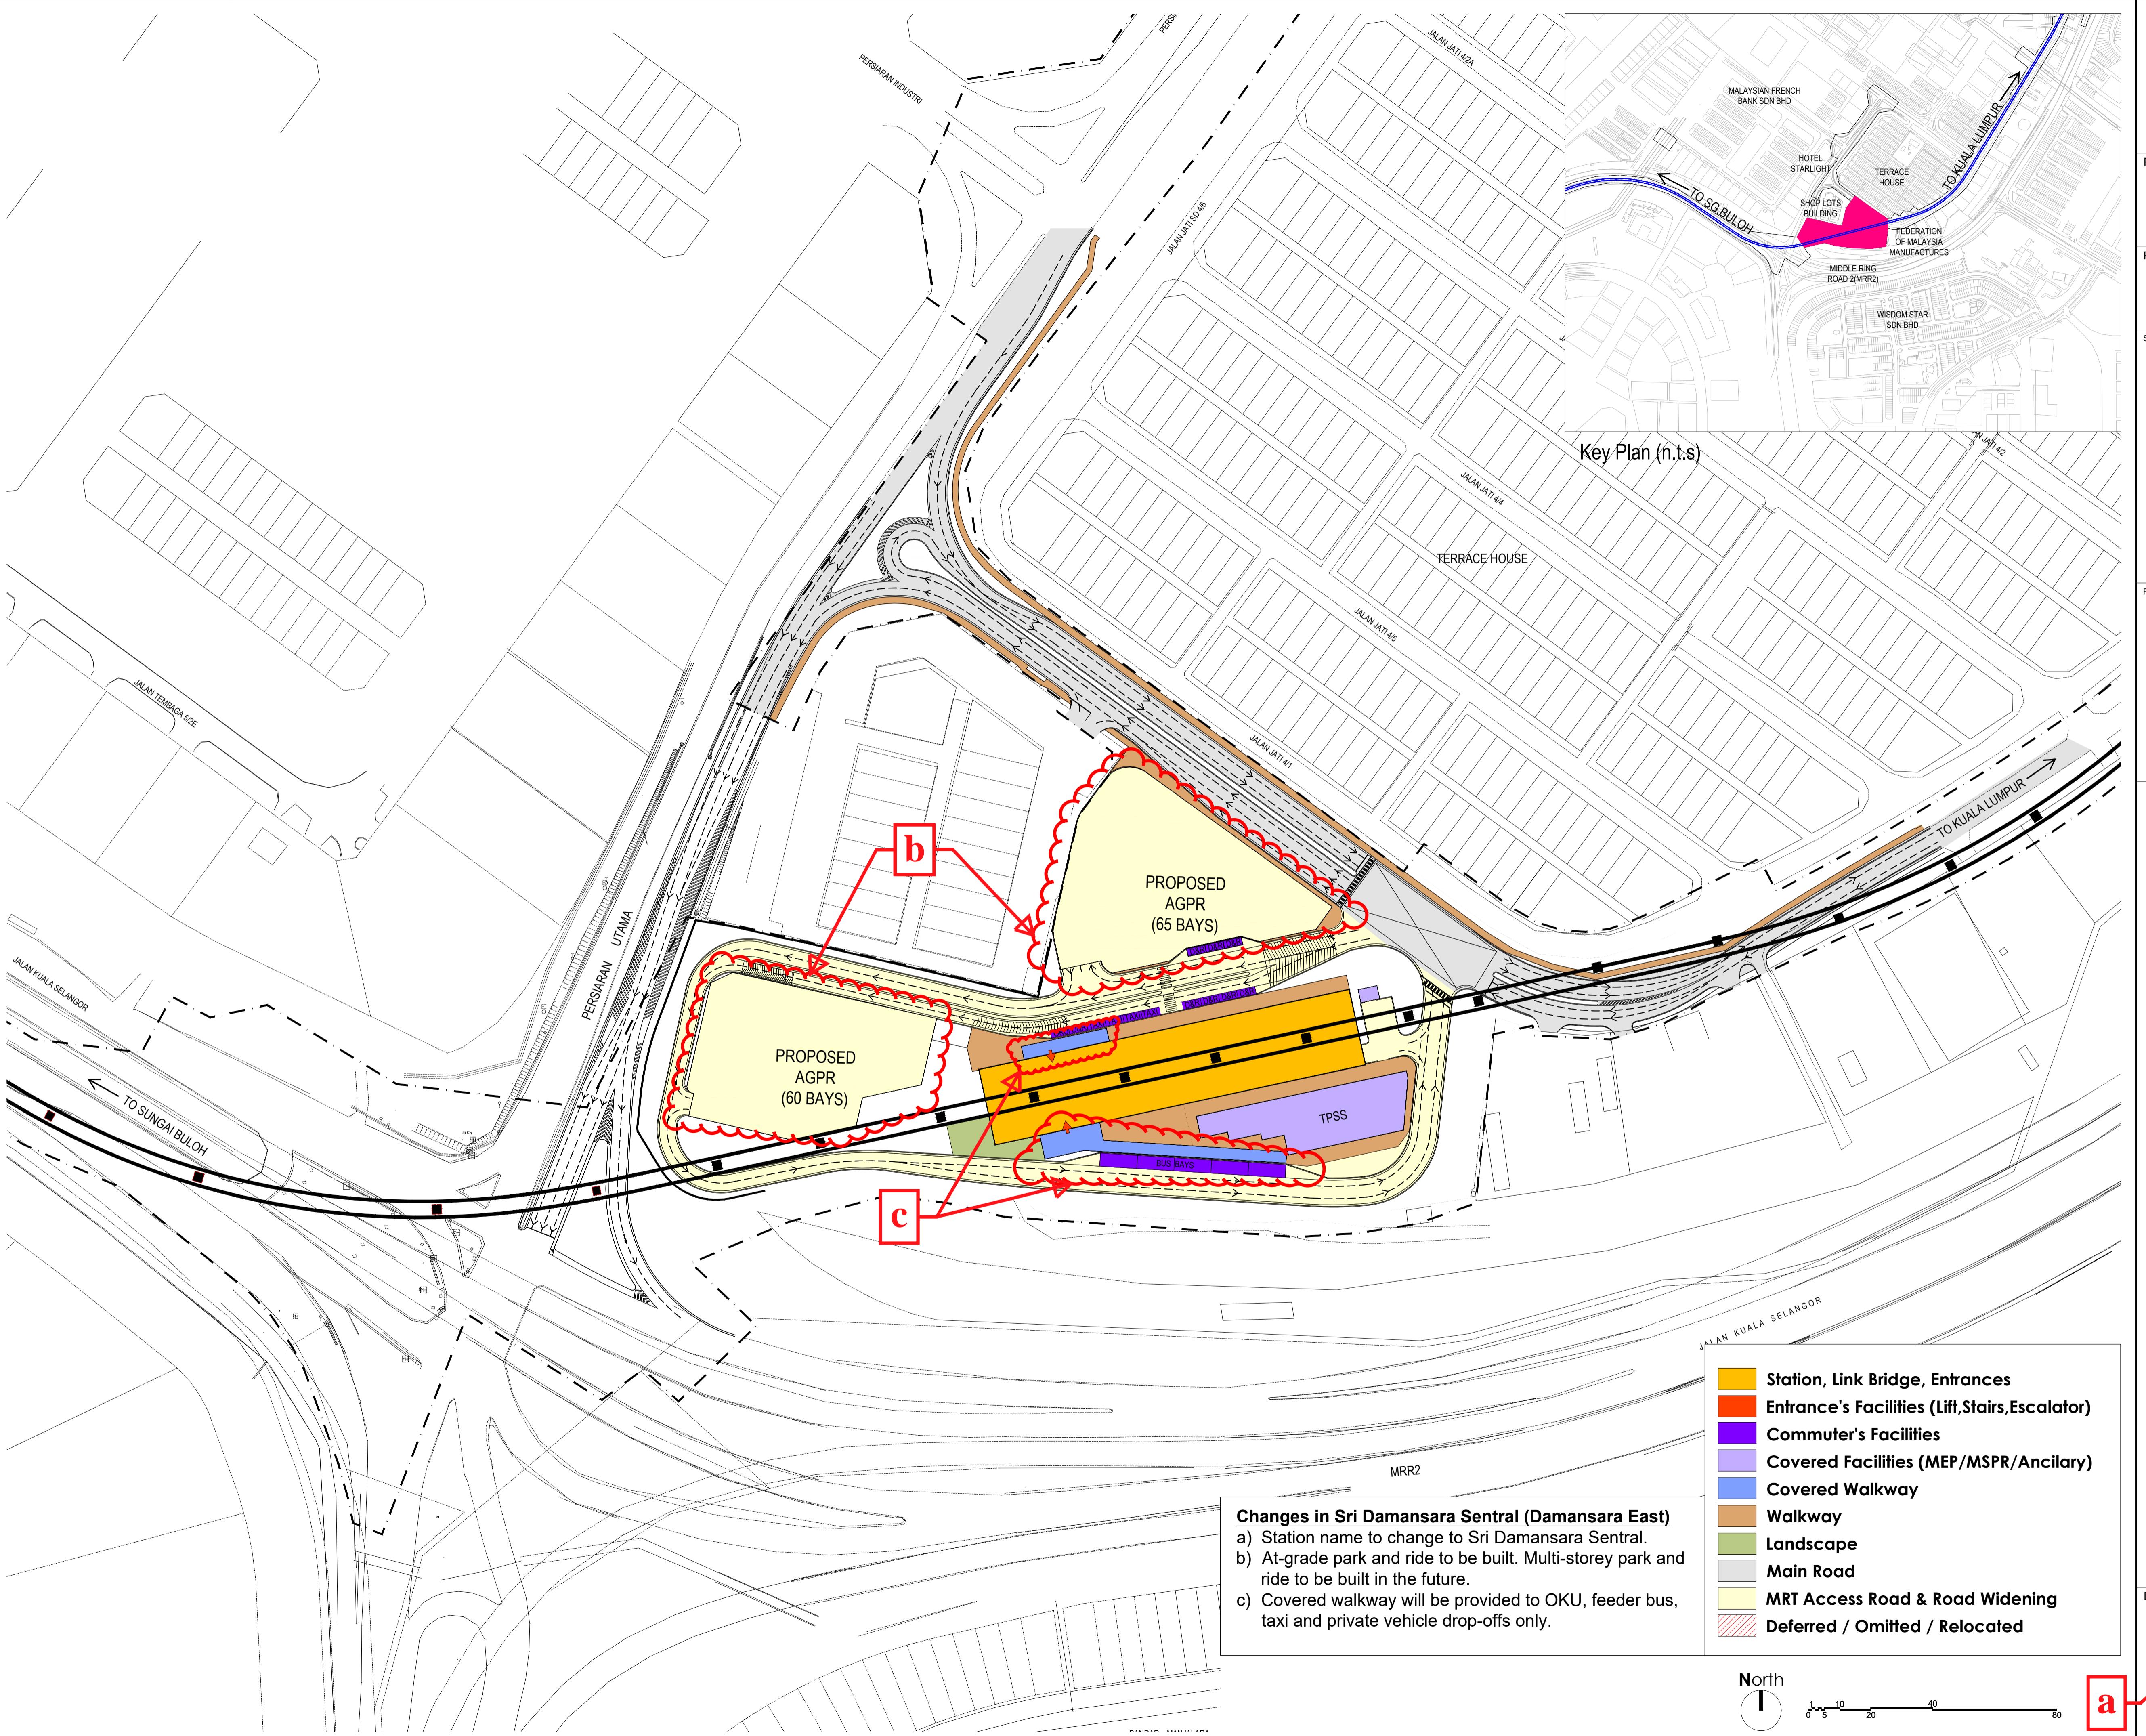

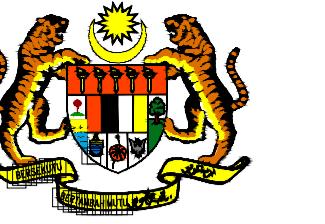

KERAJAAN MALAYSIA

PROJECT TITLE:  
PROJEK MASS RAPID TRANSIT LALUAN 2:  
PUTRAJAYA LINE  
(formerly known as PROJEK MRT LALUAN 2:  
SG BULOH - SERDANG - PUTRAJAYA (SSP))

PROJECT PACKAGE:  
ELEVATED NORTH


SUPERVISING AGENCY :  
**AGENSI PENGANGKUTAN AWAM DARAT (APAD)**  
LAND PUBLIC TRANSPORT AGENCY (APAD)

AGENSI PENGANGKUTAN AWAM DARAT  
(A.P.A.D.)

ARAS G, M DAN 20, MENARA TUN ISMAIL MOHAMED ALI,  
NO. 25, JALAN RAJA LAUT, 50350 KUALA LUMPUR,  
MALAYSIA.  
TEL (ARAS G): 603-2603 6700 / TEL (ARAS 20): 603-2603 6600

PROJECT OWNER :  
**MRT CORP**  
Mass Rapid Transit Corporation Sdn Bhd  
(902884-V)  
5th FLOOR MENARA I&P 1,  
JALAN DUNGUN, DAMANSARA HEIGHTS,  
50490 KUALA LUMPUR.

Key Plan (n.t.s)

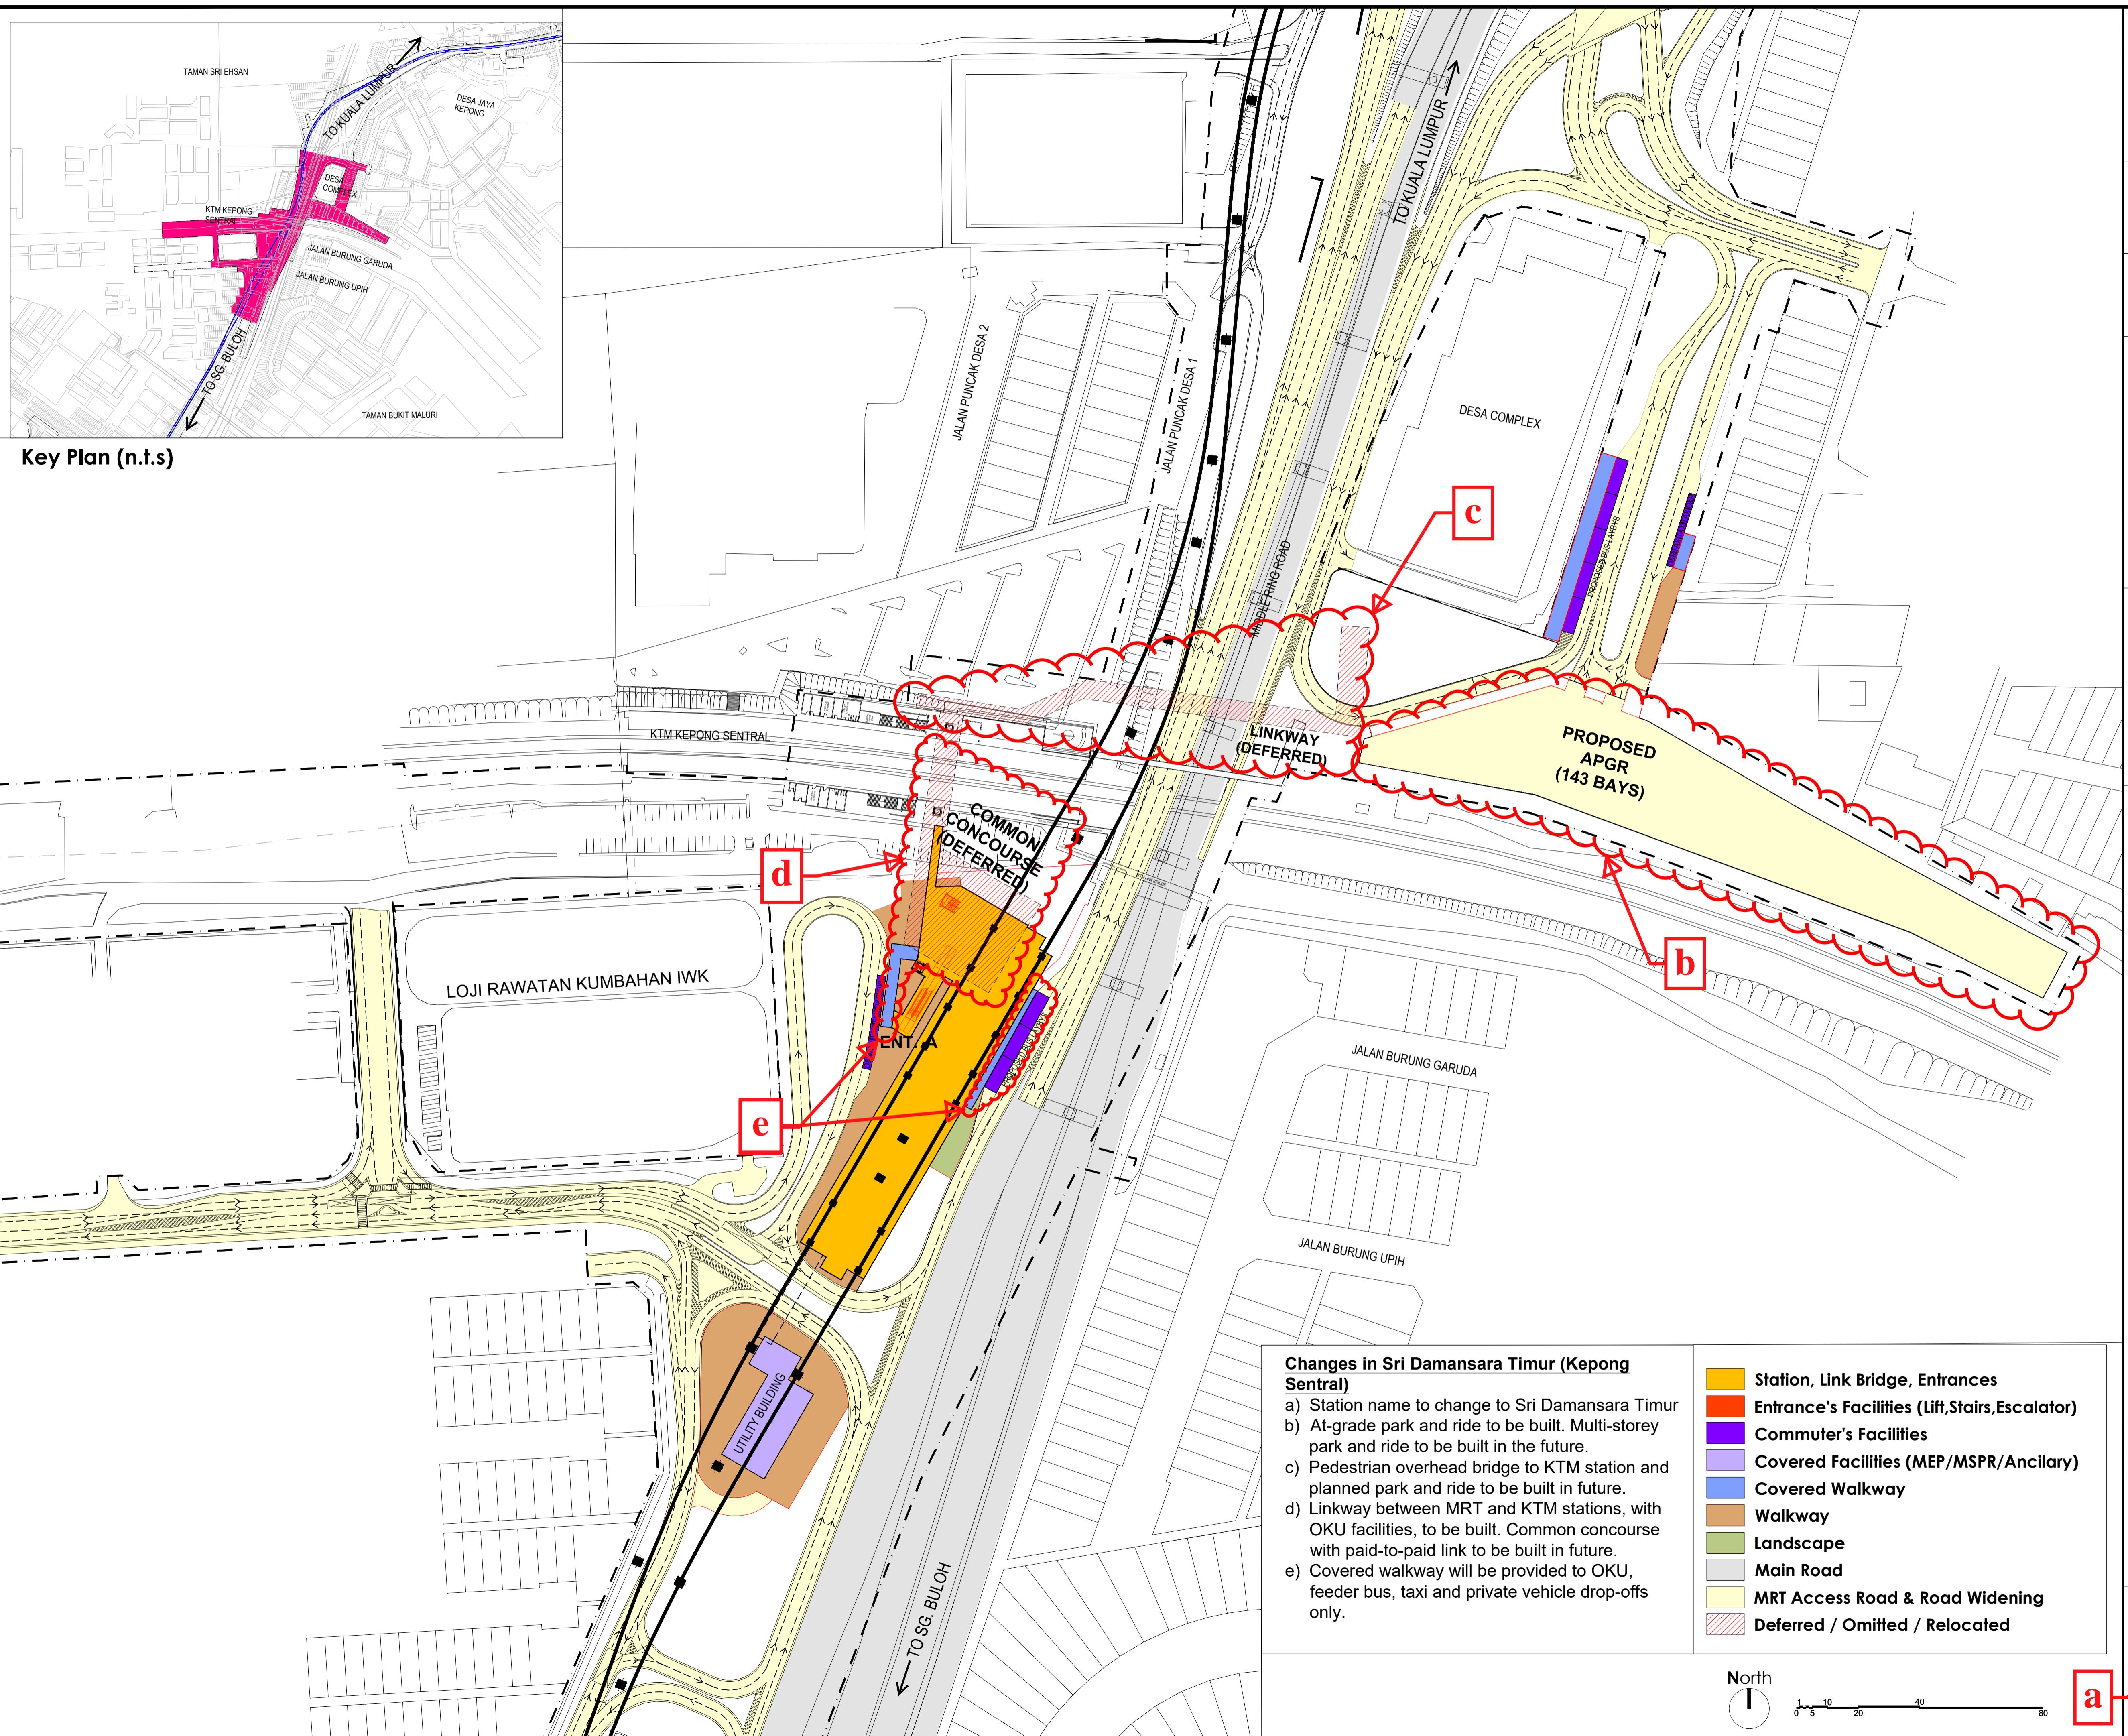

**Changes in Sri Damansara Timur (Kepong Sentral)**


- Station name to change to Sri Damansara Timur
- At-grade park and ride to be built. Multi-storey park and ride to be built in the future.
- Pedestrian overhead bridge to KTM station and planned park and ride to be built in future.
- Linkway between MRT and KTM stations, with OKU facilities, to be built. Common concourse with paid-to-paid link to be built in future.
- Covered walkway will be provided to OKU, feeder bus, taxi and private vehicle drop-offs only.

- Station, Link Bridge, Entrances
- Entrance's Facilities (Lift, Stairs, Escalator)
- Commuter's Facilities
- Covered Facilities (MEP/MSPR/Ancillary)
- Covered Walkway
- Walkway
- Landscape
- Main Road
- MRT Access Road & Road Widening
- Deferred / Omitted / Relocated

North

0 5 10 20 40 80

Drawing Title :  
S08  
SRI DAMANSARA TIMUR  
(PREVIOUSLY KNOWN AS  
KEPONG SENTRAL)

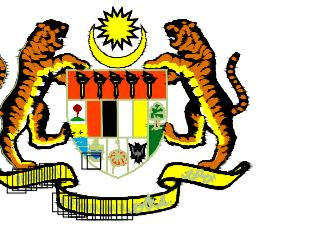

KERAJAAN MALAYSIA

PROJECT TITLE:  
PROJEK MASS RAPID TRANSIT LALUAN 2:  
PUTRAJAYA LINE  
(formerly known as PROJEK MRT LALUAN 2:  
SG BULOH - SERDANG - PUTRAJAYA (SSP))

PROJECT PACKAGE:


ELEVATED NORTH

SUPERVISING AGENCY :  
 AGENSI PENGANGKUTAN AWAM DARAT (APAD)  
LAND PUBLIC TRANSPORT AGENCY (APAD)


AGENSI PENGANGKUTAN AWAM DARAT  
(A.P.A.D.)

ARAS G, M DAN 20, MENARA TUN ISMAIL MOHAMED ALI,  
NO. 25, JALAN RAJA LAUT, 50350 KUALA LUMPUR,  
MALAYSIA.  
TEL (ARAS G): 603-2603 6700 / TEL (ARAS 20): 603-2603 6600

PROJECT OWNER :  
 MRT CORP  
Mass Rapid Transit Corporation Sdn Bhd  
(902884-V)  
5th FLOOR MENARA I&P 1,  
JALAN DUNGUN, DAMANSARA HEIGHTS,  
50490 KUALA LUMPUR.

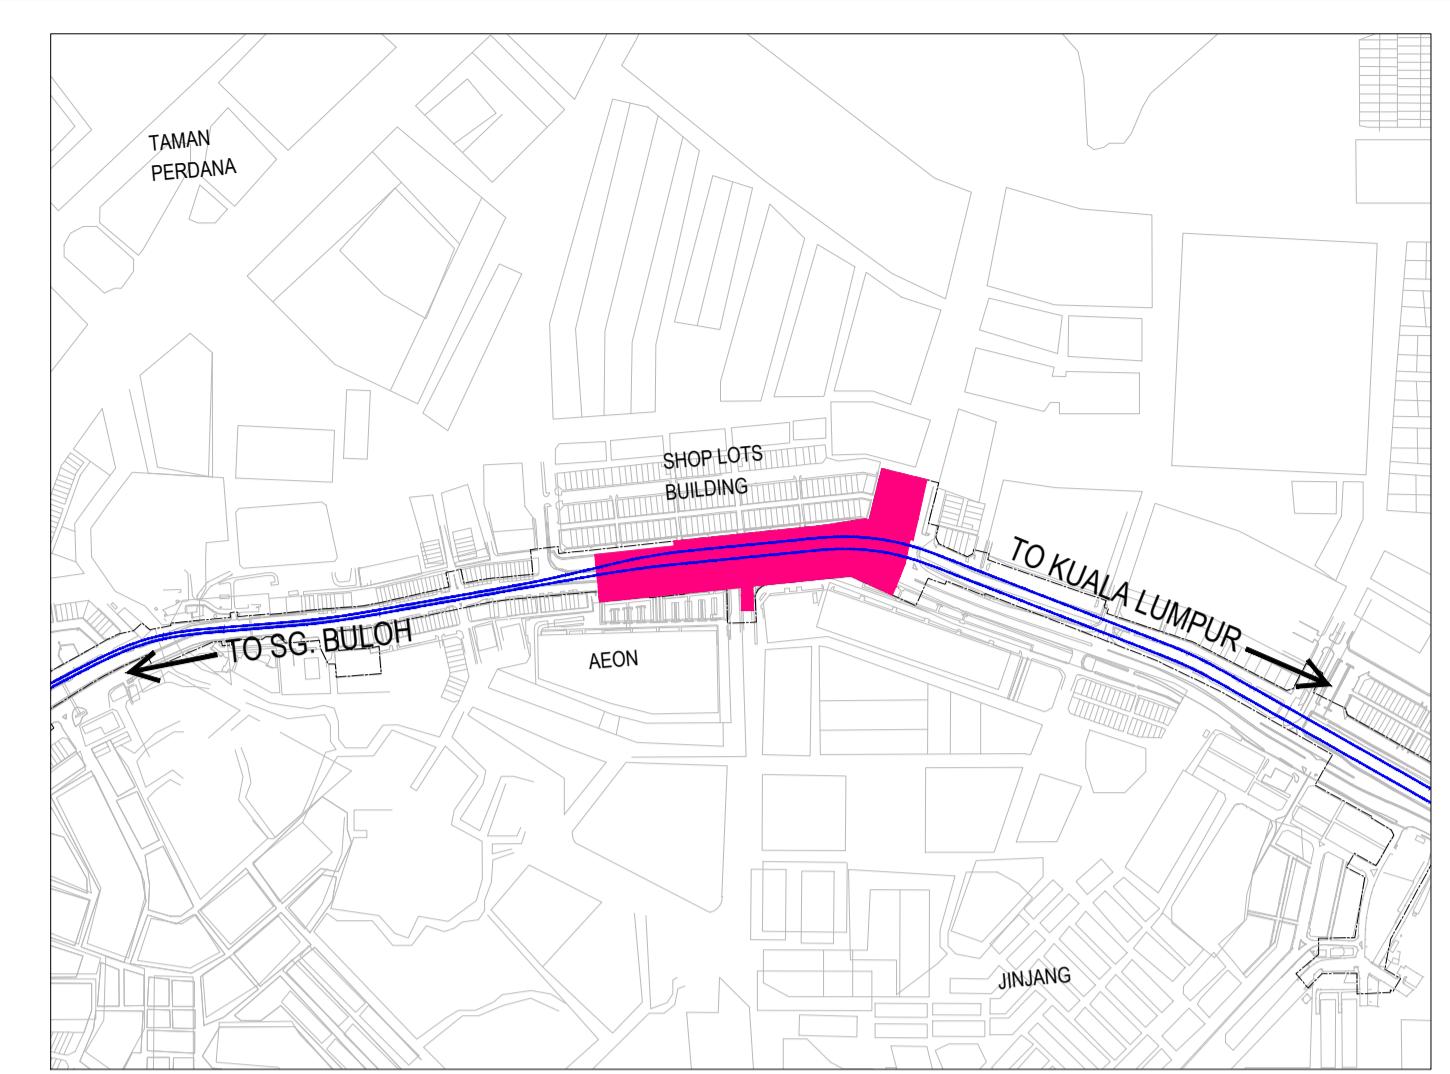

Key Plan (n.t.s)

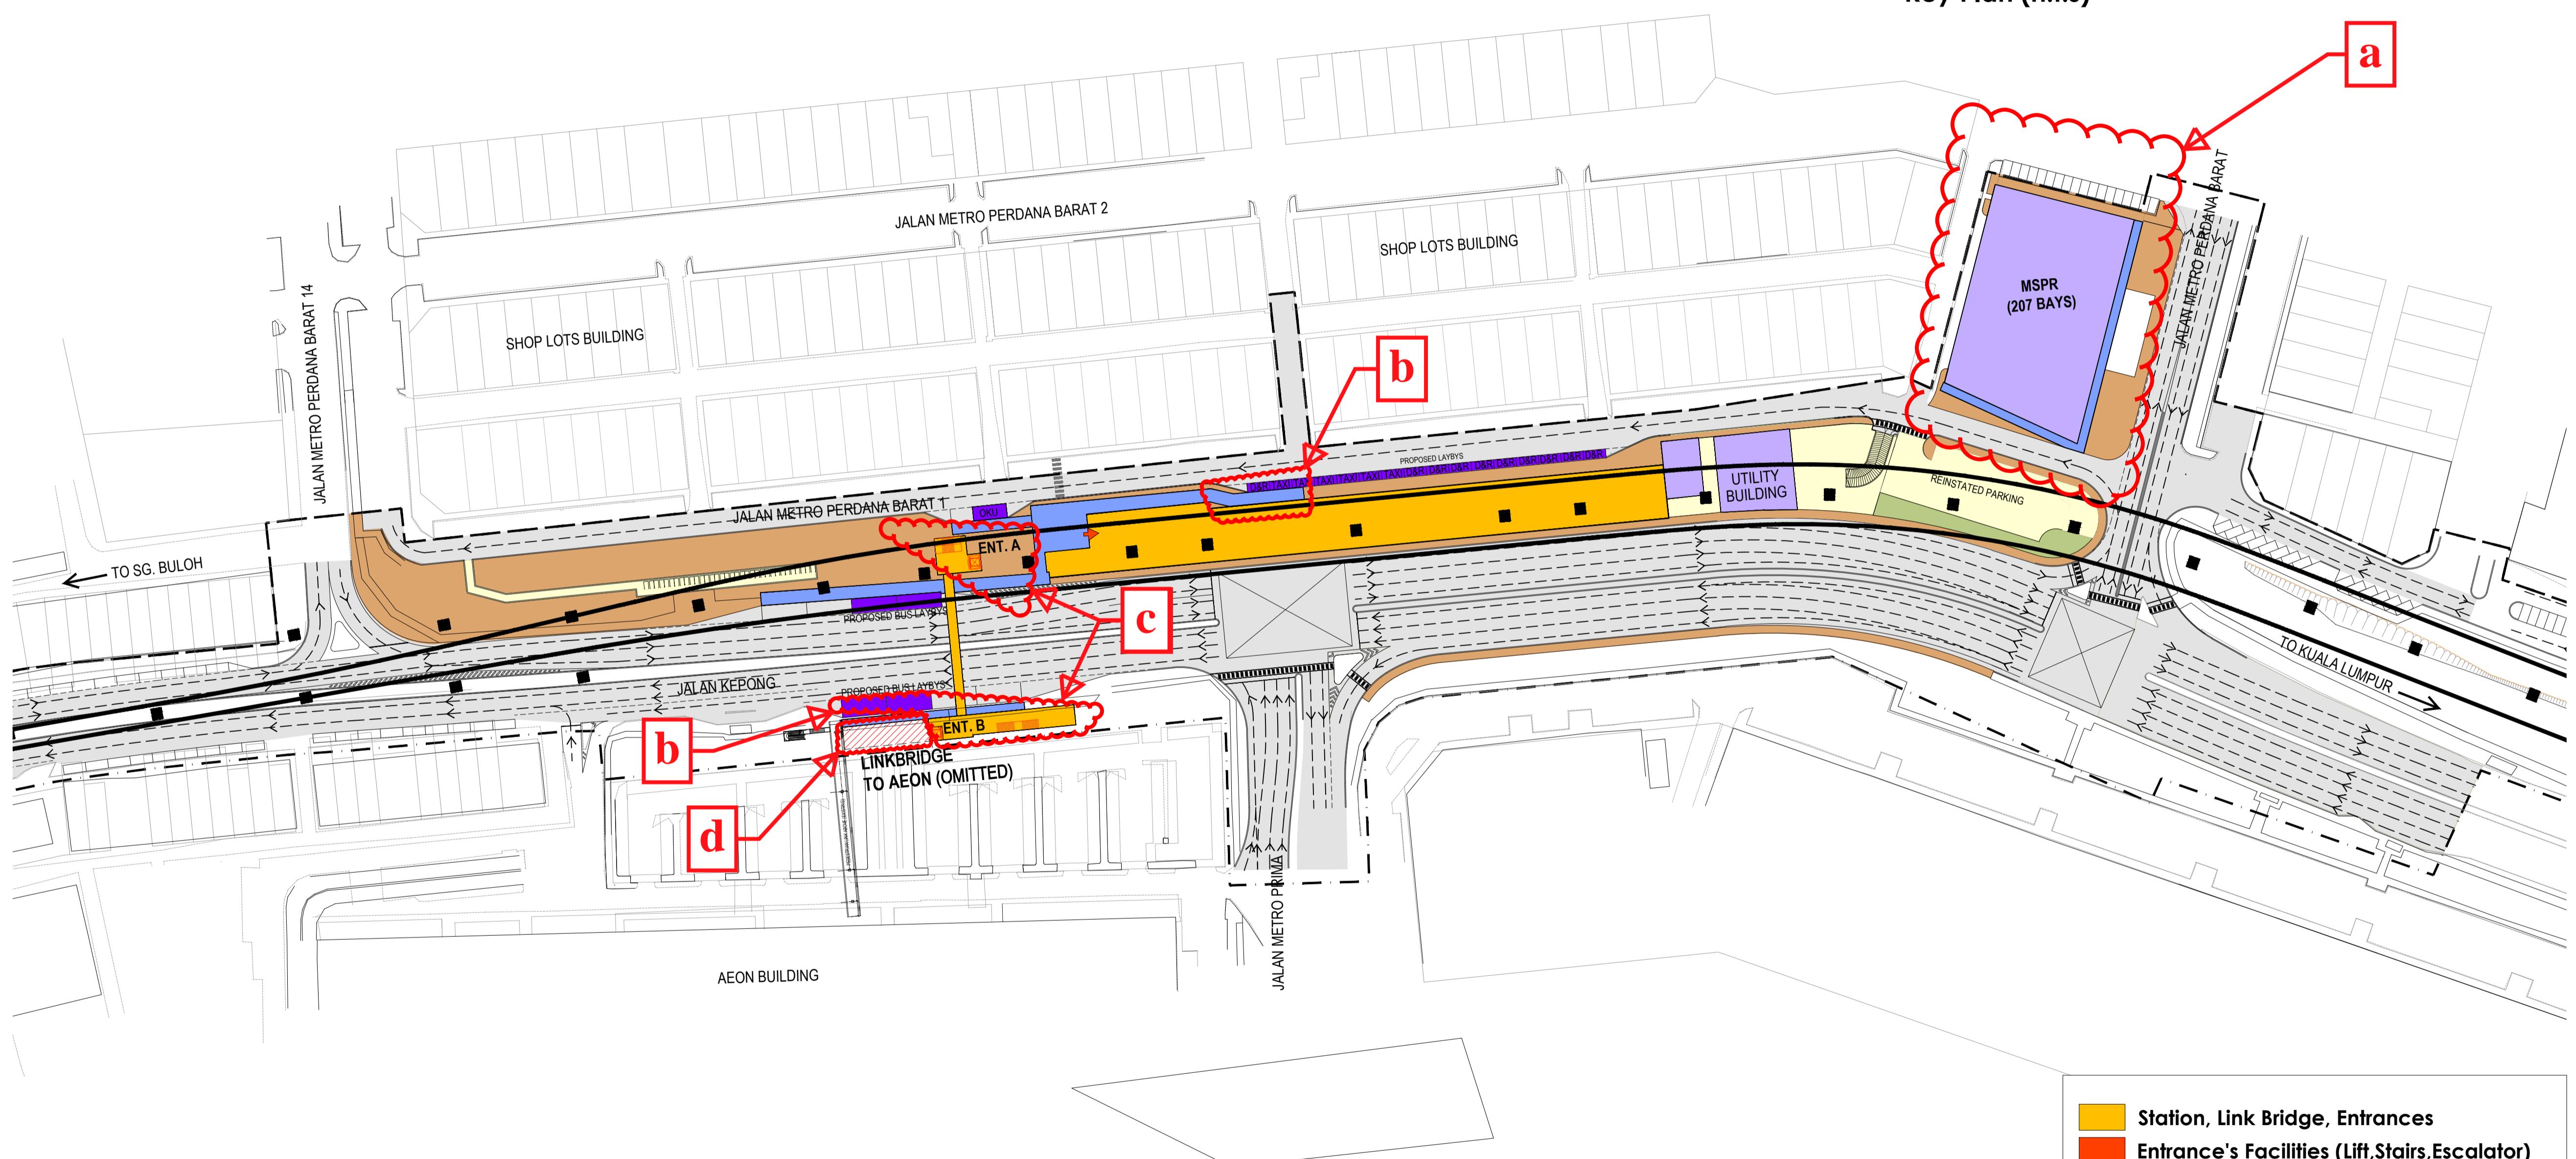


- Station, Link Bridge, Entrances
- Entrance's Facilities (Lift, Stairs, Escalator)
- Commuter's Facilities
- Covered Facilities (MEP/MSPR/Ancillary)
- Covered Walkway
- Walkway
- Landscape
- Main Road
- MRT Access Road & Road Widening
- Deferred / Omitted / Relocated

**Changes in Metro Prima**


- Multi storey park and ride to be reduced from 5 storeys to 3 storeys. Lift system to be built in the future.
- Covered walkway will be provided to OKU, feeder bus, taxi and private vehicle drop-offs only.
- Lift and staircase at Entrance A and B to be built. Escalators to be built in the future.
- Link bridge connecting Entrance B to AEON is omitted.

North

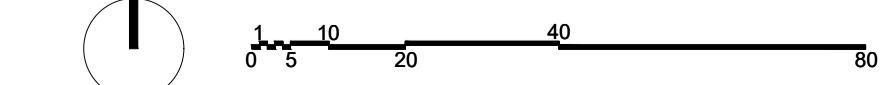

Drawing Title :

S09  
METRO PRIMA

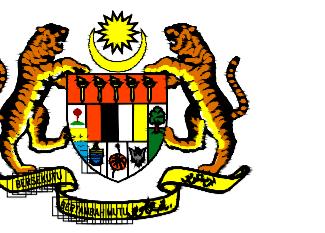

KERAJAAN MALAYSIA

PROJECT TITLE:  
PROJEK MASS RAPID TRANSIT LALUAN 2:  
PUTRAJAYA LINE  
(formerly known as PROJEK MRT LALUAN 2:  
SG BULOH - SERDANG - PUTRAJAYA (SSP))


PROJECT PACKAGE:  
ELEVATED NORTH

SUPERVISING AGENCY :  
**AGENSI PENGANGKUTAN AWAM DARAT (APAD)**  
LAND PUBLIC TRANSPORT AGENCY (APAD)


**AGENSI PENGANGKUTAN AWAM DARAT (A.P.A.D.)**

ARAS G, M DAN 20, MENARA TUN ISMAIL MOHAMED ALI,  
NO. 25, JALAN RAJA LAUT, 50350 KUALA LUMPUR,  
MALAYSIA.  
TEL (ARAS G): 603-2603 6700 / TEL (ARAS 20): 603-2603 6600


PROJECT OWNER :  
**MRT CORP**  
Mass Rapid Transit Corporation Sdn Bhd  
(902884-V)  
5th FLOOR MENARA I&P 1,  
JALAN DUNGUN, DAMANSARA HEIGHTS,  
50490 KUALA LUMPUR.

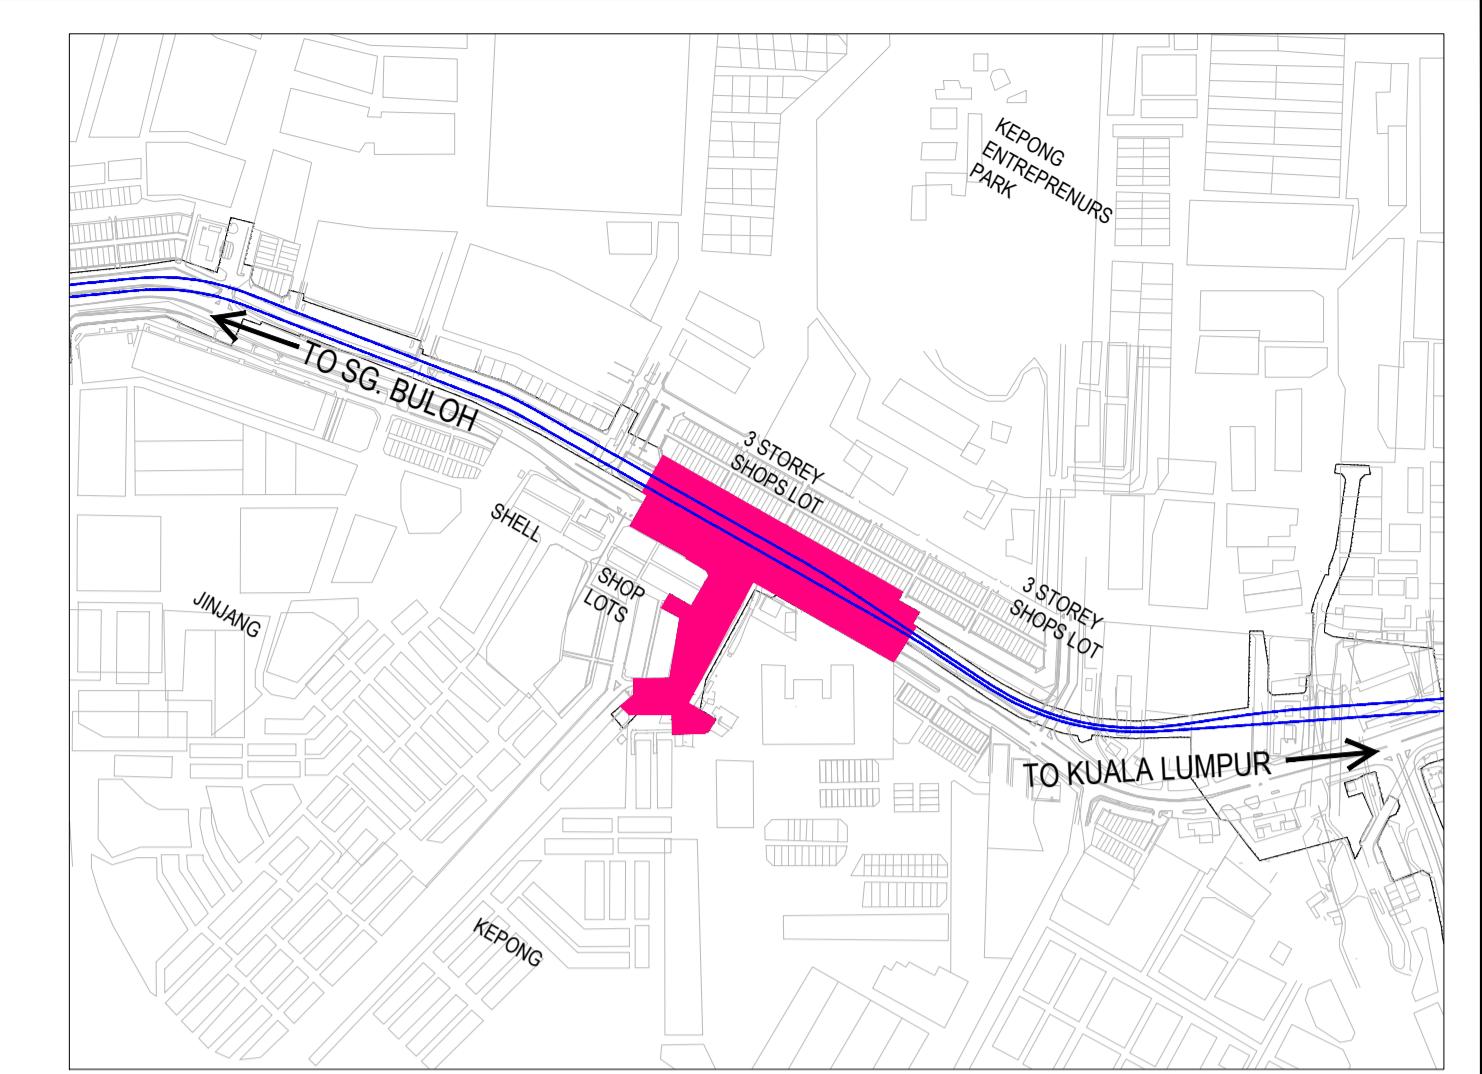

Key Plan (n.t.s)

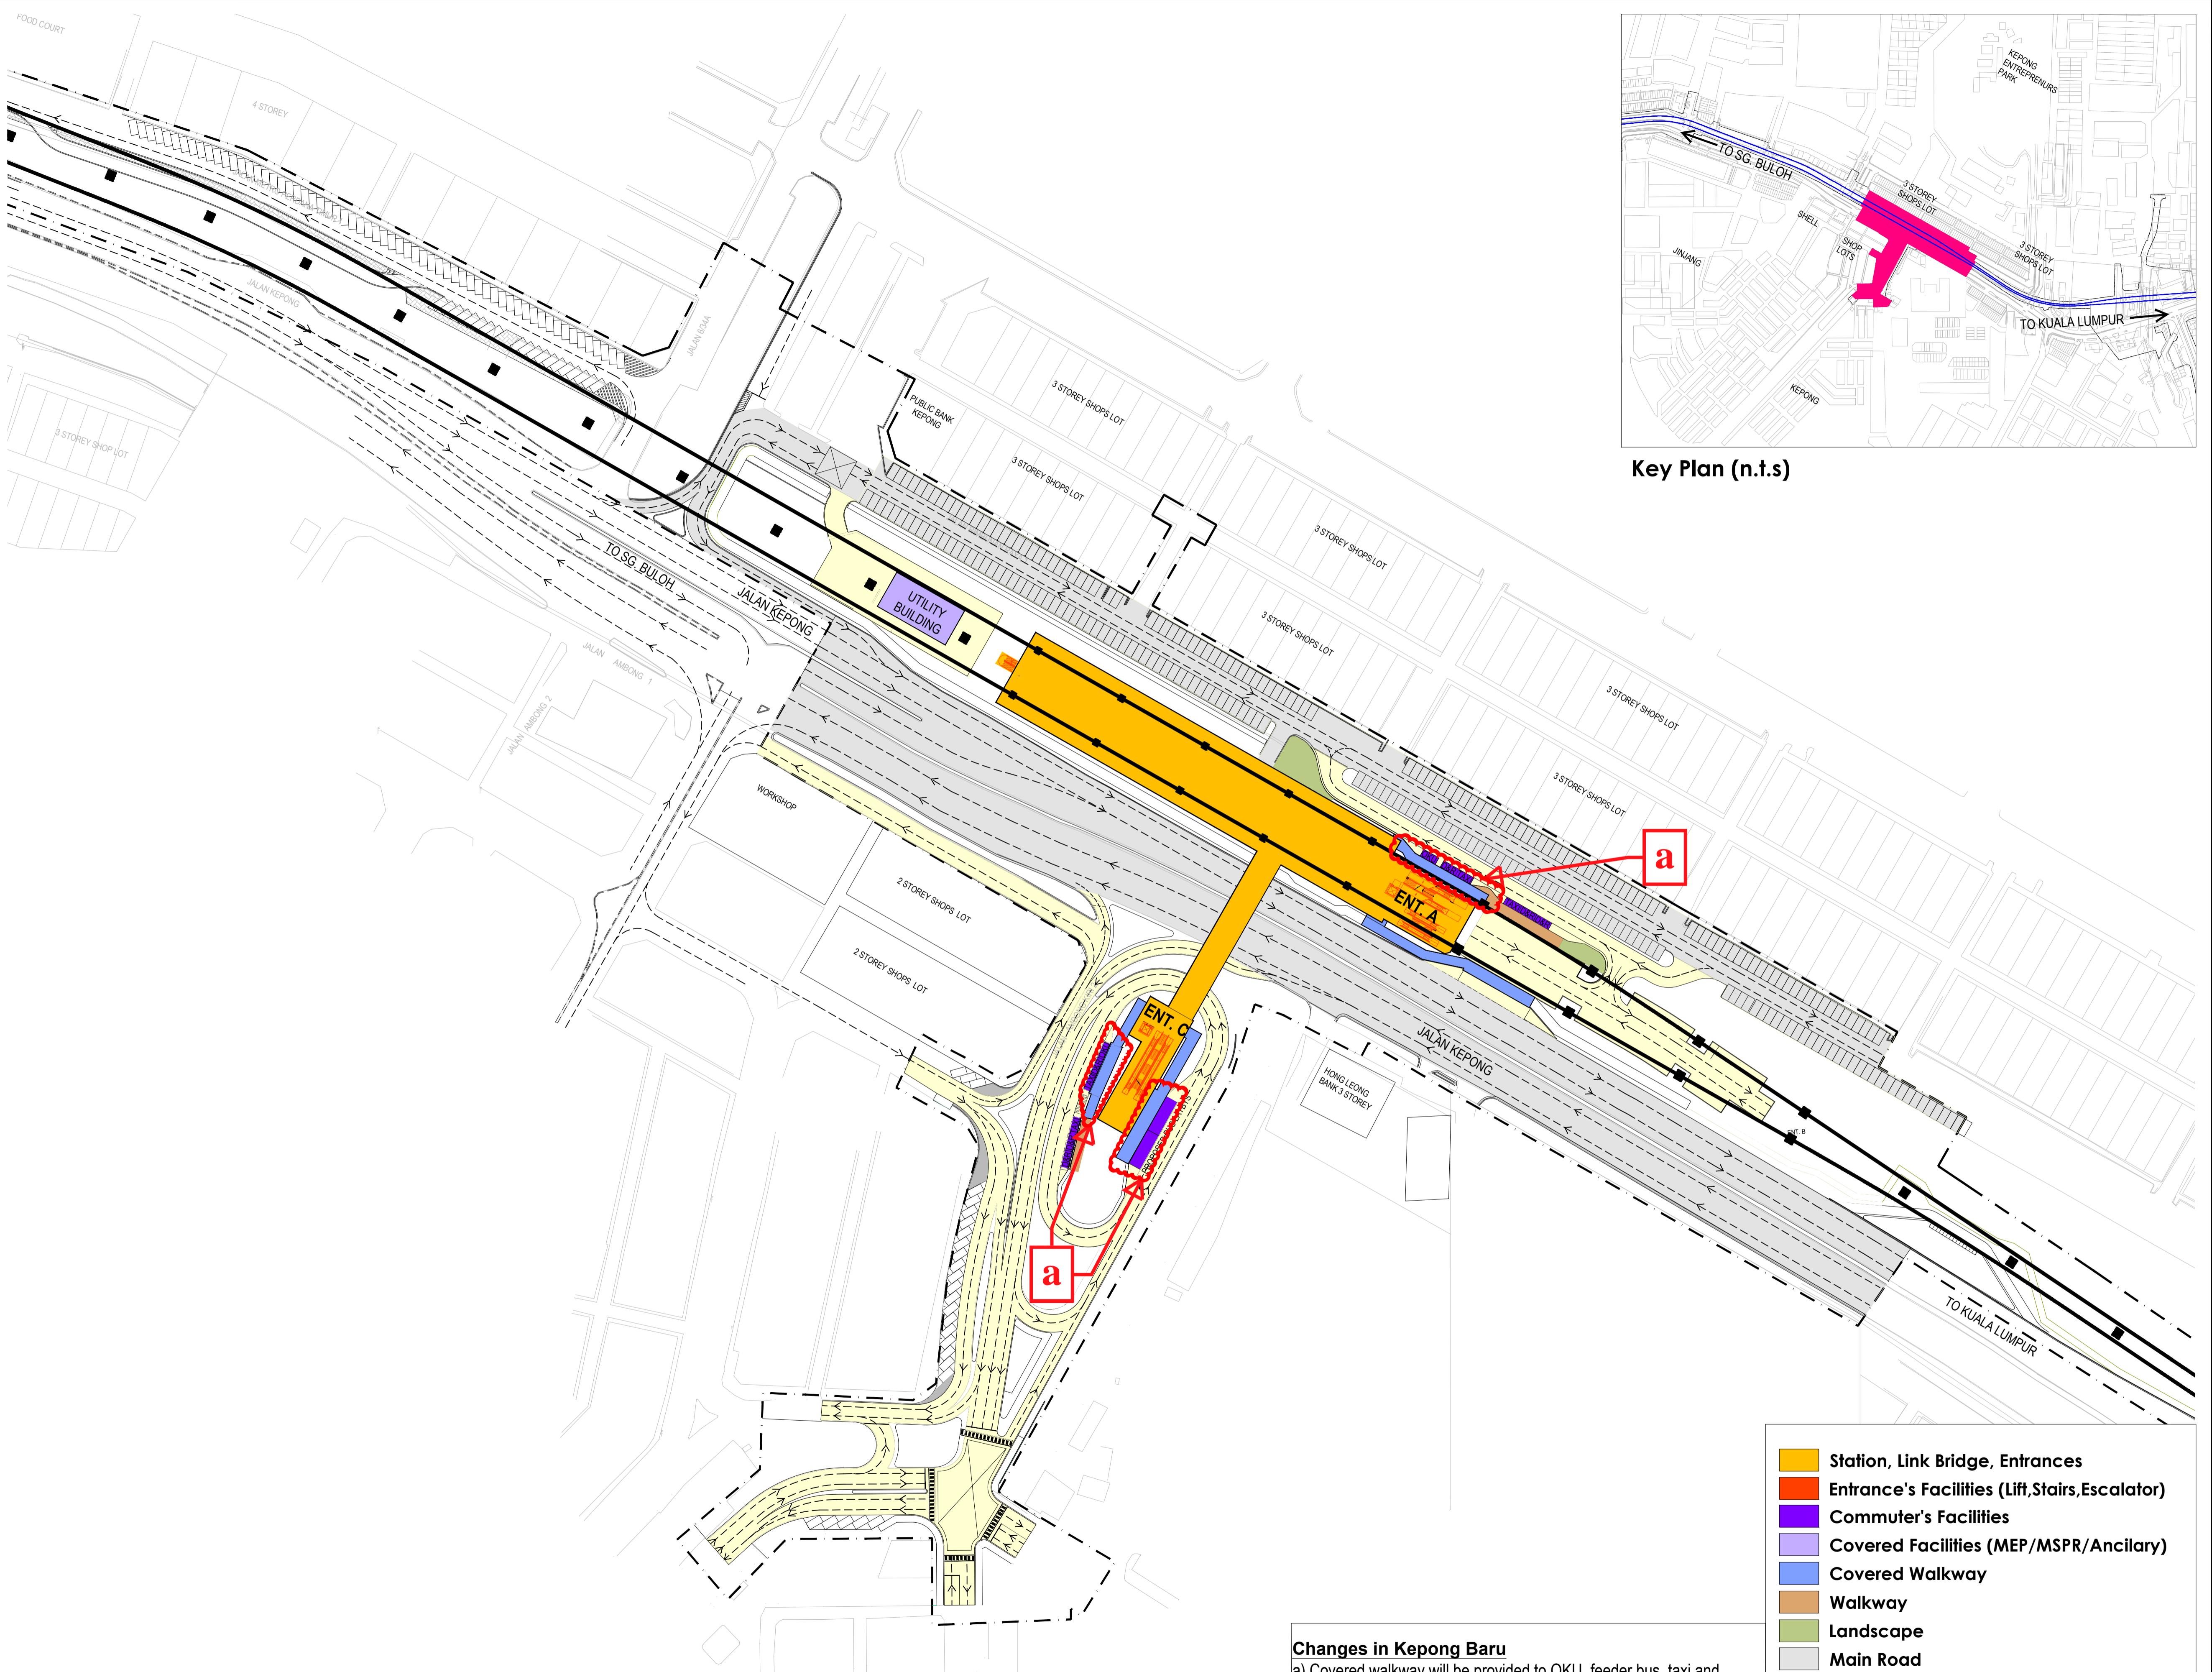


North

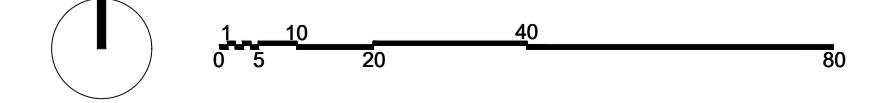

Drawing Title :

S10  
KEPONG BARU

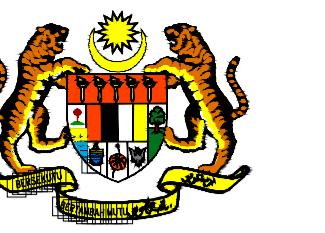

KERAJAAN MALAYSIA

PROJECT TITLE:  
PROJEK MASS RAPID TRANSIT LALUAN 2:  
PUTRAJAYA LINE  
(formerly known as PROJEK MRT LALUAN 2:  
SG BULOH - SERDANG - PUTRAJAYA (SSP))

PROJECT PACKAGE:


ELEVATED NORTH


SUPERVISING AGENCY :  
**AGENSI PENGANGKUTAN AWAM DARAT (APAD)**  
LAND PUBLIC TRANSPORT AGENCY (APAD)

AGENSI PENGANGKUTAN AWAM DARAT (A.P.A.D.)

ARAS G, M DAN 20, MENARA TUN ISMAIL MOHAMED ALI,  
NO. 25, JALAN RAJA LAUT, 50350 KUALA LUMPUR,  
MALAYSIA.  
TEL (ARAS G): 603-2603 6700 / TEL (ARAS 20): 603-2603 6600

PROJECT OWNER :  
**MRT CORP**  
Mass Rapid Transit Corporation Sdn Bhd  
(902884-V)  
5th FLOOR MENARA I&P 1,  
JALAN DUNGUN, DAMANSARA HEIGHTS,  
50490 KUALA LUMPUR.

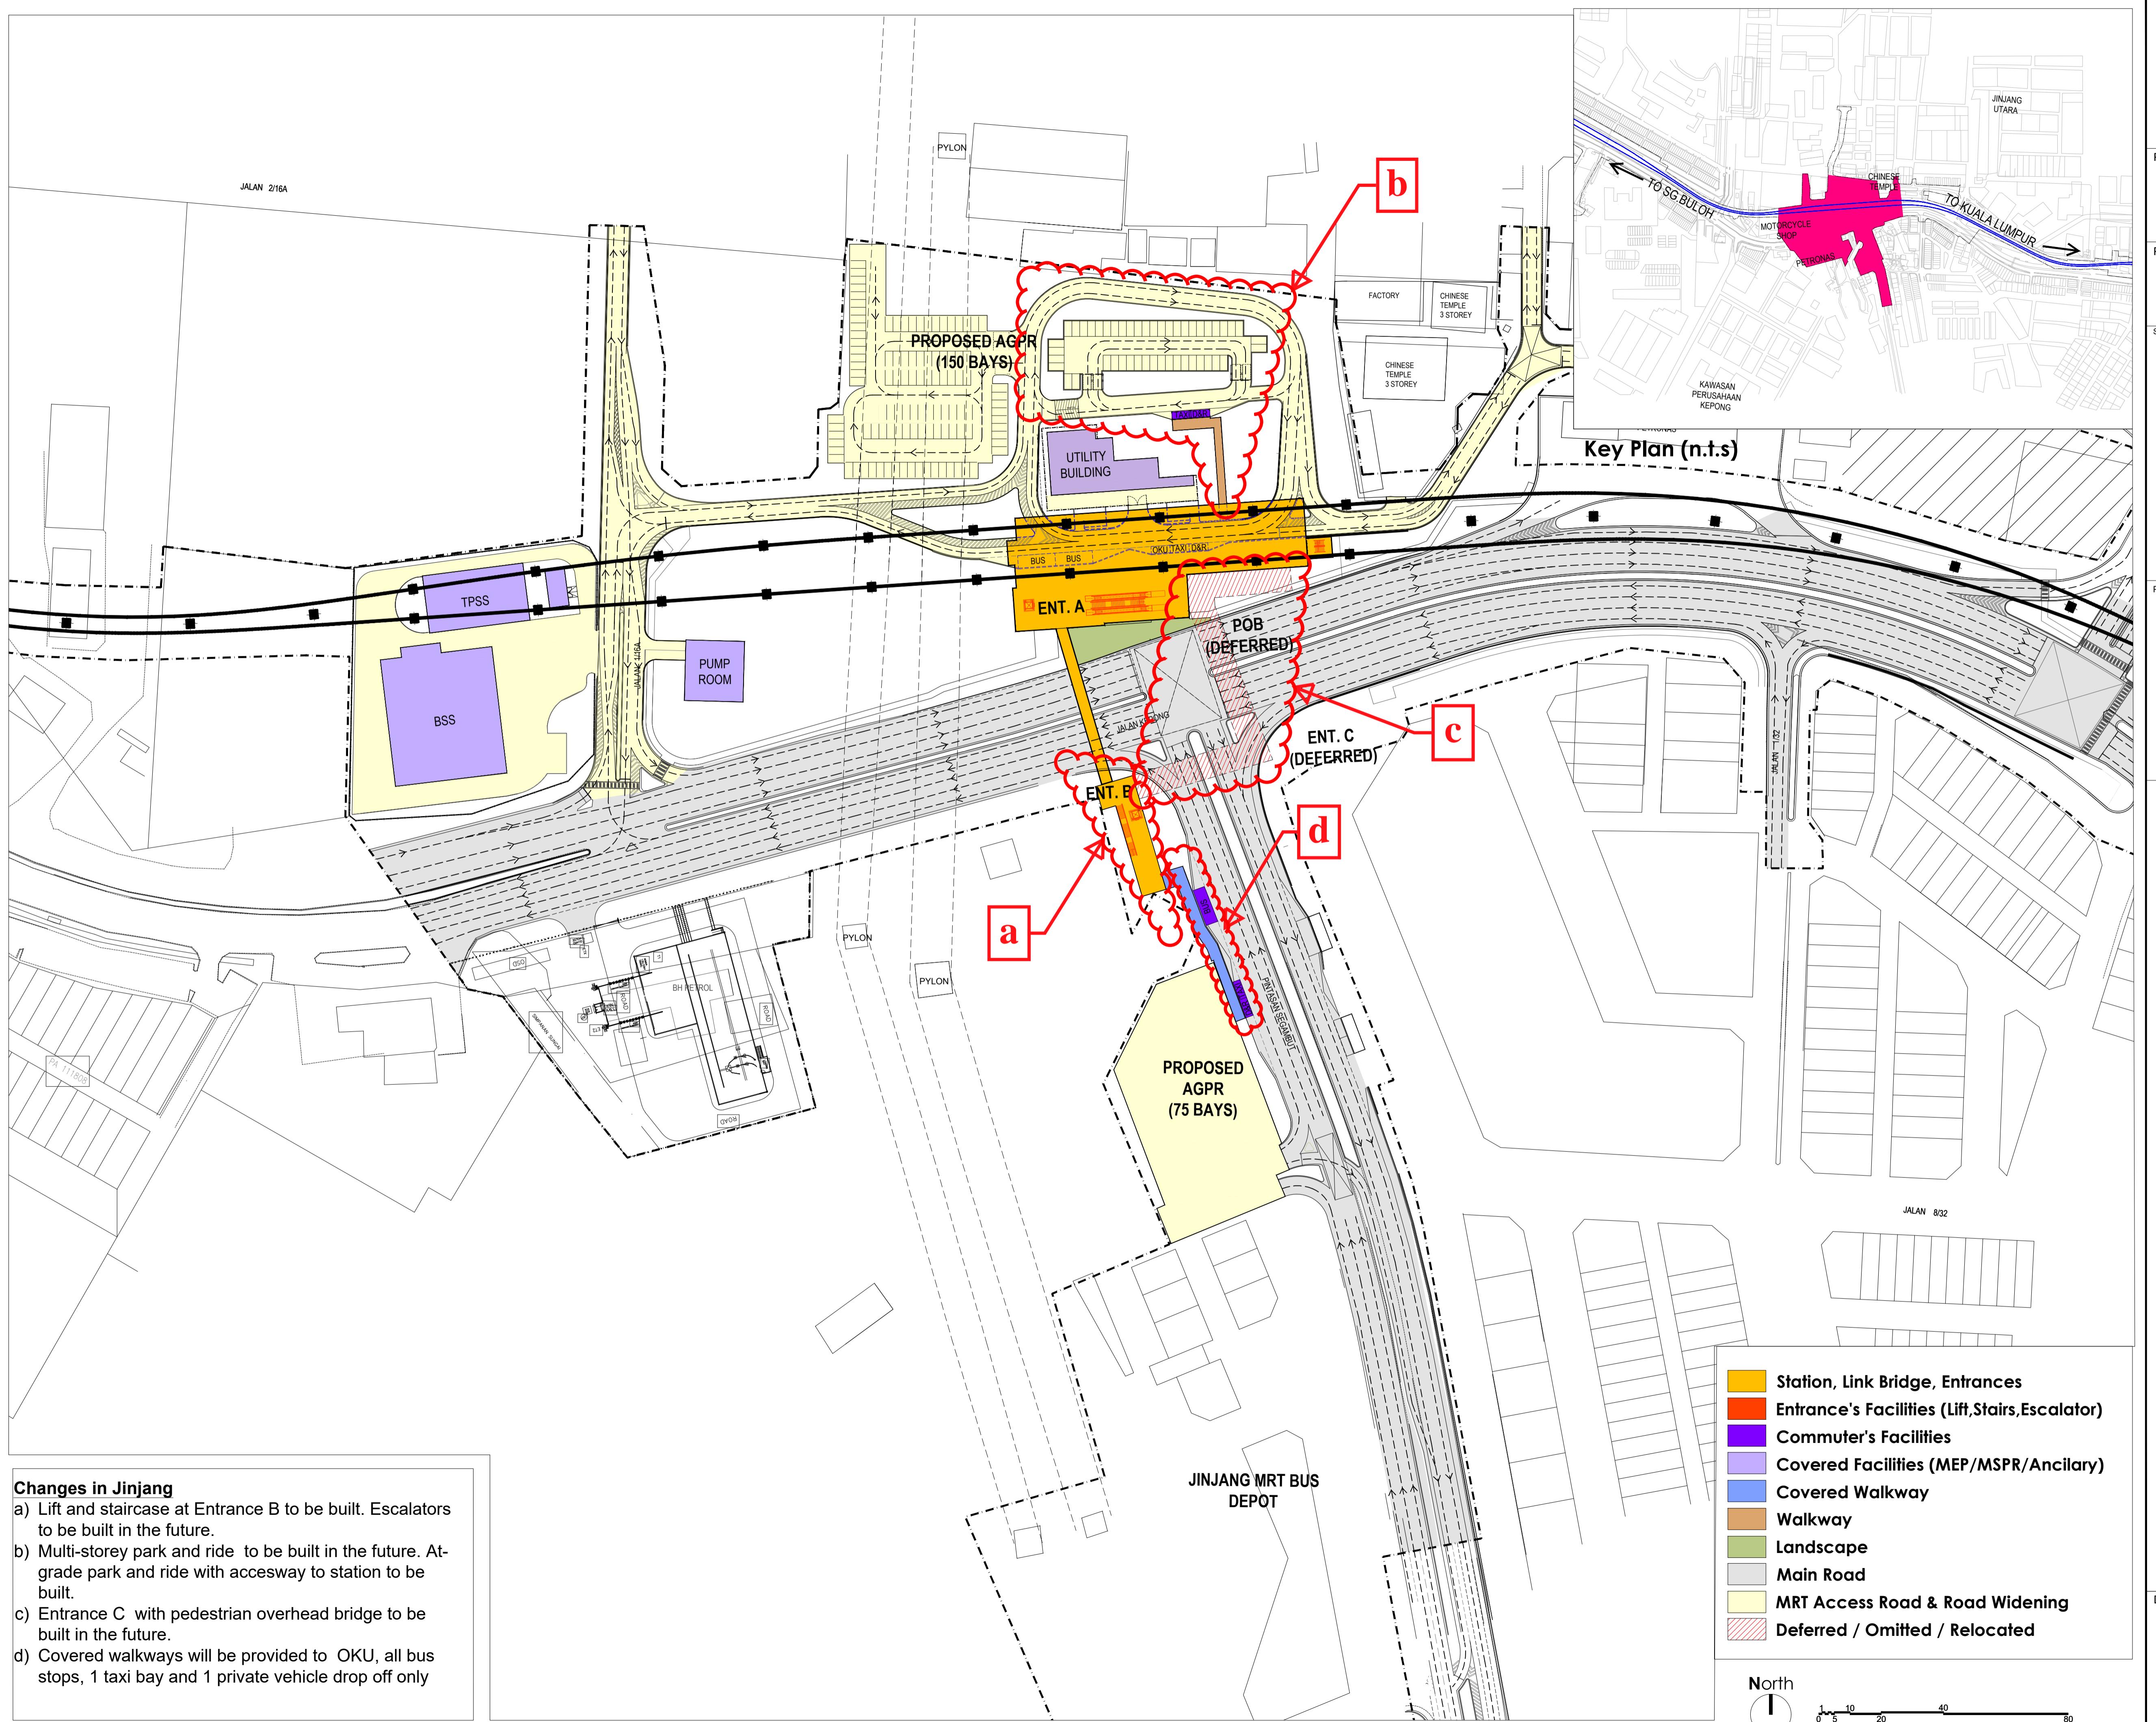

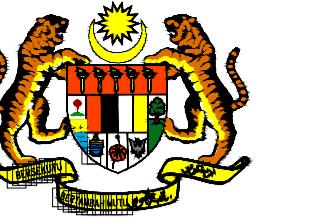

KERAJAAN MALAYSIA

PROJECT TITLE:  
PROJEK MASS RAPID TRANSIT LALUAN 2:  
PUTRAJAYA LINE  
(formerly known as PROJEK MRT LALUAN 2:  
SG BULOH - SERDANG - PUTRAJAYA (SSP))

PROJECT PACKAGE:

ELEVATED NORTH


SUPERVISING AGENCY :  
**AGENSI PENGANGKUTAN AWAM DARAT (APAD)**  
LAND PUBLIC TRANSPORT AGENCY (APAD)


**AGENSI PENGANGKUTAN AWAM DARAT (A.P.A.D.)**

ARAS G, M DAN 20, MENARA TUN ISMAIL MOHAMED ALI,  
NO. 25, JALAN RAJA LAUT, 50350 KUALA LUMPUR,  
MALAYSIA.  
TEL (ARAS G): 603-2603 6700 / TEL (ARAS 20): 603-2603 6600

PROJECT OWNER :  
**MRT CORP**  
Mass Rapid Transit Corporation Sdn Bhd  
(902884-V)  
5th FLOOR MENARA I&P 1,  
JALAN DUNGUN, DAMANSARA HEIGHTS,  
50490 KUALA LUMPUR.

Key Plan (n.t.s)

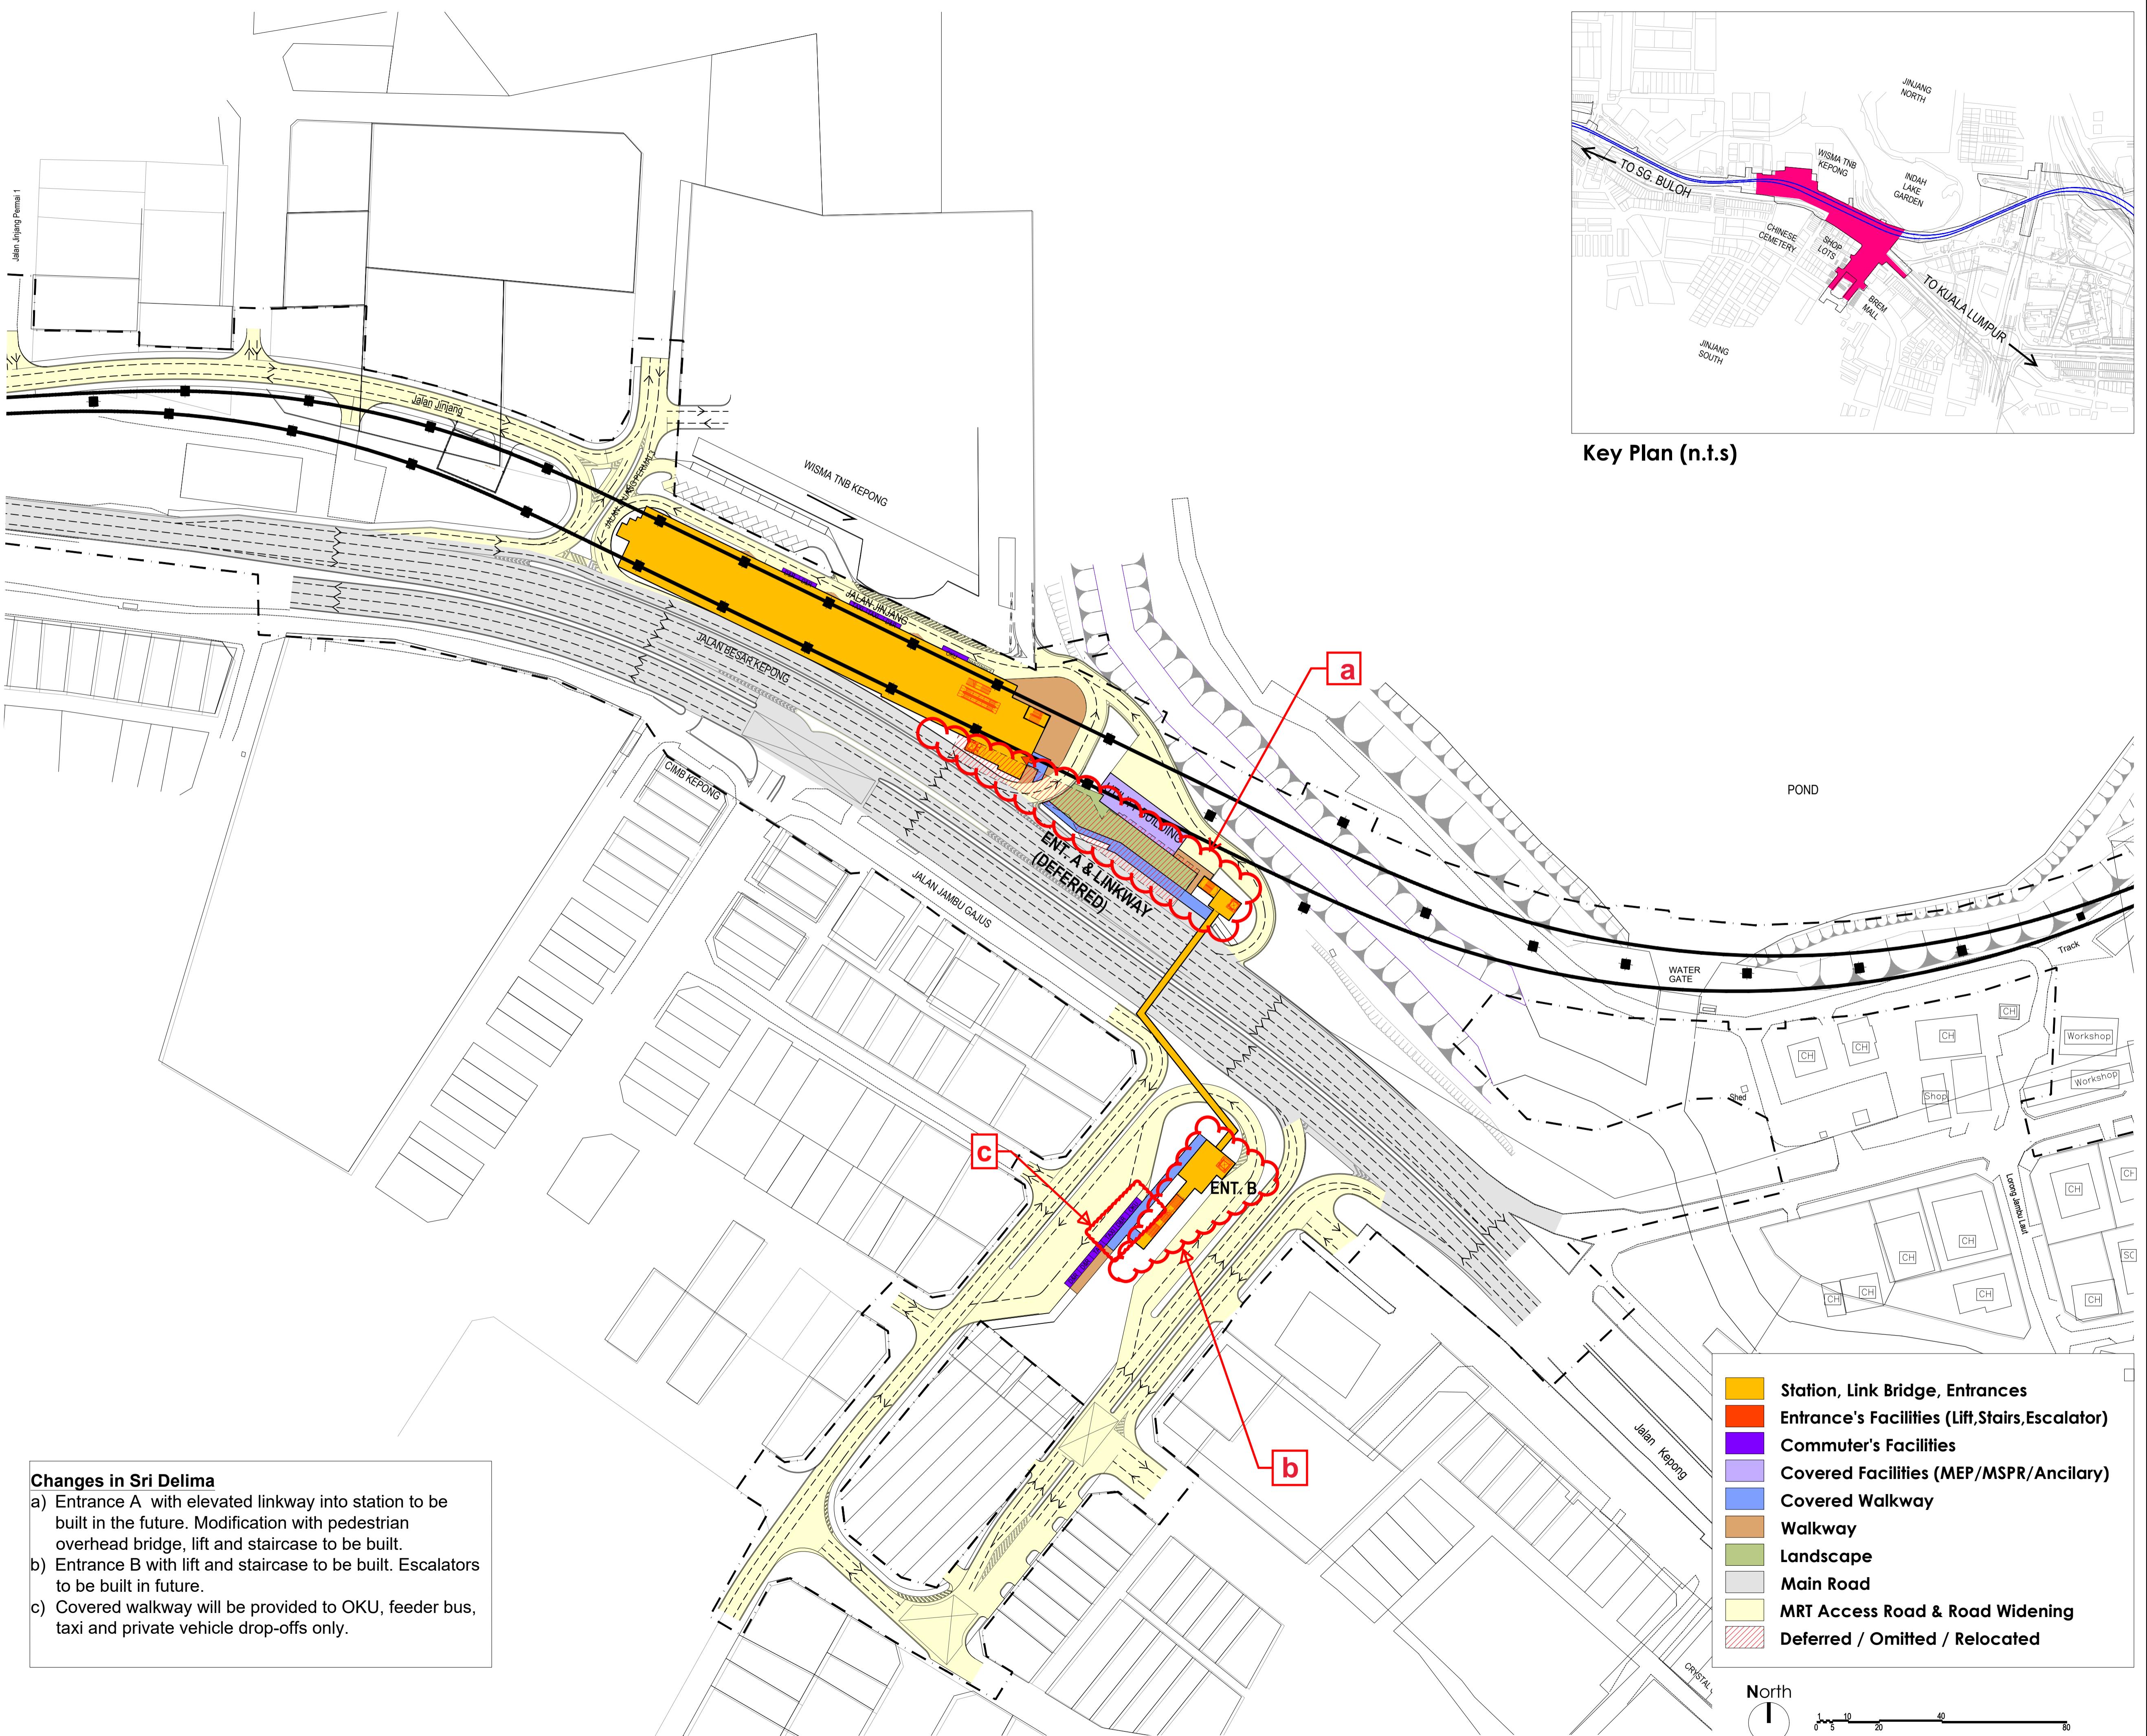

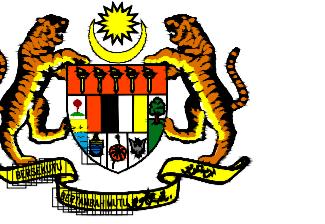

KERAJAAN MALAYSIA

PROJECT TITLE:  
PROJEK MASS RAPID TRANSIT LALUAN 2:  
PUTRAJAYA LINE  
(formerly known as PROJEK MRT LALUAN 2:  
SG BULOH - SERDANG - PUTRAJAYA (SSP))

PROJECT PACKAGE:


ELEVATED NORTH

SUPERVISING AGENCY :  
**AGENSI PENGANGKUTAN AWAM DARAT (APAD)**  
LAND PUBLIC TRANSPORT AGENCY (APAD)


AGENSI PENGANGKUTAN AWAM DARAT  
(A.P.A.D.)

ARAS G, M DAN 20, MENARA TUN ISMAIL MOHAMED ALI,  
NO. 25, JALAN RAJA LAUT, 50350 KUALA LUMPUR,  
MALAYSIA.  
TEL (ARAS G): 603-2603 6700 / TEL (ARAS 20): 603-2603 6600

PROJECT OWNER :  
**MRT CORP**  
Mass Rapid Transit Corporation Sdn Bhd  
(902884-V)  
5th FLOOR MENARA I&P 1,  
JALAN DUNGUN, DAMANSARA HEIGHTS,  
50490 KUALA LUMPUR.

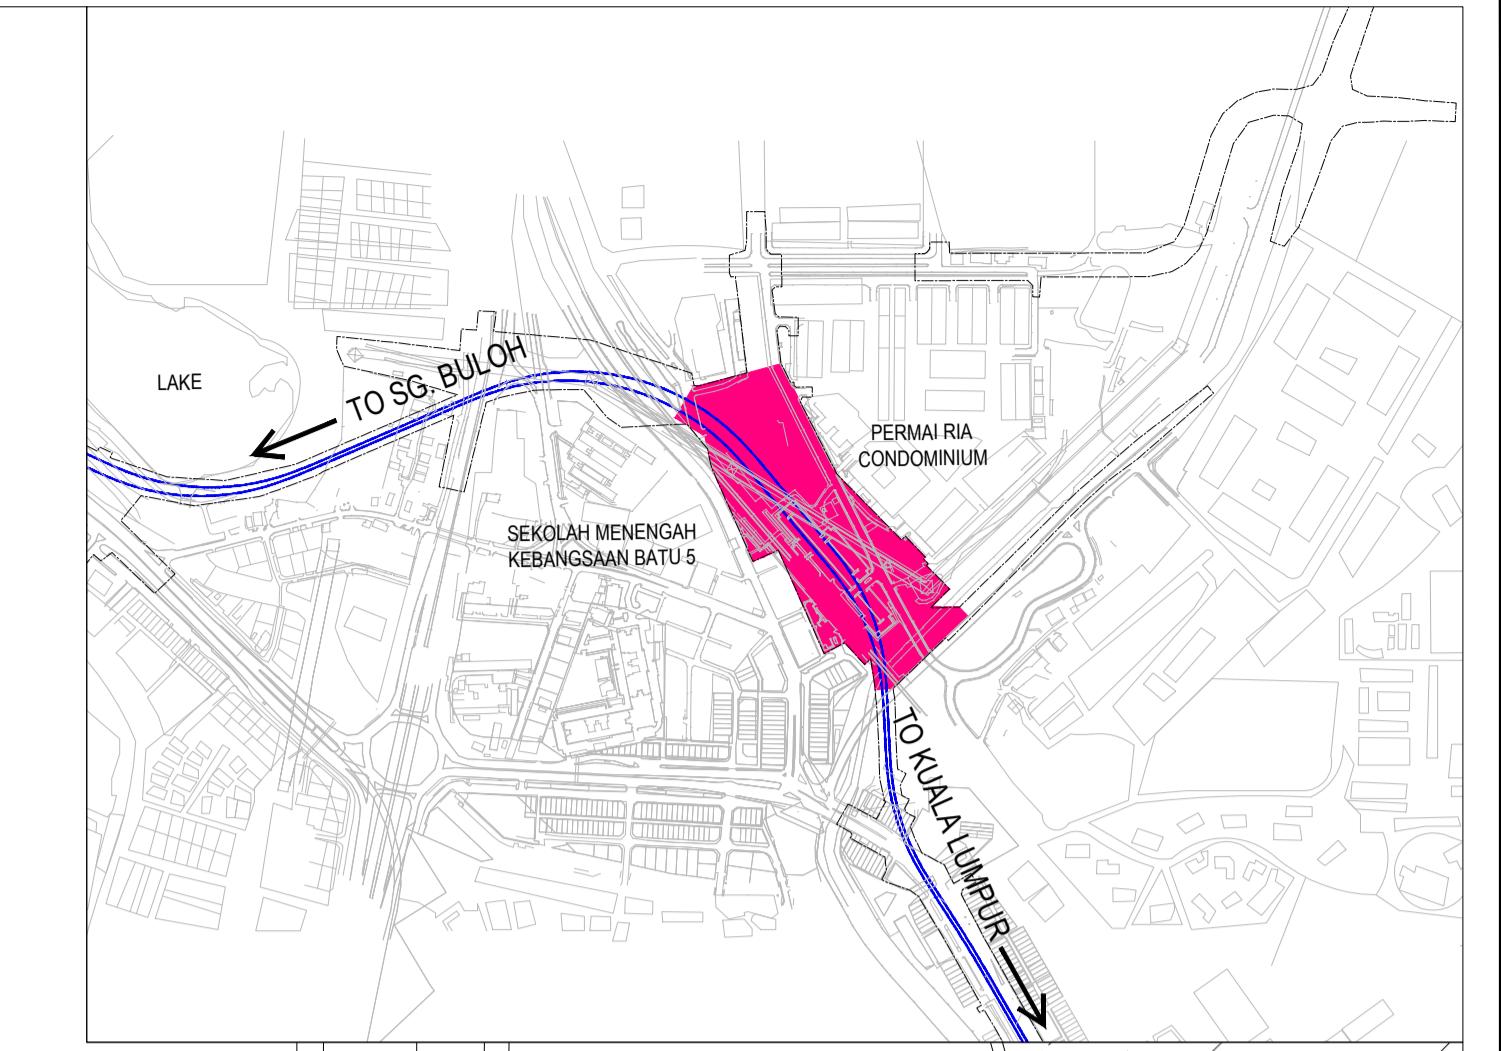


Key Plan (n.t.s)

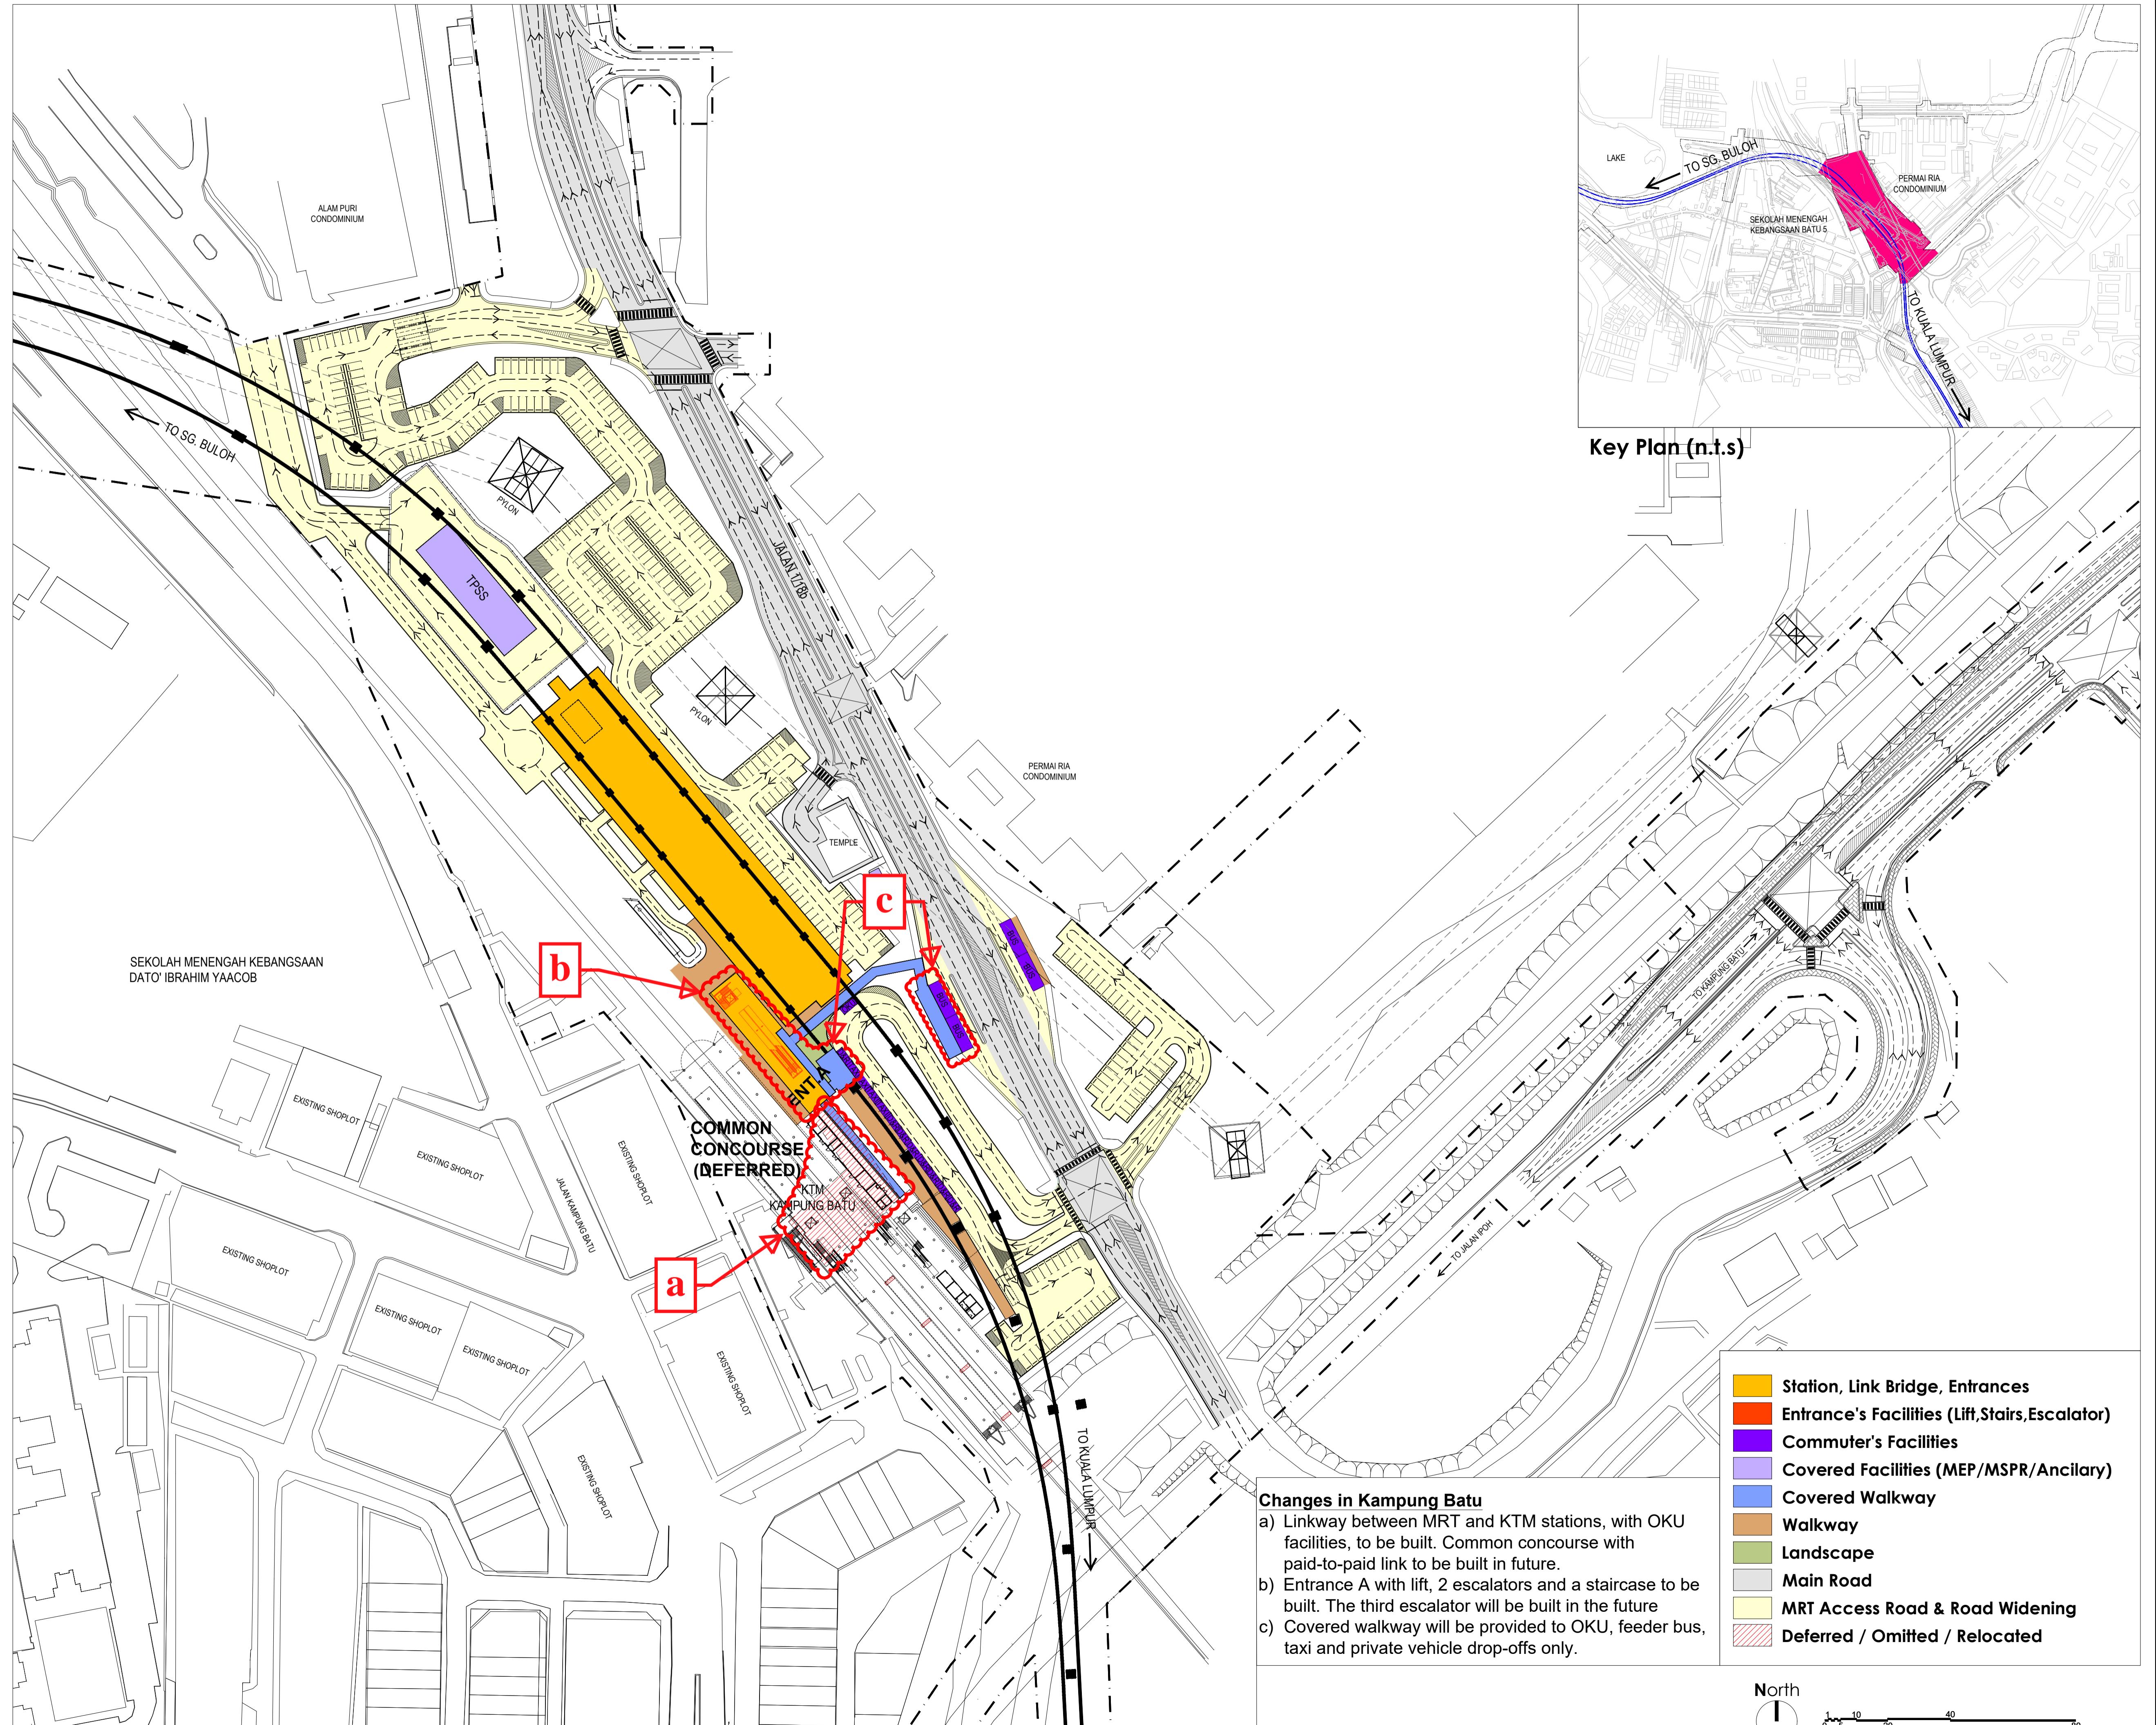

Drawing Title :

S13  
KAMPUNG BATU

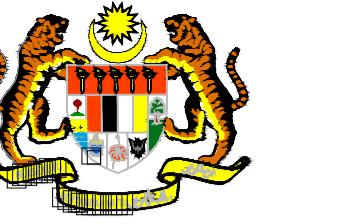

KERAJAAN MALAYSIA

PROJECT TITLE:  
PROJEK MASS RAPID TRANSIT LALUAN 2:  
PUTRAJAYA LINE  
(formerly known as PROJEK MRT LALUAN 2:  
SG BULOH - SERDANG - PUTRAJAYA (SSP))

PROJECT PACKAGE:


ELEVATED NORTH

SUPERVISING AGENCY :  
**AGENSI PENGANGKUTAN AWAM DARAT (APAD)**  
LAND PUBLIC TRANSPORT AGENCY (APAD)


**AGENSI PENGANGKUTAN AWAM DARAT (A.P.A.D.)**

ARAS G, M DAN 20, MENARA TUN ISMAIL MOHAMED ALI,  
NO. 25, JALAN RAJA LAUT, 50350 KUALA LUMPUR,  
MALAYSIA.  
TEL (ARAS G): 603-2603 6700 / TEL (ARAS 20): 603-2603 6600

PROJECT OWNER :  
**MRT CORP**  
Mass Rapid Transit Corporation Sdn Bhd  
(902884-V)  
5th FLOOR MENARA I&P 1,  
JALAN DUNGUN, DAMANSARA HEIGHTS,  
50490 KUALA LUMPUR.

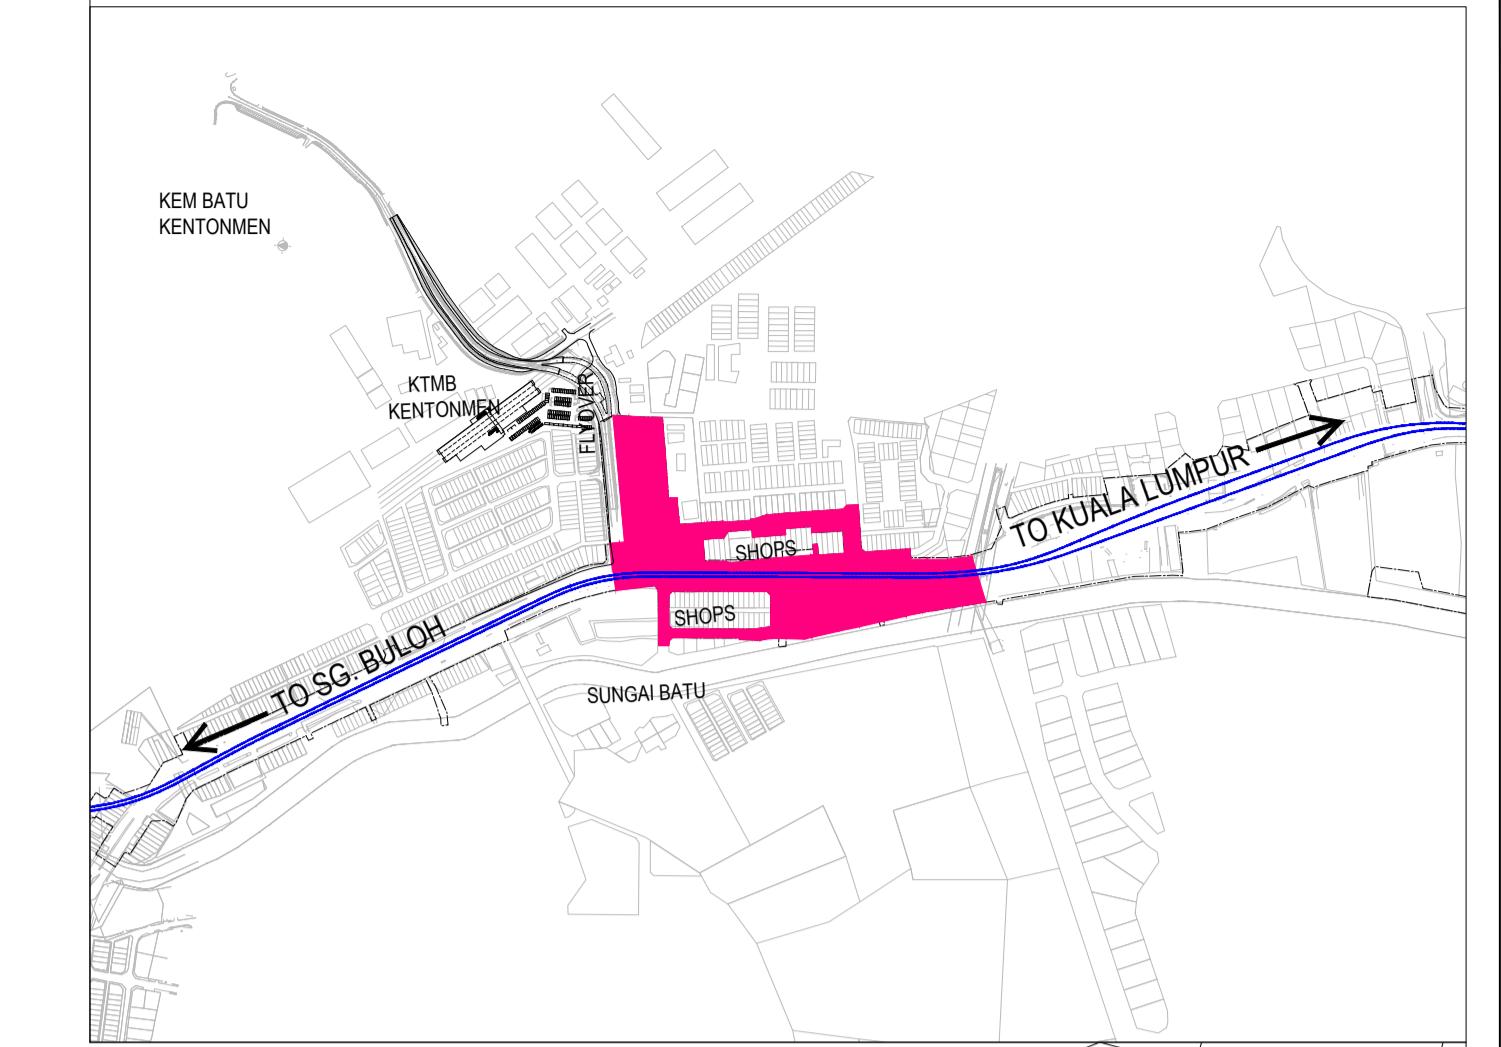


Key Plan (n.t.s)

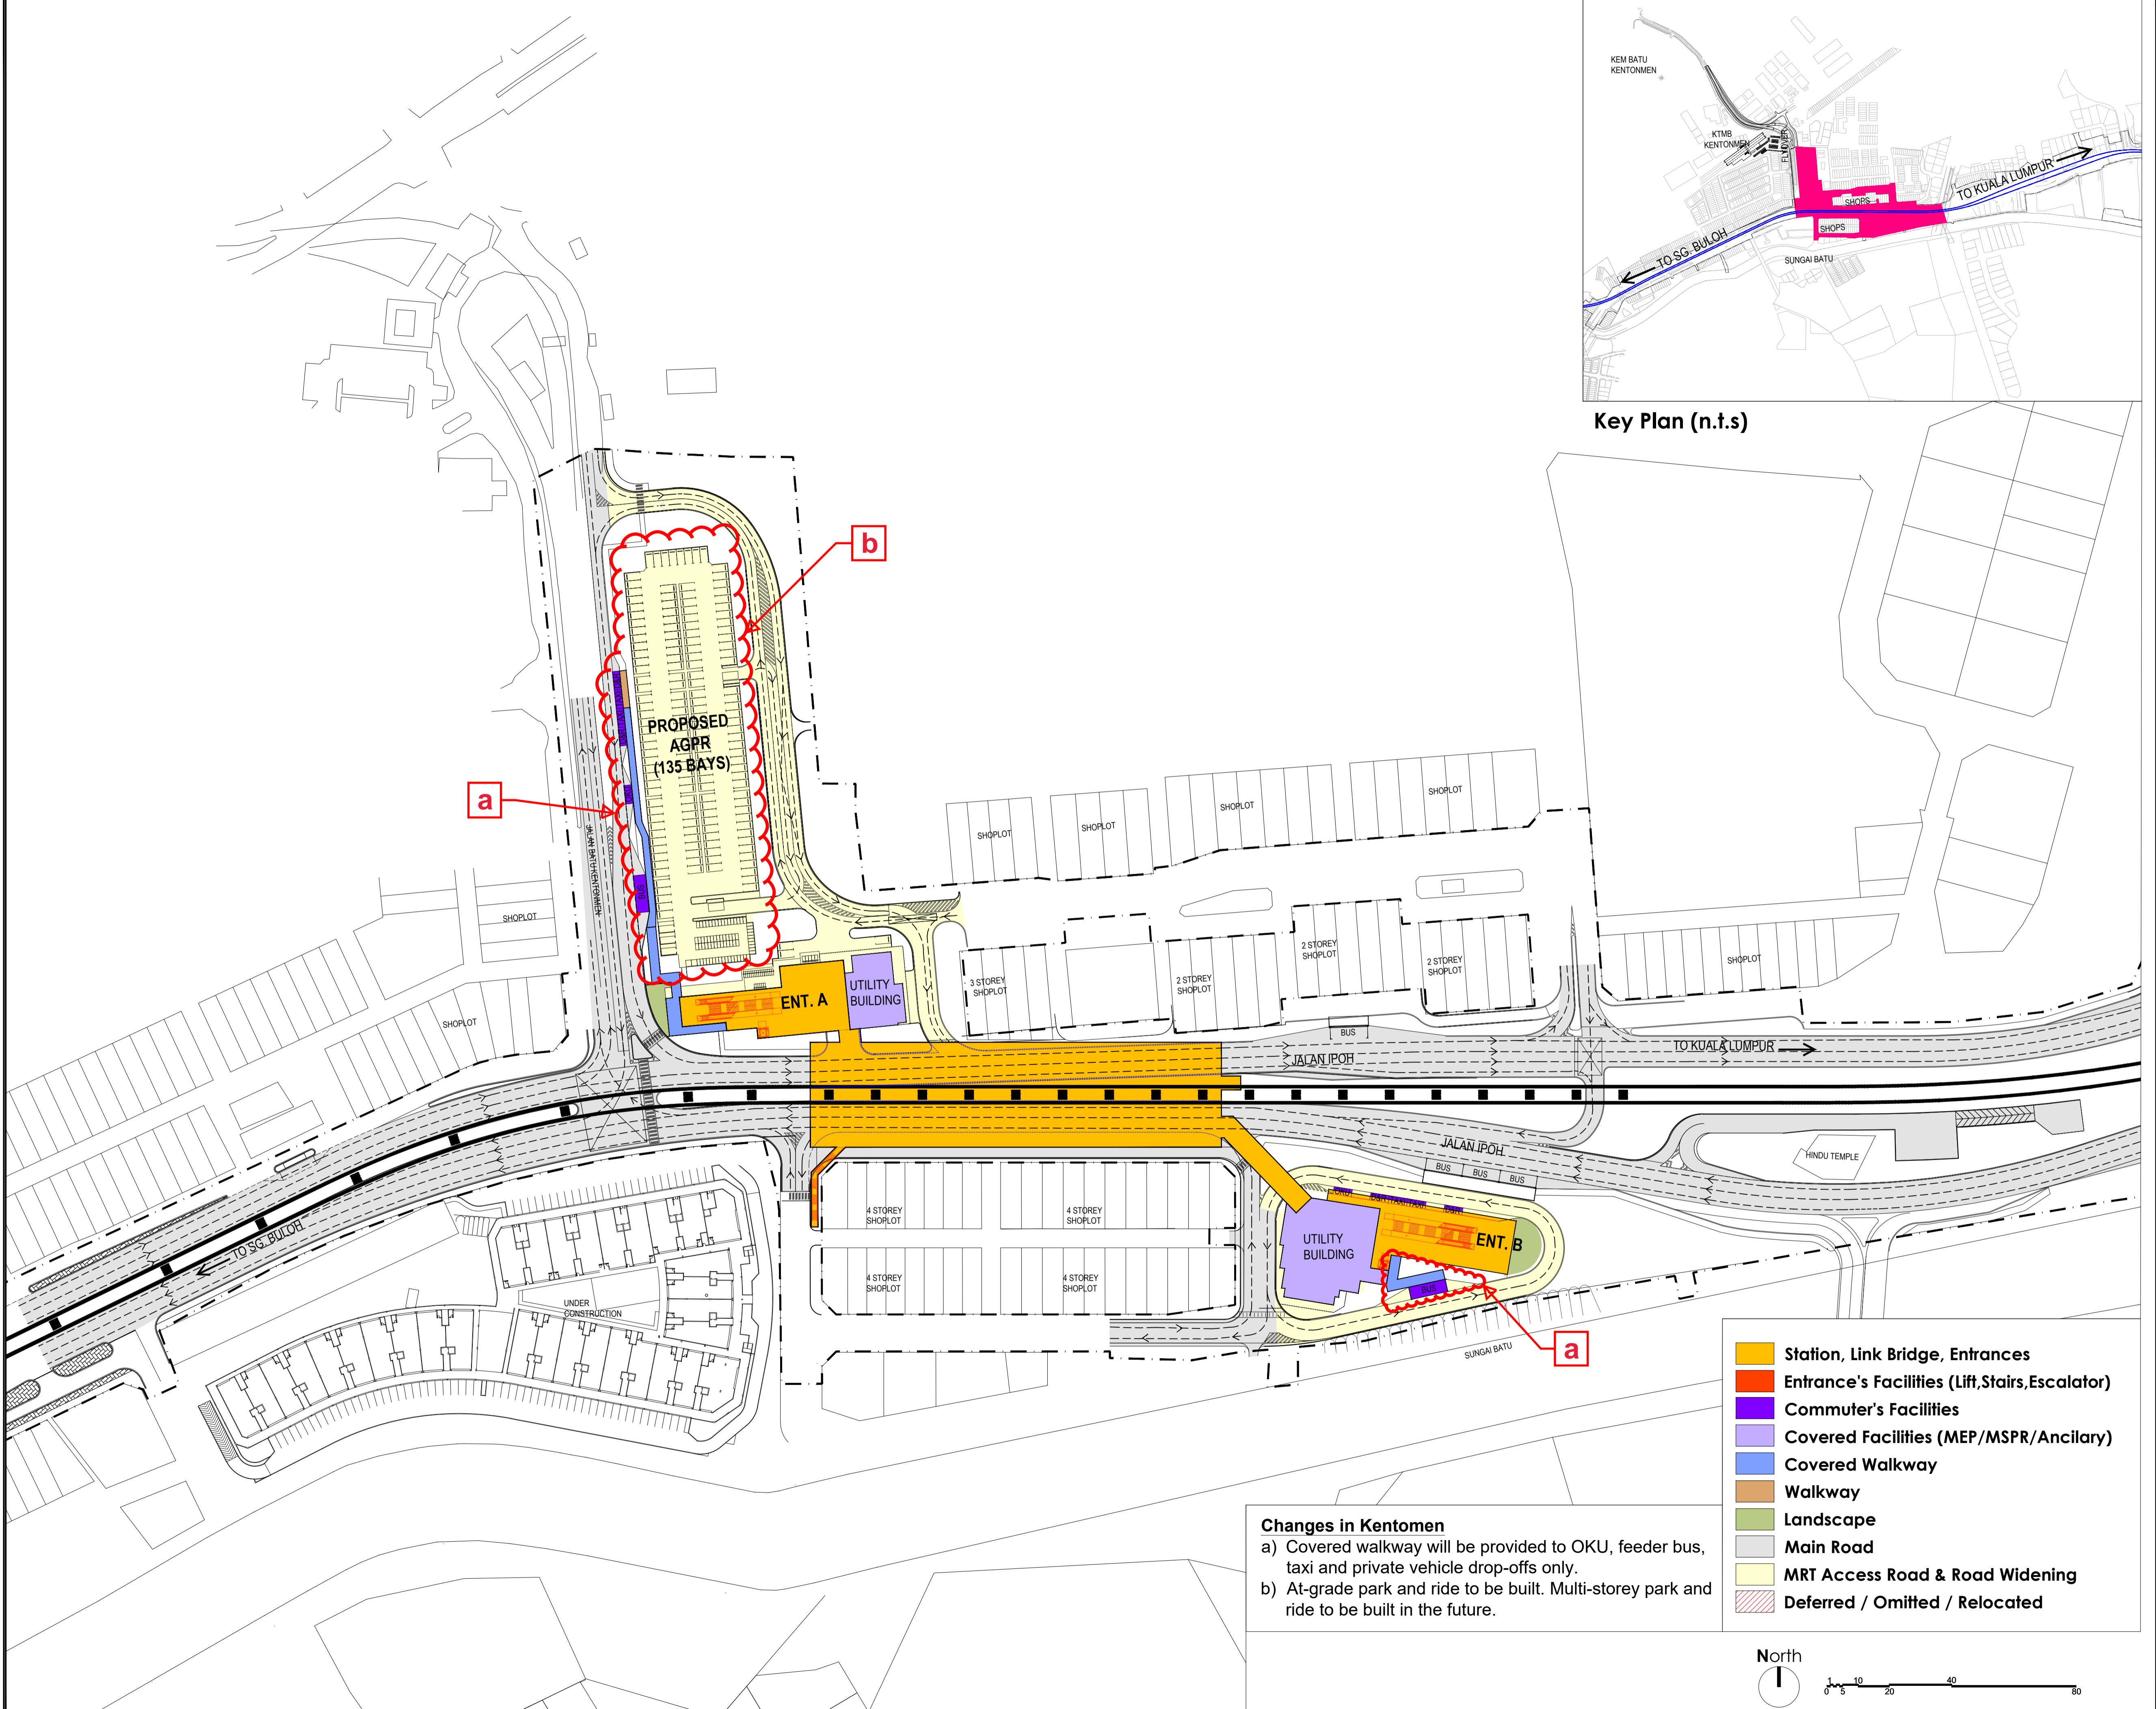

Drawing Title :

S14  
KENTONMEN

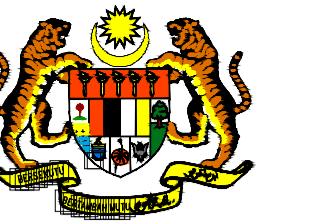

KERAJAAN MALAYSIA

PROJECT TITLE:  
PROJEK MASS RAPID TRANSIT LALUAN 2:  
PUTRAJAYA LINE  
(formerly known as PROJEK MRT LALUAN 2:  
SG BULOH - SERDANG - PUTRAJAYA (SSP))

PROJECT PACKAGE:  
ELEVATED NORTH


SUPERVISING AGENCY :  
**AGENSI PENGANGKUTAN AWAM DARAT (APAD)**  
LAND PUBLIC TRANSPORT AGENCY (APAD)

**AGENSI PENGANGKUTAN AWAM DARAT (A.P.A.D.)**

ARAS G, M DAN 20, MENARA TUN ISMAIL MOHAMED ALI,  
NO. 25, JALAN RAJA LAUT, 50350 KUALA LUMPUR,  
MALAYSIA.  
TEL (ARAS G): 603-2603 6700 / TEL (ARAS 20): 603-2603 6600

PROJECT OWNER :  
**MRT CORP**  
Mass Rapid Transit Corporation Sdn Bhd  
(902884-V)  
5th FLOOR MENARA I&P 1,  
JALAN DUNGUN, DAMANSARA HEIGHTS,  
50490 KUALA LUMPUR.


Key Plan (n.t.s)

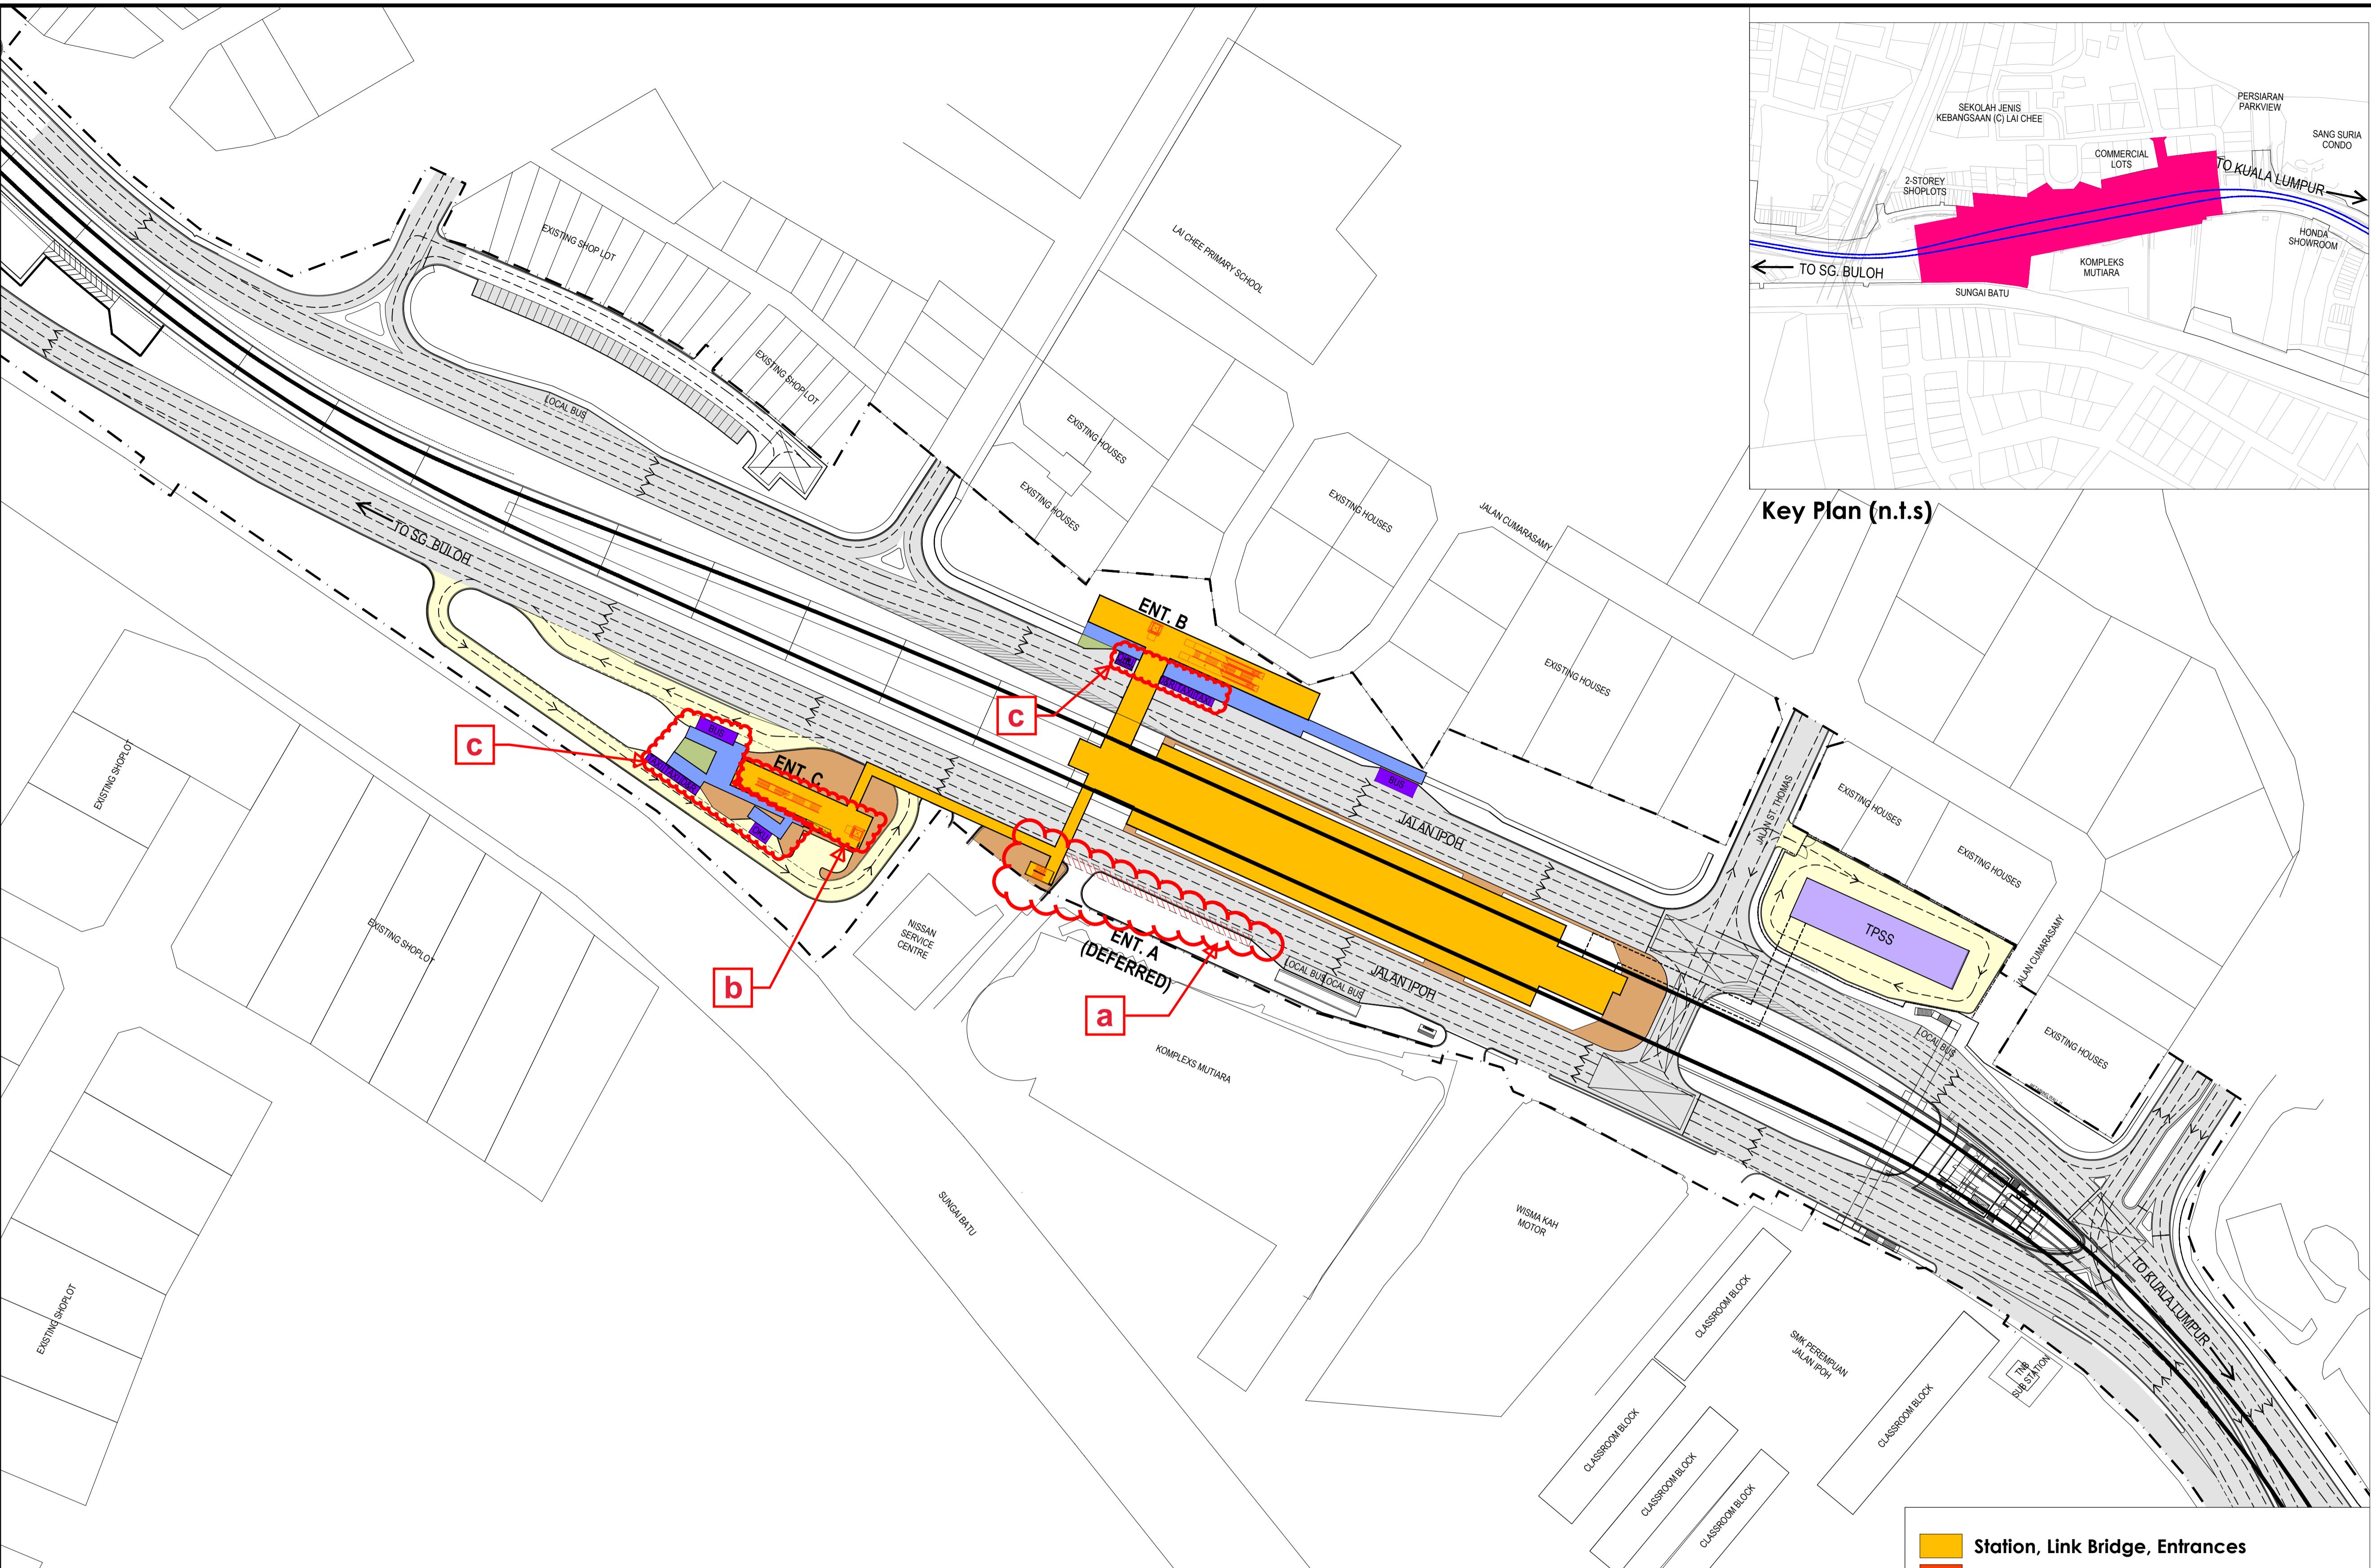

**Changes in Jalan Ipoh**

- a) Entrance A to be built in the future.
- b) Entrance C with lift and staircase to be built. Escalators to be built in future.
- c) Covered walkway will be provided to OKU, feeder bus, taxi and private vehicle drop-offs only.

North

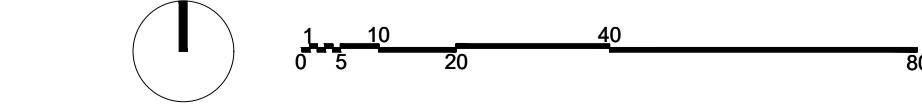

Drawing Title :

S15  
JALAN IPOH

**MRT PUTRAJAYA LINE**  
**(PREVIOUSLY KNOWN AS SG BULOH – SERDANG – PUTRAJAYA)**



**KERAJAAN MALAYSIA**

**STATION SITE CONTEXT PLAN  
(UNDERGROUND)**

SUPERVISING AGENCY:



PROJECT AND ASSET OWNER:



MASS RAPID TRANSIT  
CORPORATION SDN BHD



**KERAJAAN MALAYSIA**


PROJECT TITLE:  
PROJECT MASS RAPID TRANSIT LALUAN 2:  
PUTRAJAYA LINE  
(formerly known as PROJEK MRT LALUAN 2:  
SG BULOH - SERDANG - PUTRAJAYA (SSP))

PROJECT PACKAGE:  
**UNDERGROUND**

SUPERVISING AGENCY :  
**AGENSI PENGANGKUTAN AWAM DARAT (APAD)**  
LAND PUBLIC TRANSPORT AGENCY (APAD)  
**AGENSI PENGANGKUTAN AWAM DARAT (AP.A.D.)**

ARAS G, M DAN 20, MENARA TUN ISMAIL MOHAMED ALI,  
NO. 25, JALAN RAJA LAUT,  
50470 KUALA LUMPUR.  
Tel (ARAS G): 603-2603 6700 / Tel (ARAS 20): 603-2603 6600  
Fax : 603-26036710


PROJECT OWNER :  
**MRT CORP**  
**Mass Rapid Transit Corporation Sdn Bhd**  
(902884-V)  
5th FLOOR MENARA I&P 1,  
JALAN DUNGUN, DAMANSARA HEIGHTS,  
50490 KUALA LUMPUR.

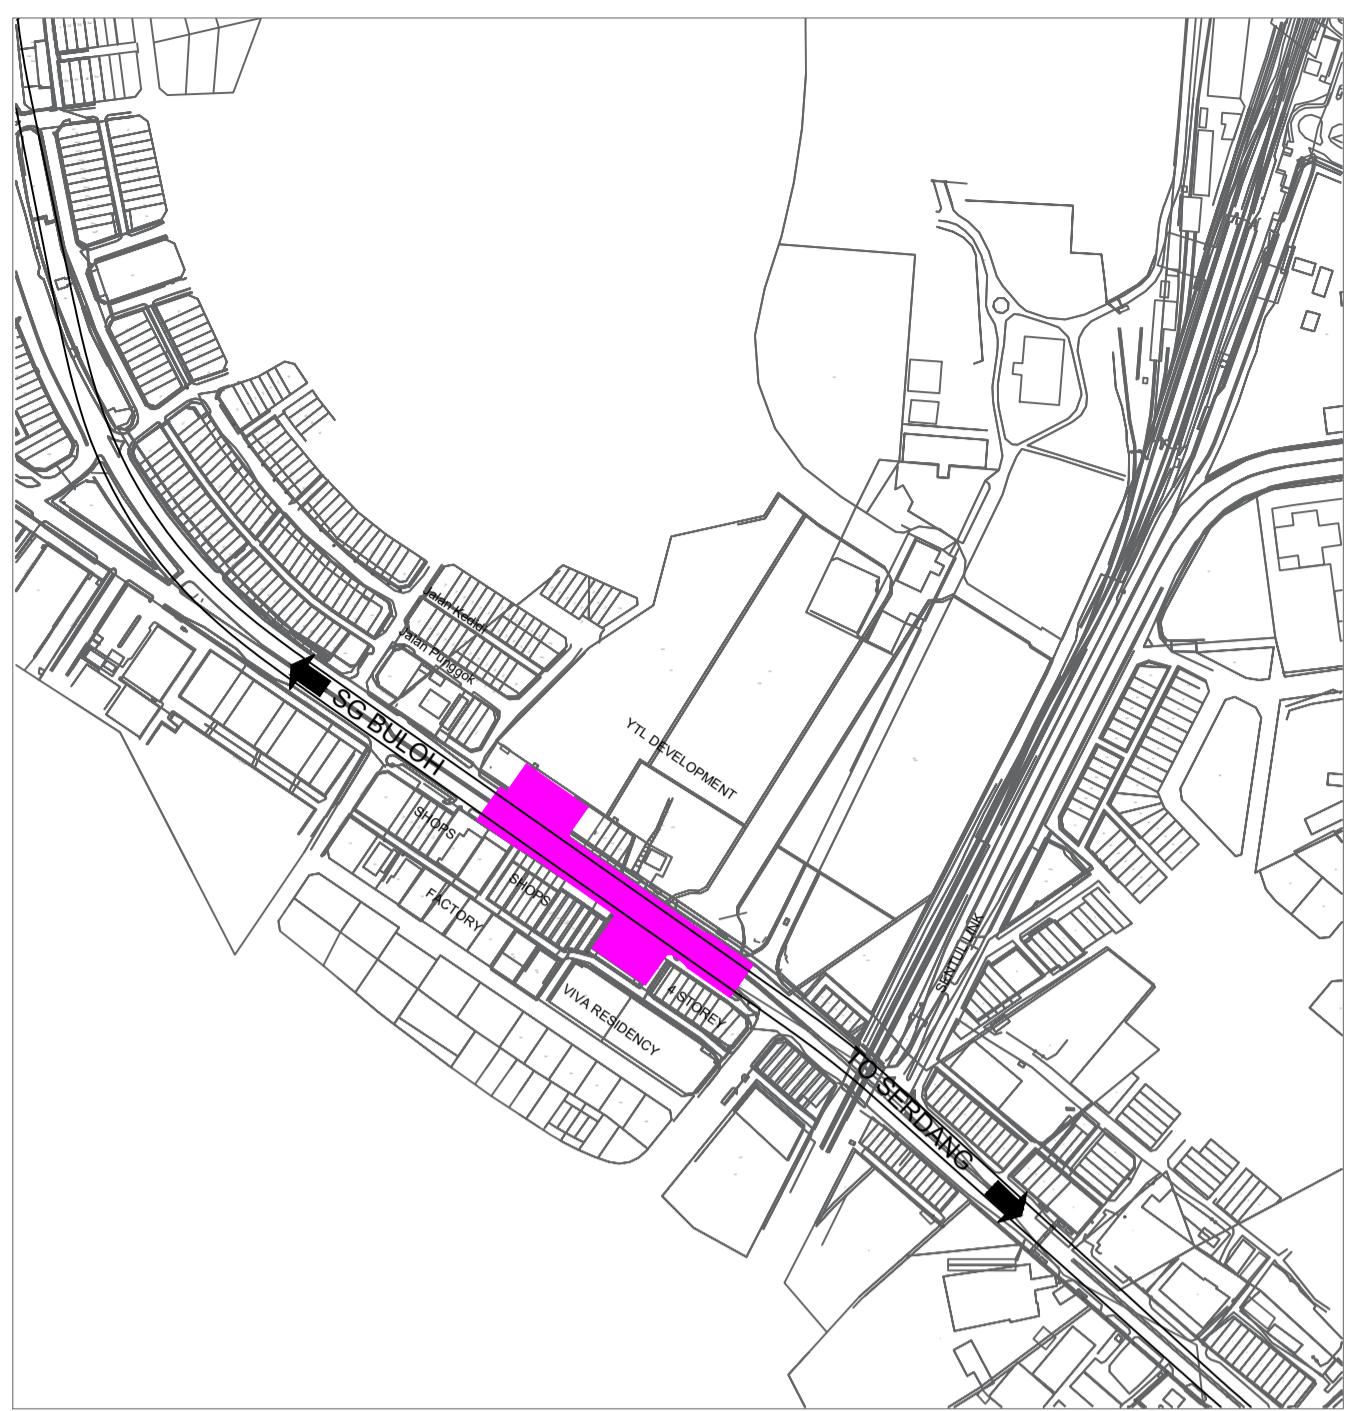


<b>Station, Link Bridge, Entrances</b>
<b>Entrance's Facilities (Lift, Stairs, Escalator)</b>
<b>Commuter's Facilities</b>
<b>Covered Facilities (MEP/MSPR/Ancillary)</b>
<b>Covered Walkway</b>
<b>Walkway</b>
<b>Landscape</b>
<b>Main Road</b>
<b>MRT Access Road &amp; Road Widening</b>
<b>Deferred / Omitted / Relocated</b>

**Changes in Sentul Barat (Sentul West)**

- Station name to change to Sentul Barat.
- Entrance A to be omitted.
- Entrance B bus stops to be omitted and to be replaced with private car drop off.

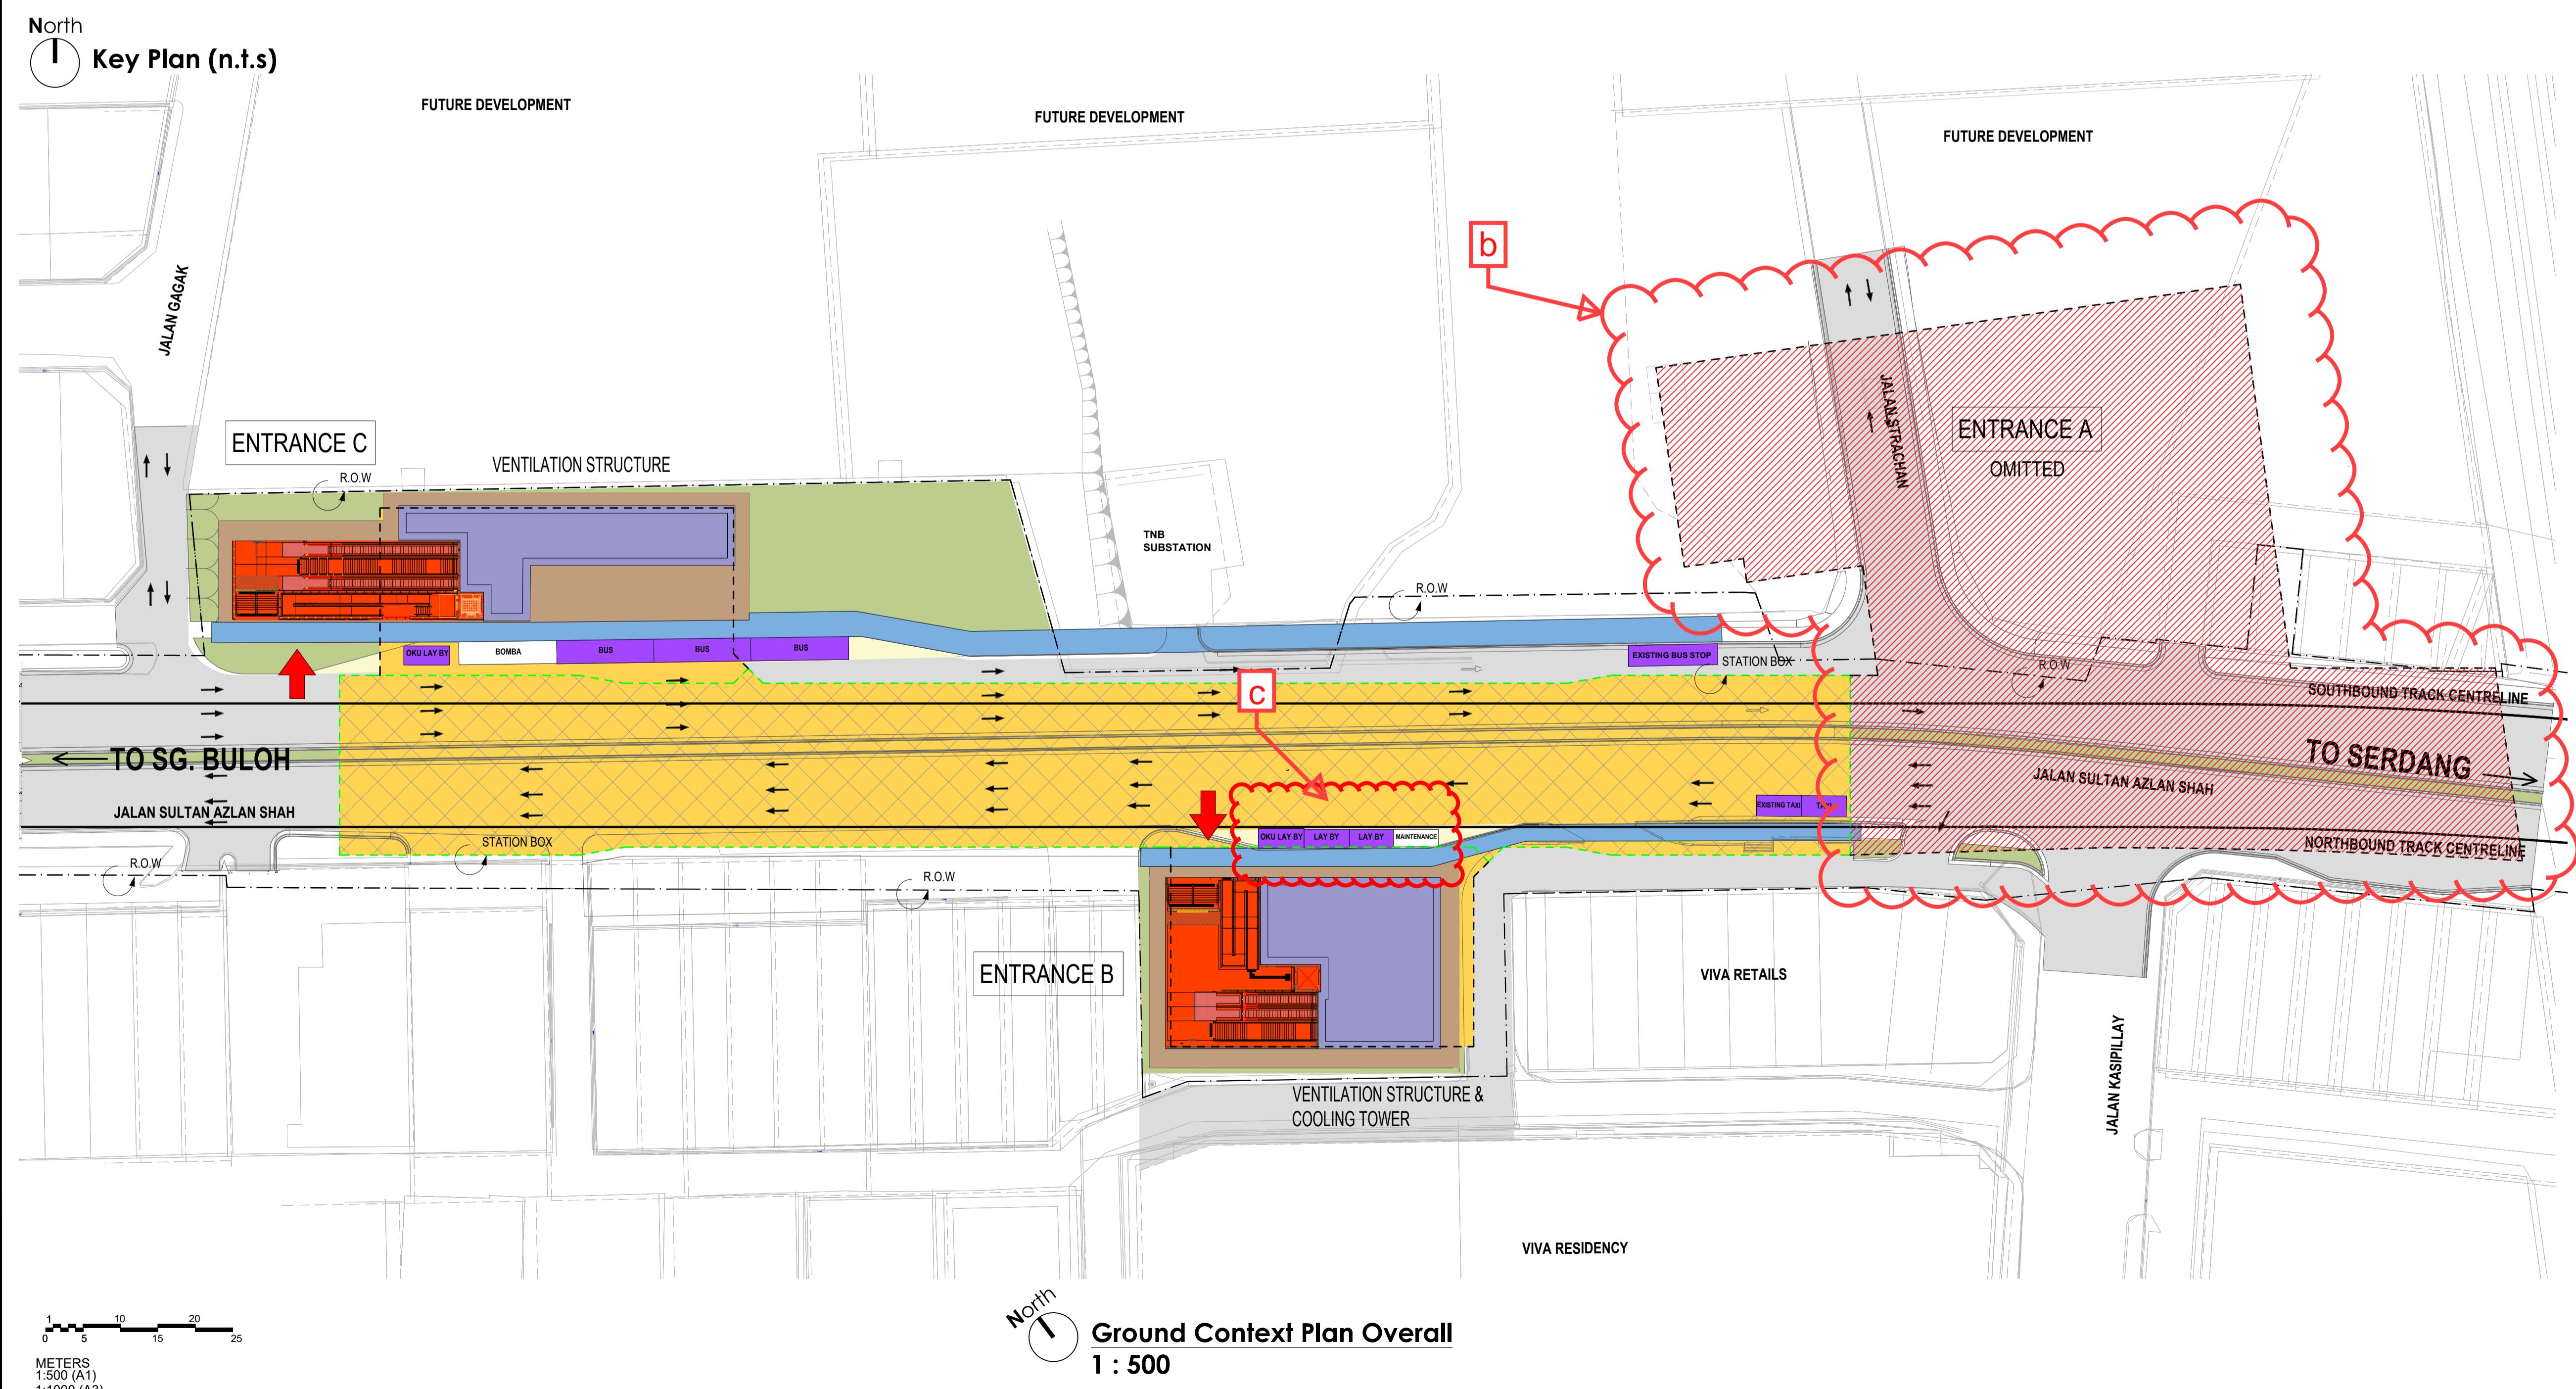

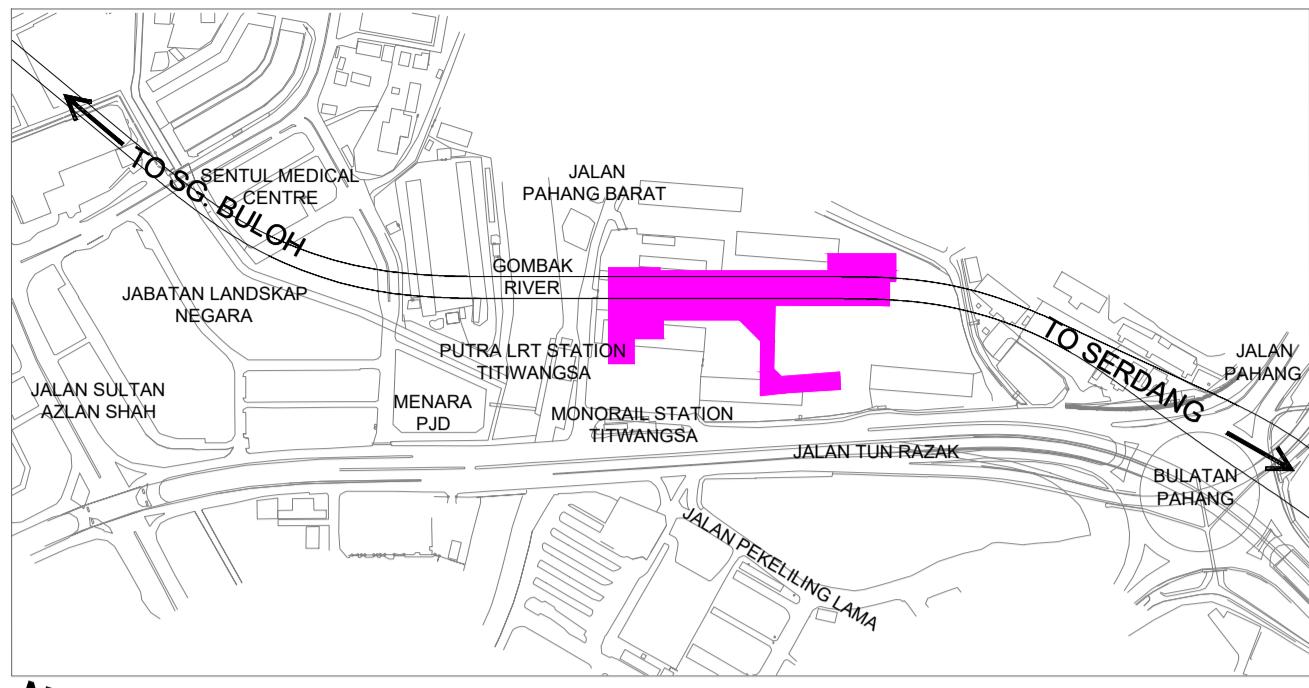


## Changes in Titiwangsa

- a) Entrance C with underground linkway to be built in the future.
  - b) Two additional lifts for the LRT pedestrian overhead bridge to be built.
  - c) Bus interchange to be built in the future by others.

# *North* Key Plan (n.t.s)

# Key Plan (n.t.s)

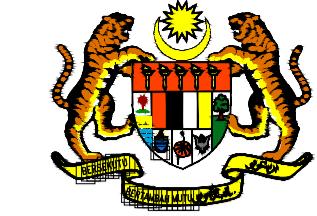

KERAJAAN MALAYSIA

PROJECT TITLE:

**PROJECT MASS RAPID TRANSIT LALUAN 2:  
PUTRAJAYA LINE**

(formerly known as PROJEK MRT LALUAN 2:  
SG BULOH - SERDANG - PUTRAJAYA (SSP))

# PROJECT PACKAGE: UNDERGROUND

**SUPERVISING AGENCY :**

**AGENSI PENGANGKUTAN AWAM DARAT (APAD)**

---

**LAND PUBLIC TRANSPORT AGENCY (APAD)**

**AGENSI PENGANGKUTAN AWAM DARAT**

ARAS G, M DAN 20, MENARA TUN ISMAIL MOHAMED ALI,  
NO. 25, JALAN RAJA LAUT,  
50470 KUALA LUMPUR.  
Tel (ARAS G): 603-2603 6700 / Tel (ARAS 20): 603-2603 6600  
Fax : 603-26036710

PROJECT OWNER :

**MRT CORP**

**Mass Rapid Transit Corporation Sdn Bhd**  
(902884-V)

5th FLOOR MENARA I&P 1,  
JALAN DUNGUN, DAMANSARA HEIGHTS,  
50490 KUALA LUMPUR.

Drawing Title

S17  
TITIWANGSA



KERAJAAN MALAYSIA

PROJECT TITLE:

PROJECT MASS RAPID TRANSIT LALUAN 2:  
PUTRAJAYA LINE  
(formerly known as PROJEK MRT LALUAN 2:  
SG BULOH - SERDANG - PUTRAJAYA (SSP))

PROJECT PACKAGE:

UNDERGROUND

SUPERVISING AGENCY :

AGENSI PENGANGKUTAN AWAM DARAT (APAD)  
LAND PUBLIC TRANSPORT AGENCY (APAD)

AGENSI PENGANGKUTAN AWAM DARAT (APAD)

ARAS G, M DAN 20, MENARA TUN ISMAIL MOHAMED ALI,  
NO. 25, JALAN RAJA LAUT,  
50470 KUALA LUMPUR.  
Tel (ARAS G): 603-2603 6700 / Tel (ARAS 20): 603-2603 6600  
Fax : 603-26036710

PROJECT OWNER :




Mass Rapid Transit Corporation Sdn Bhd  
(902884-V)

5th FLOOR MENARA I&P 1,  
JALAN DUNGUN, DAMANSARA HEIGHTS,  
50490 KUALA LUMPUR.


### Changes in Hospital KL

- a) Entrance C to be built in the future.
- b) Entrance A location to be changed based on requirement of Hospital Kuala Lumpur.

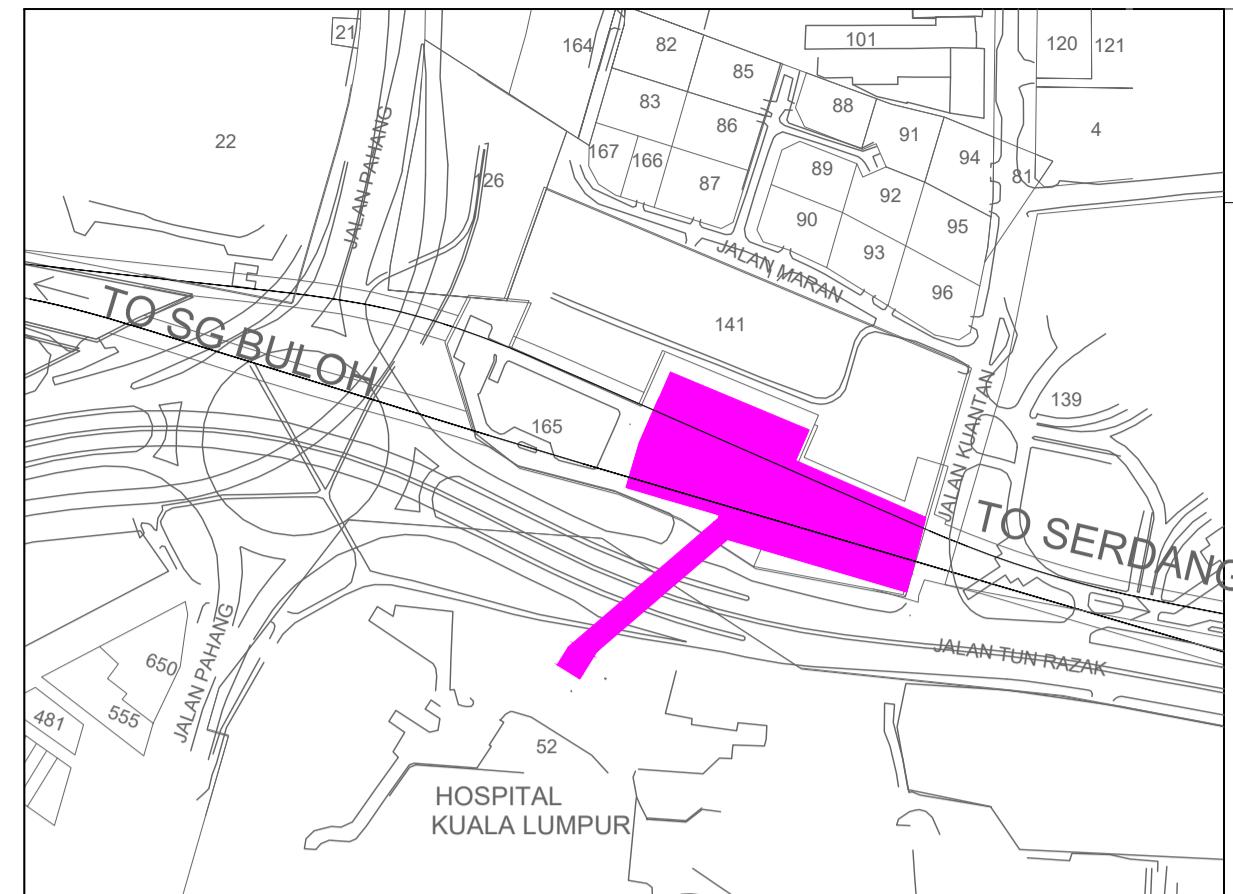

North

Key Plan (n.t.s)

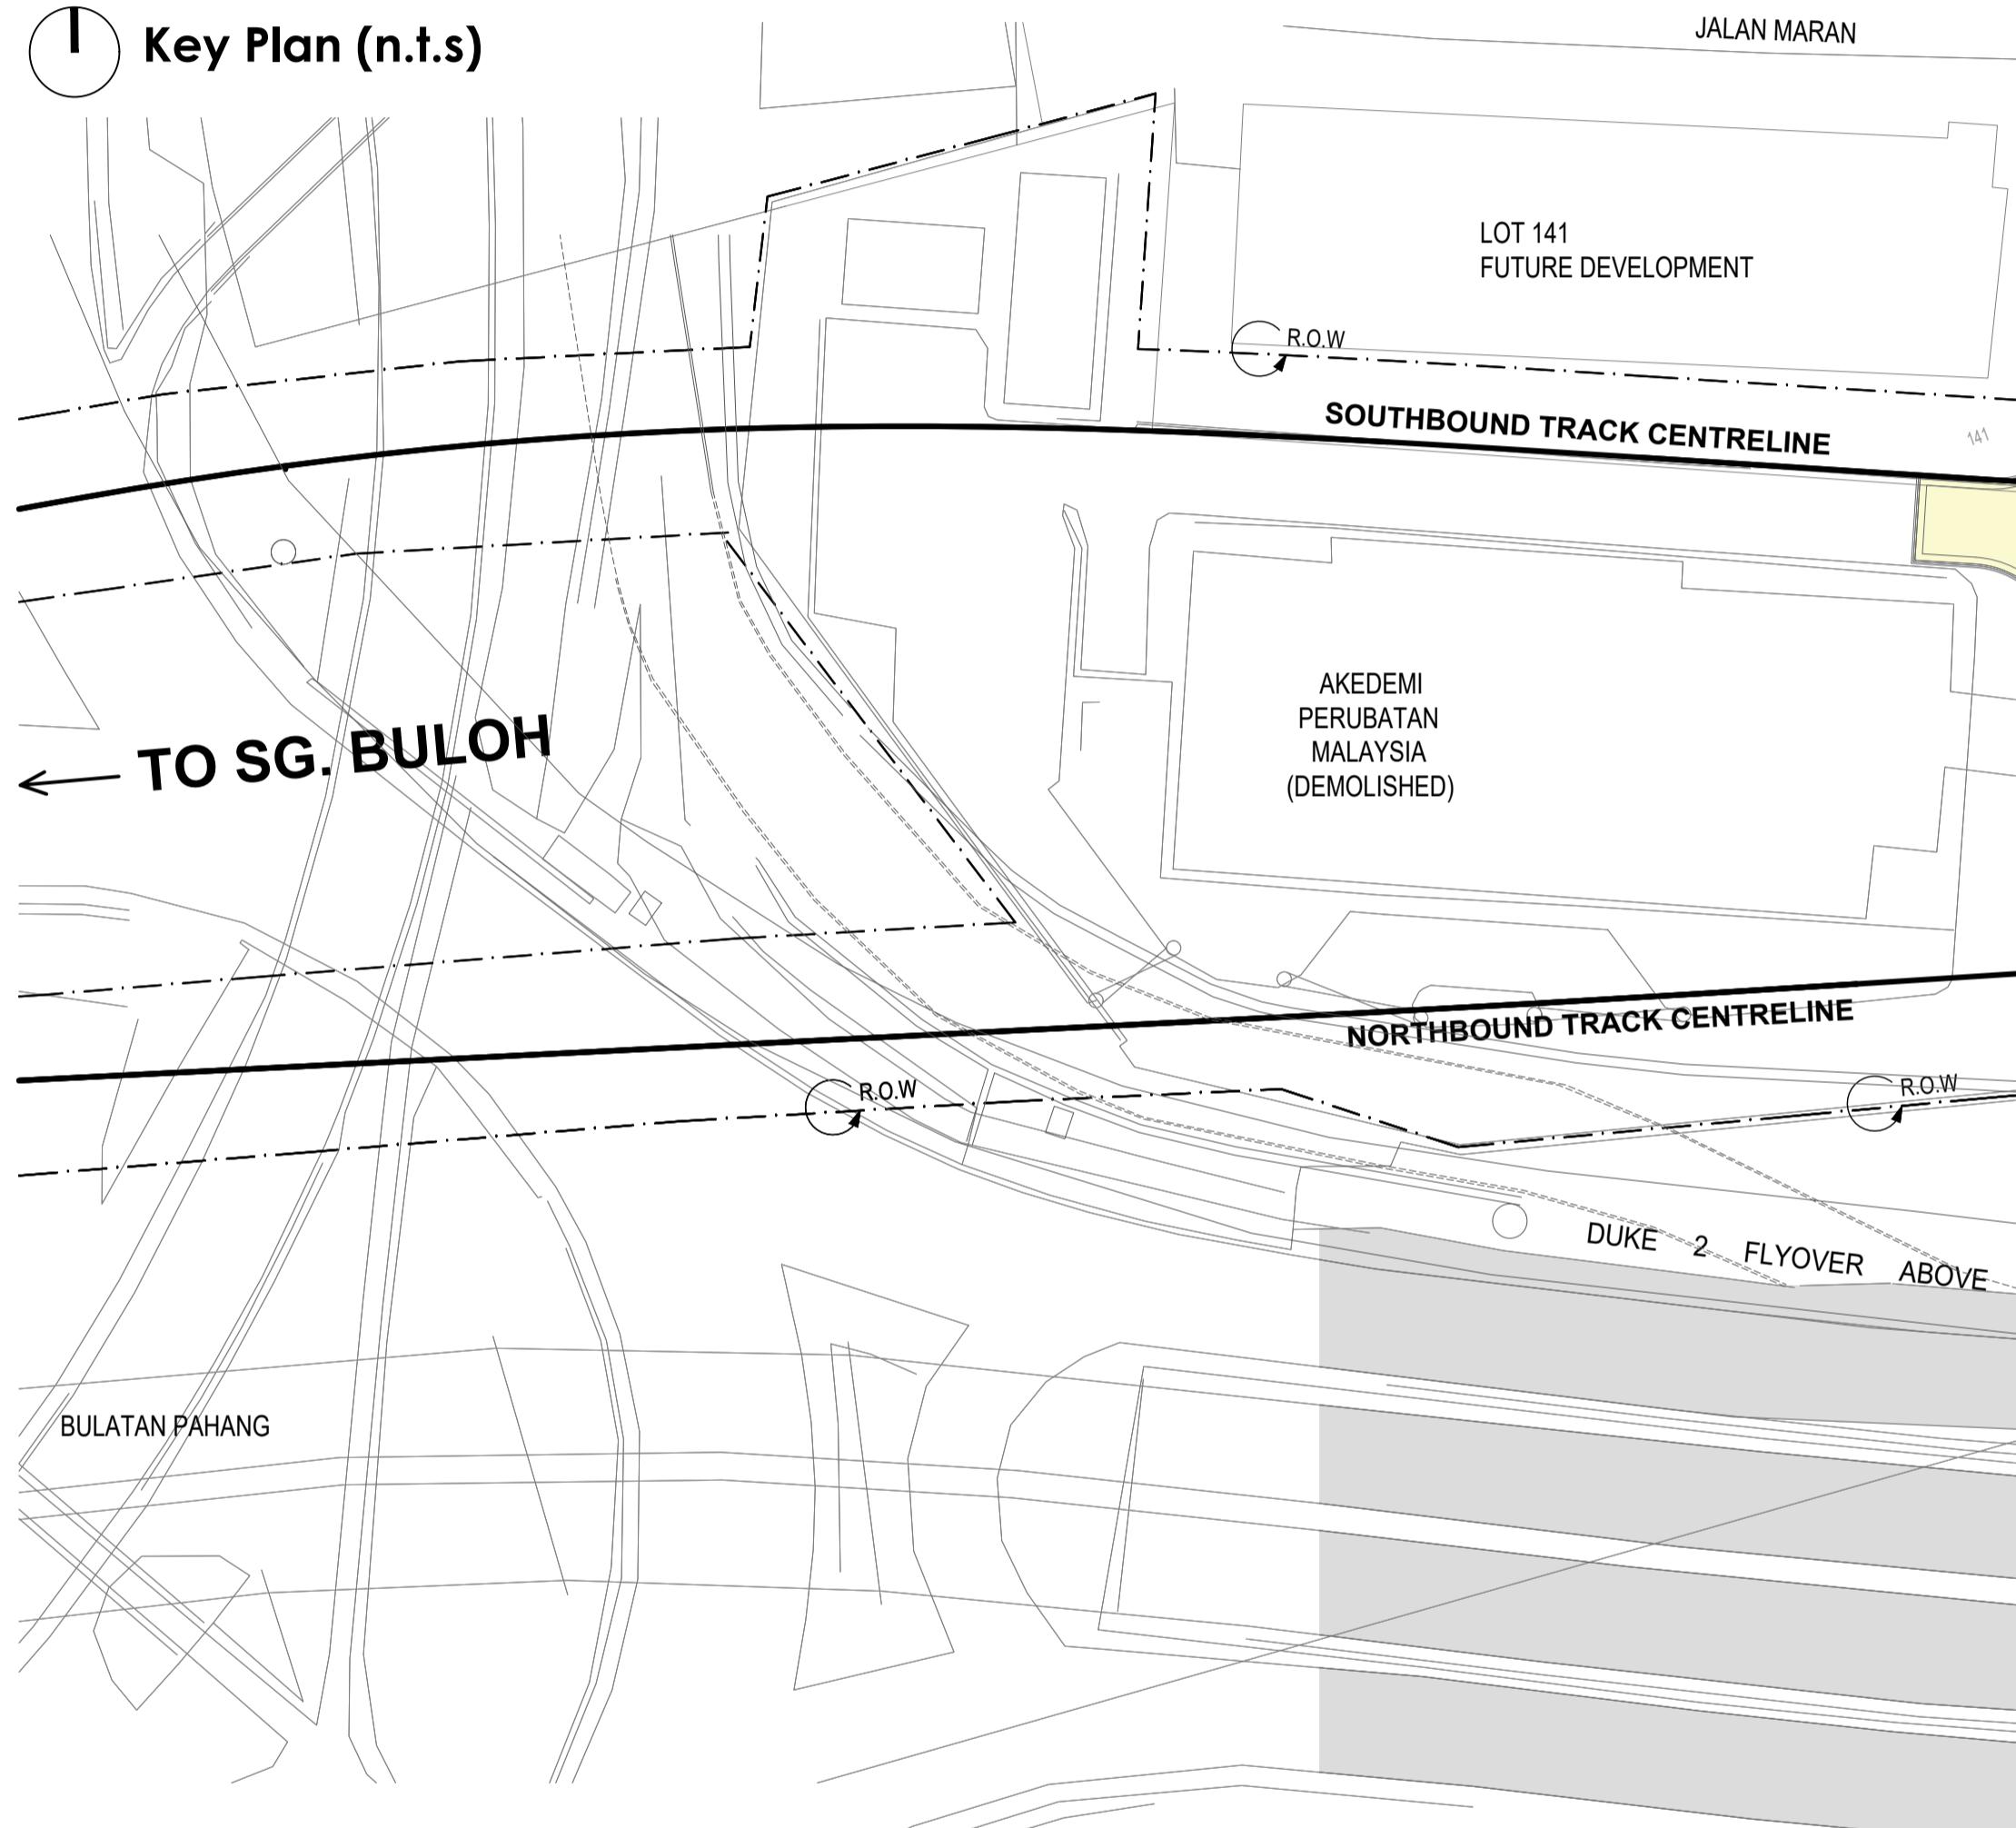


LOT 141  
FUTURE DEVELOPMENT

JALAN MARAN

JALAN KUANTAN

ISTANA BUDAYA

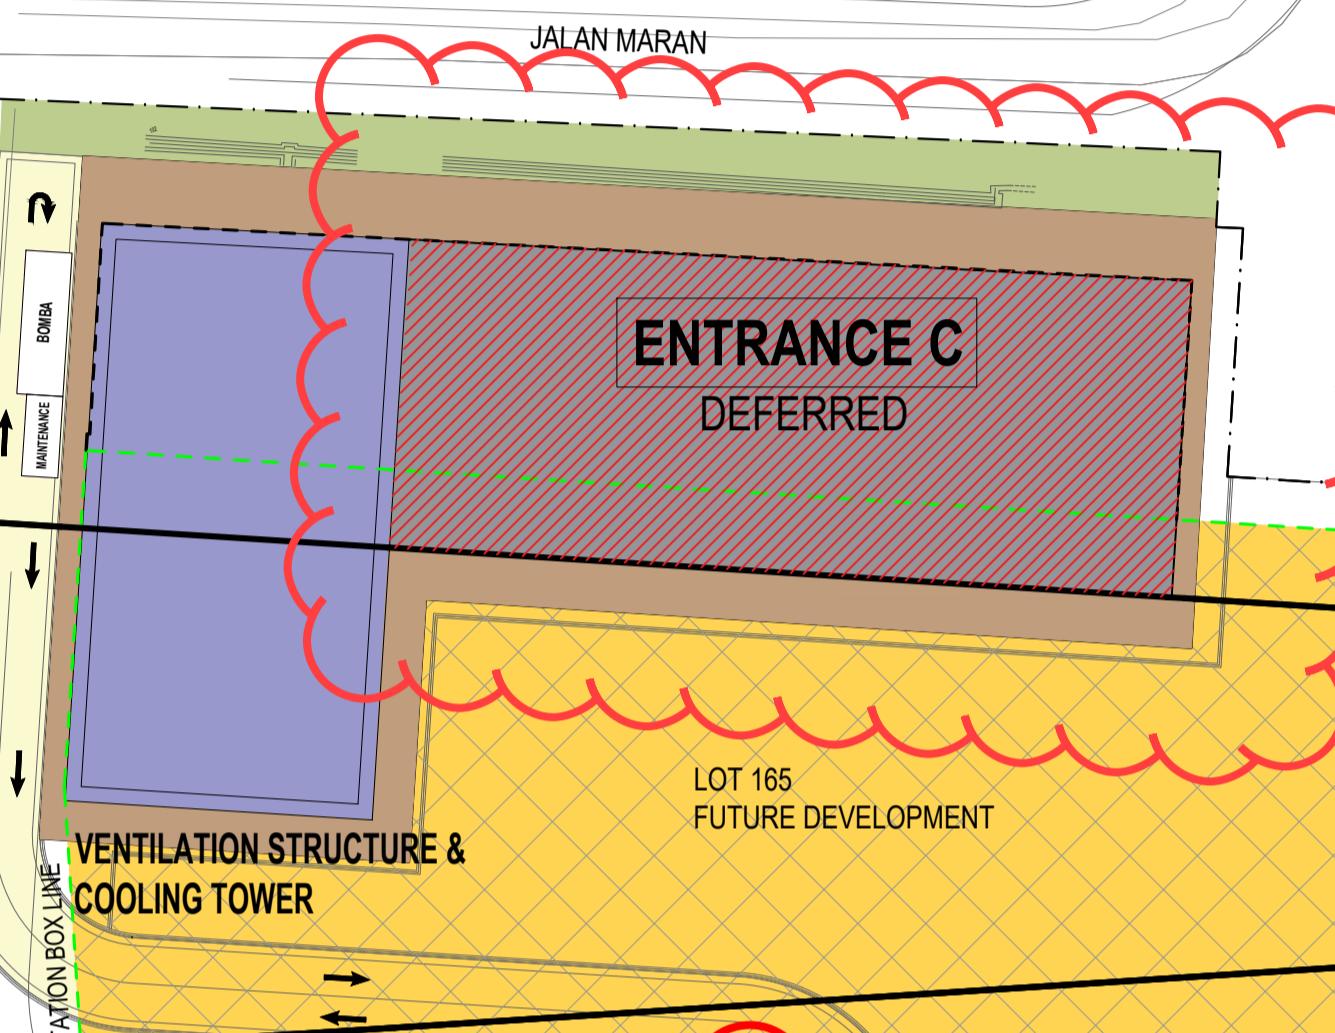

ENTRANCE B

LOT 141  
FUTURE DEVELOPMENT

TO SERDANG

LOT 165  
FUTURE DEVELOPMENT

LOT 141  
FUTURE DEVELOPMENT


VENTILATION STRUCTURE

VENTILATION STRUCTURE &  
COOLING TOWER

STATION BOX LINE

R.O.W.

STATION BOX LINE

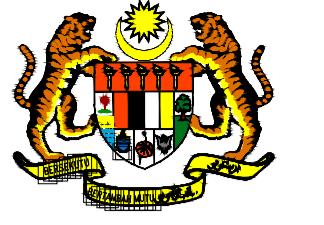

**KERAJAAN MALAYSIA**


PROJECT TITLE:  
PROJECT MASS RAPID TRANSIT LALUAN 2:  
PUTRAJAYA LINE  
(formerly known as PROJEK MRT LALUAN 2:  
SG BULOH - SERDANG - PUTRAJAYA (SSP))

PROJECT PACKAGE:  
**UNDERGROUND**

SUPERVISING AGENCY :  
**AGENSI PENGANGKUTAN AWAM DARAT (APAD)**  
LAND PUBLIC TRANSPORT AGENCY (APAD)  
**AGENSI PENGANGKUTAN AWAM DARAT (A.P.A.D.)**

ARAS G, M DAN 20, MENARA TUN ISMAIL MOHAMED ALI,  
NO. 25, JALAN RAJA LAUT,  
50470 KUALA LUMPUR.  
Tel (ARAS G): 603-2603 6700 / Tel (ARAS 20): 603-2603 6600  
Fax : 603-26036710


PROJECT OWNER :  
**MRT CORP**  
Mass Rapid Transit Corporation Sdn Bhd  
(902884-V)  
5th FLOOR MENARA I&P 1,  
JALAN DUNGUN, DAMANSARA HEIGHTS,  
50490 KUALA LUMPUR.

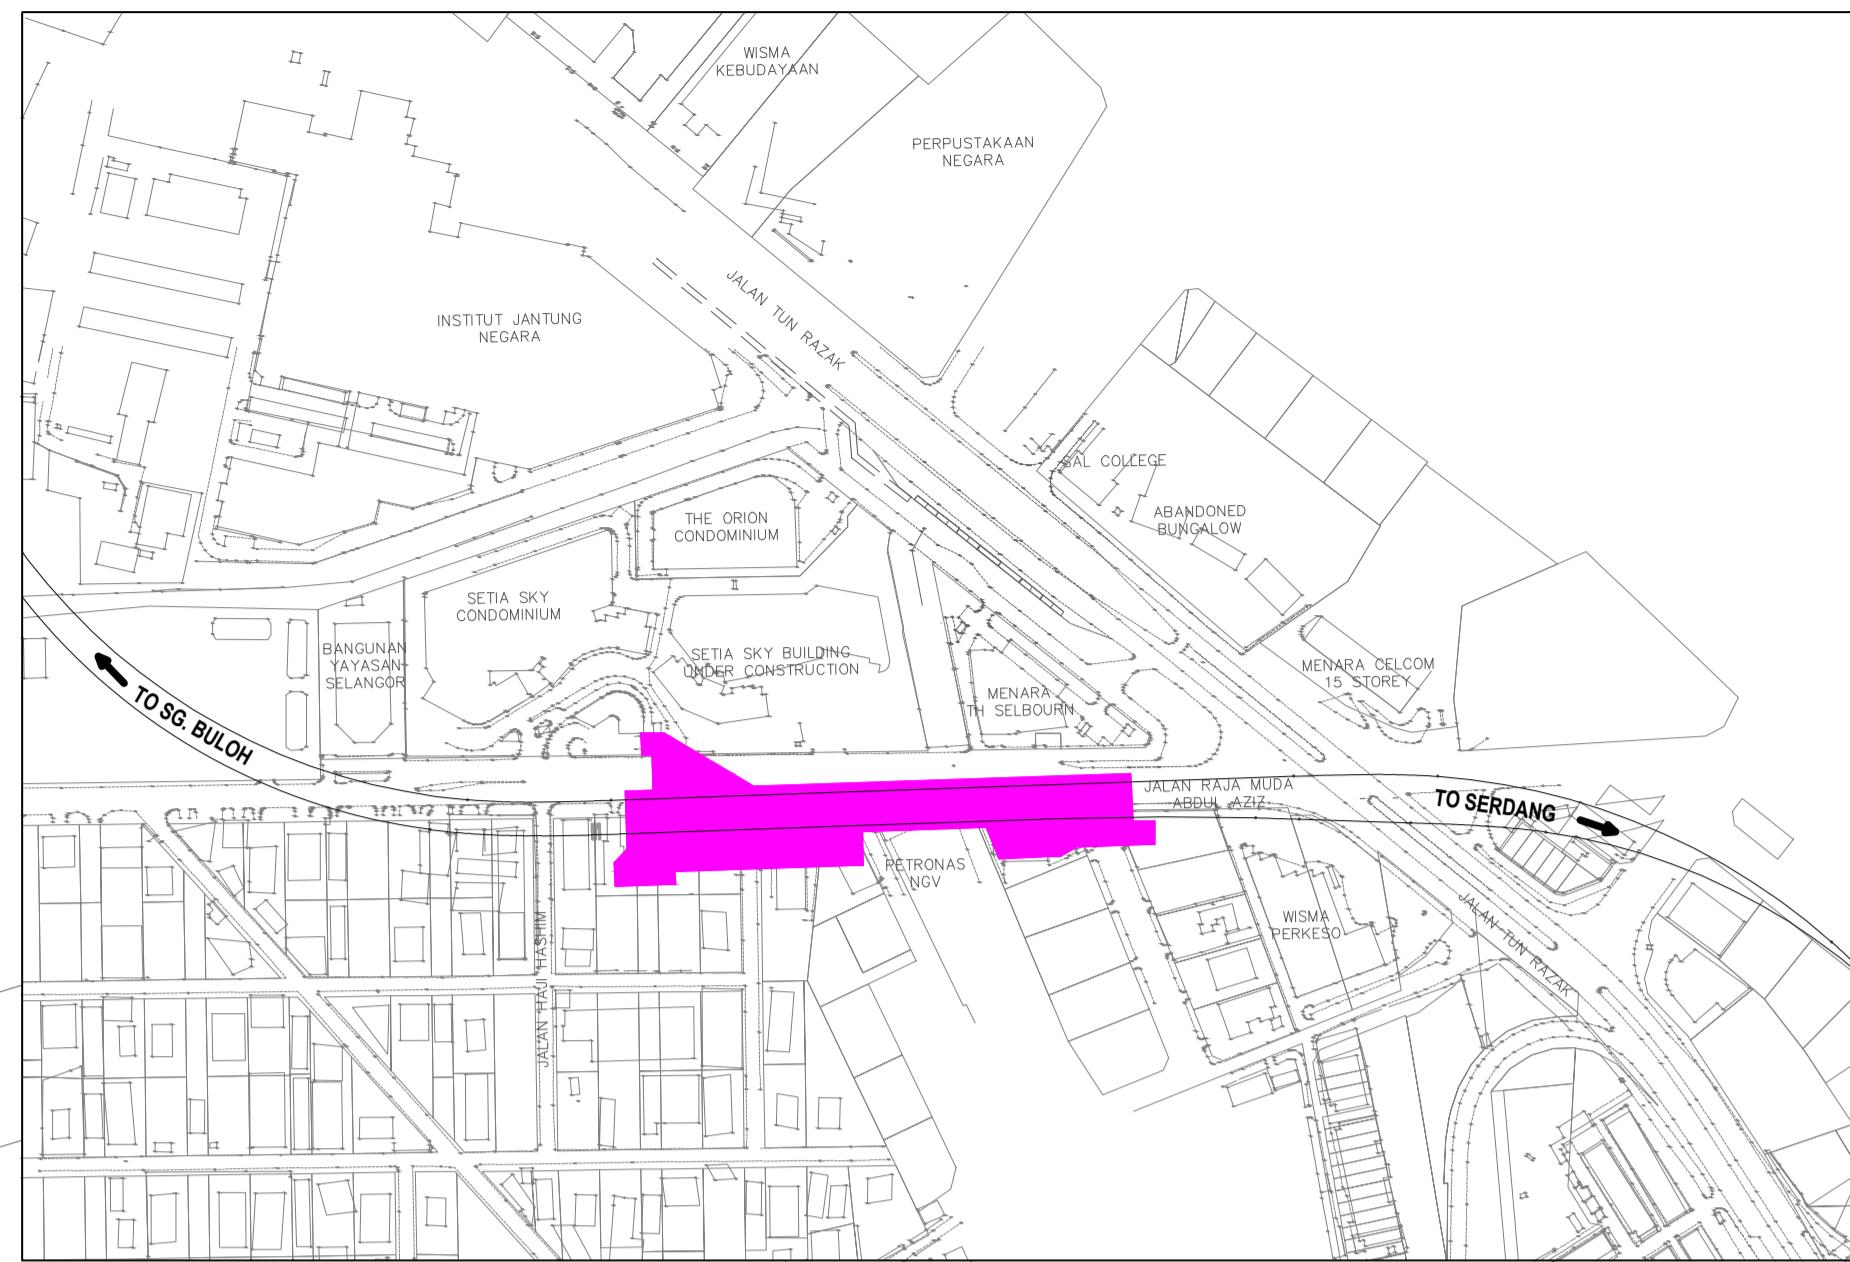

<b>Station, Link Bridge, Entrances</b>
<b>Entrance's Facilities (Lift,Stairs,Escalator)</b>
<b>Commuter's Facilities</b>
<b>Covered Facilities (MEP/MSPR/Ancillary)</b>
<b>Covered Walkway</b>
<b>Walkway</b>
<b>Landscape</b>
<b>Main Road</b>
<b>MRT Access Road &amp; Road Widening</b>
<b>Deferred / Omitted / Relocated</b>


#### Changes in Raja Uda (Kampung Baru)

- a) Station name to change to Raja Uda.
- b) Entrance C to be built in the future. A covered walkway to Entrance B will be provided.
- c) Additional laybys at Entrance D to be built.

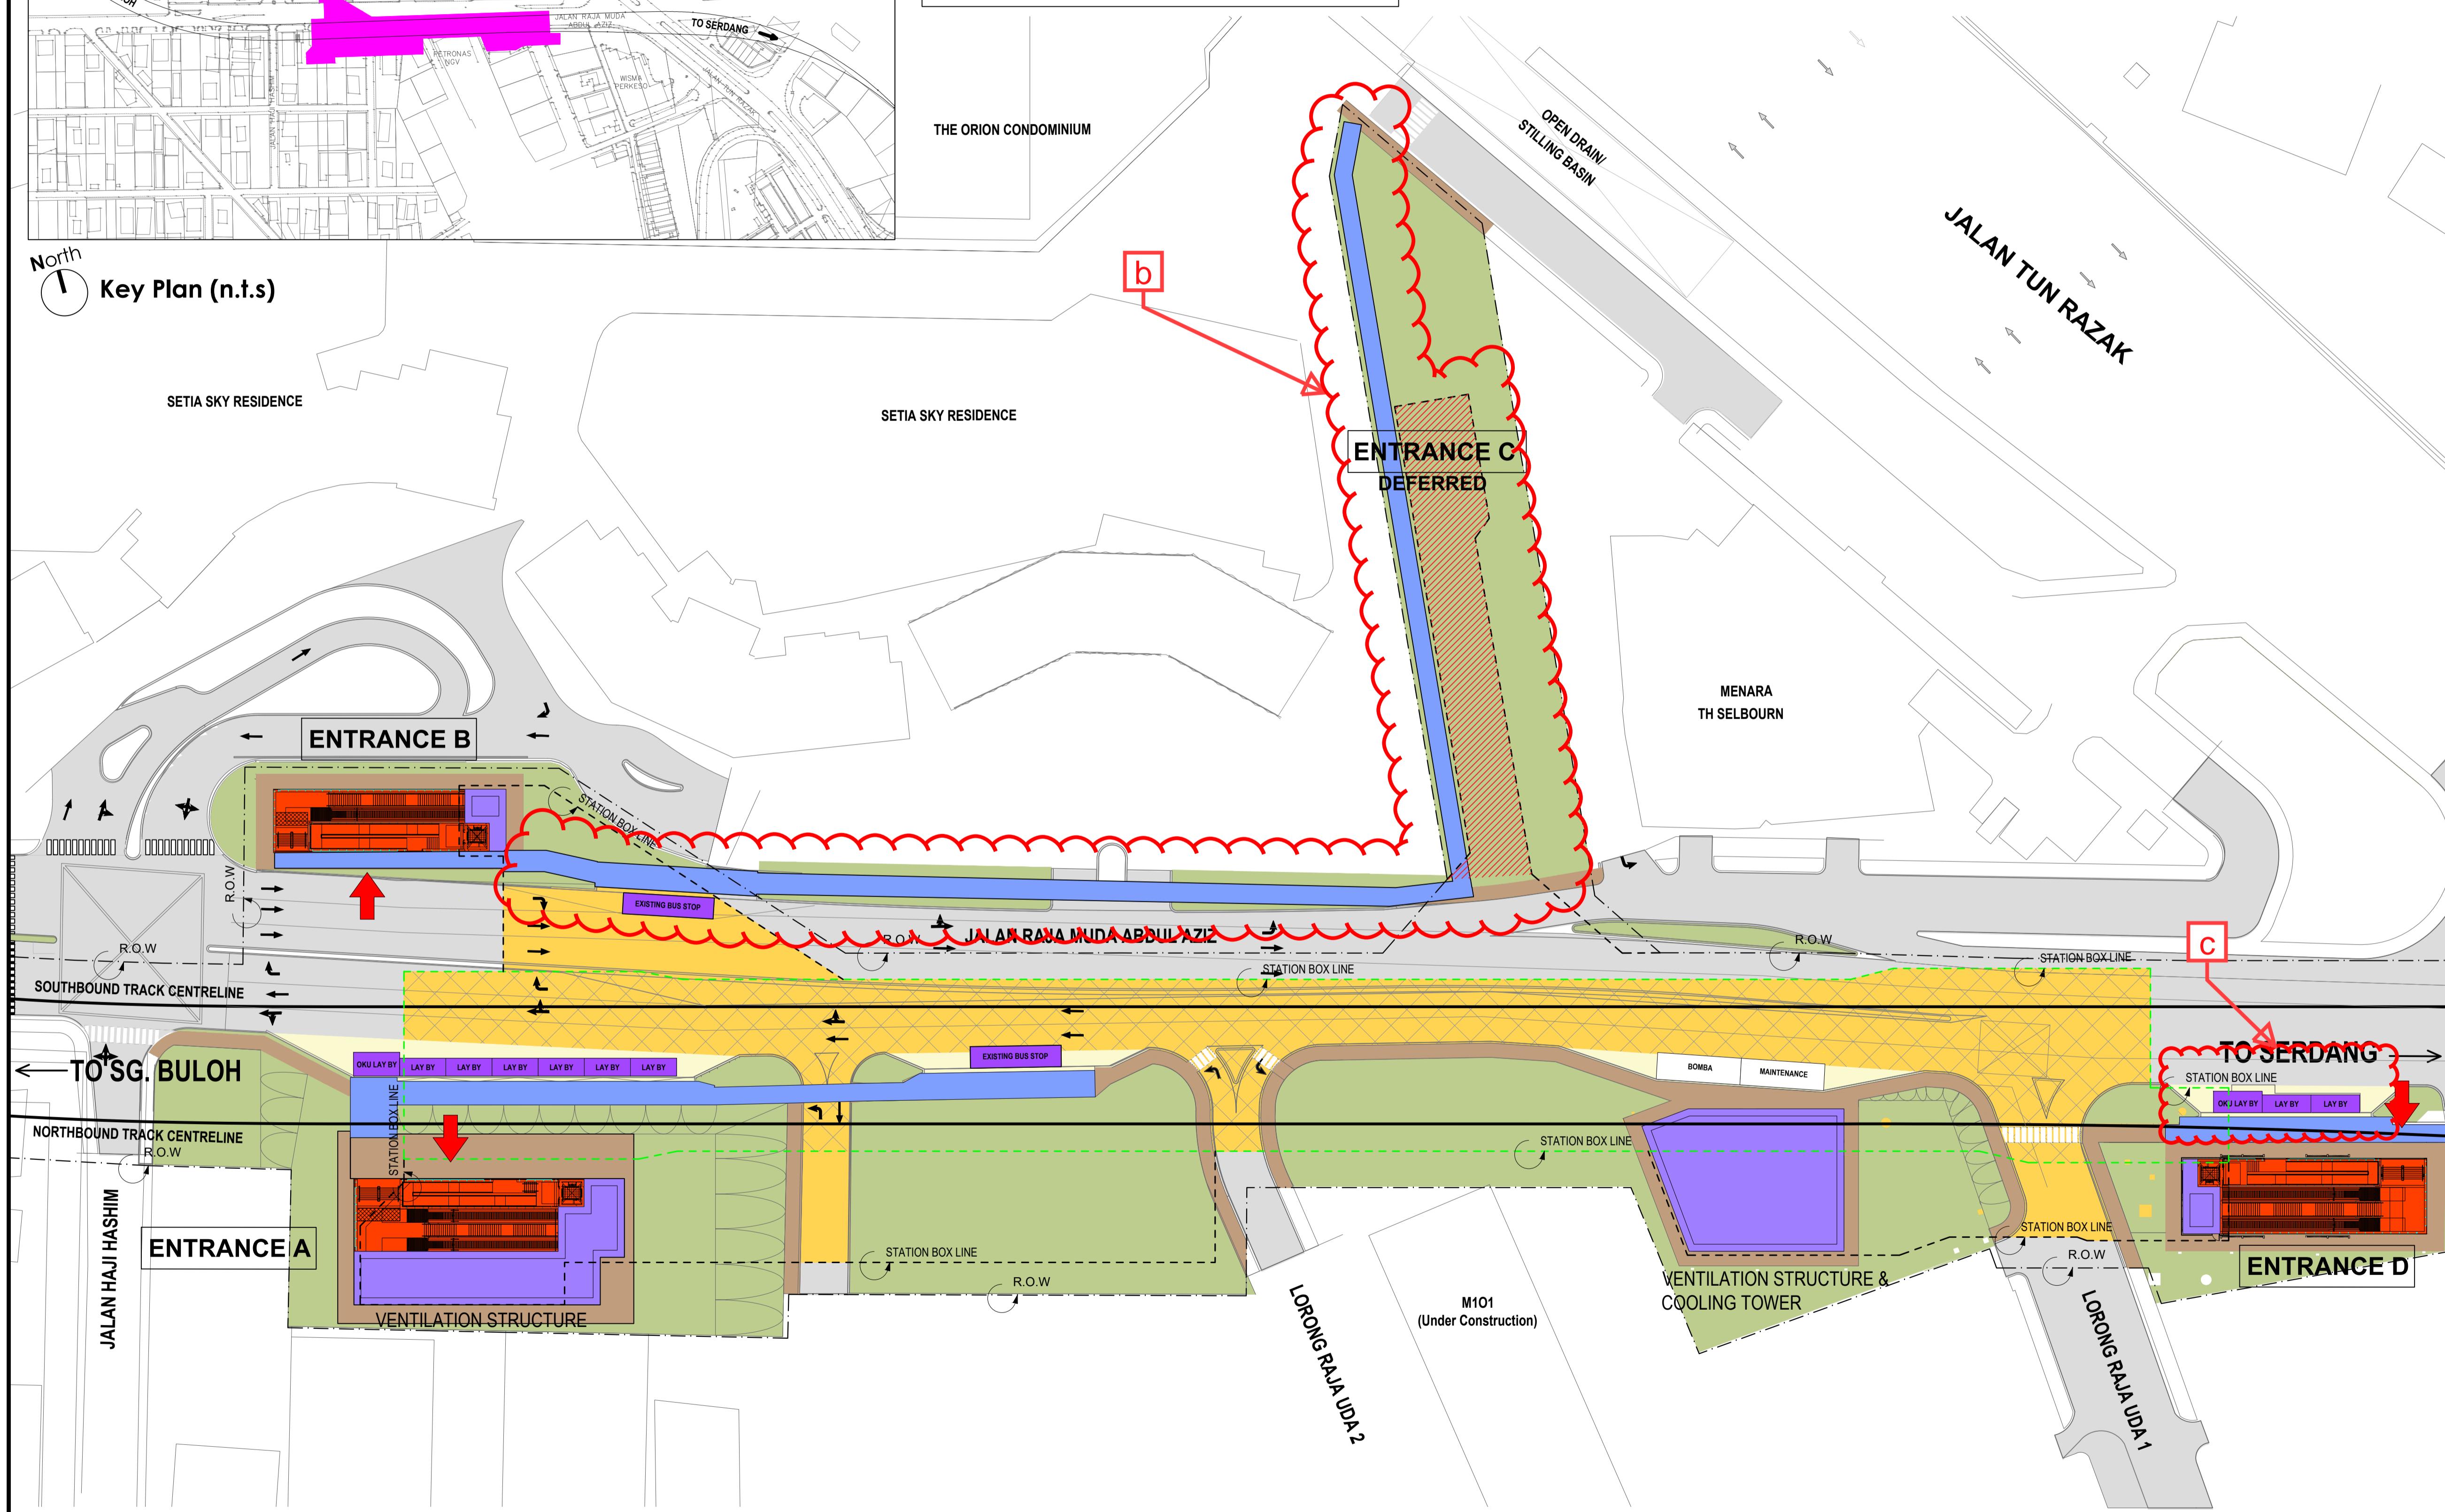

North  
1 : 500  
**Ground Context Plan Overall**

Drawing Title :  
**S19**  
RAJA UDA  
(PREVIOUSLY KNOWN AS KAMPUNG BARU NORTH)

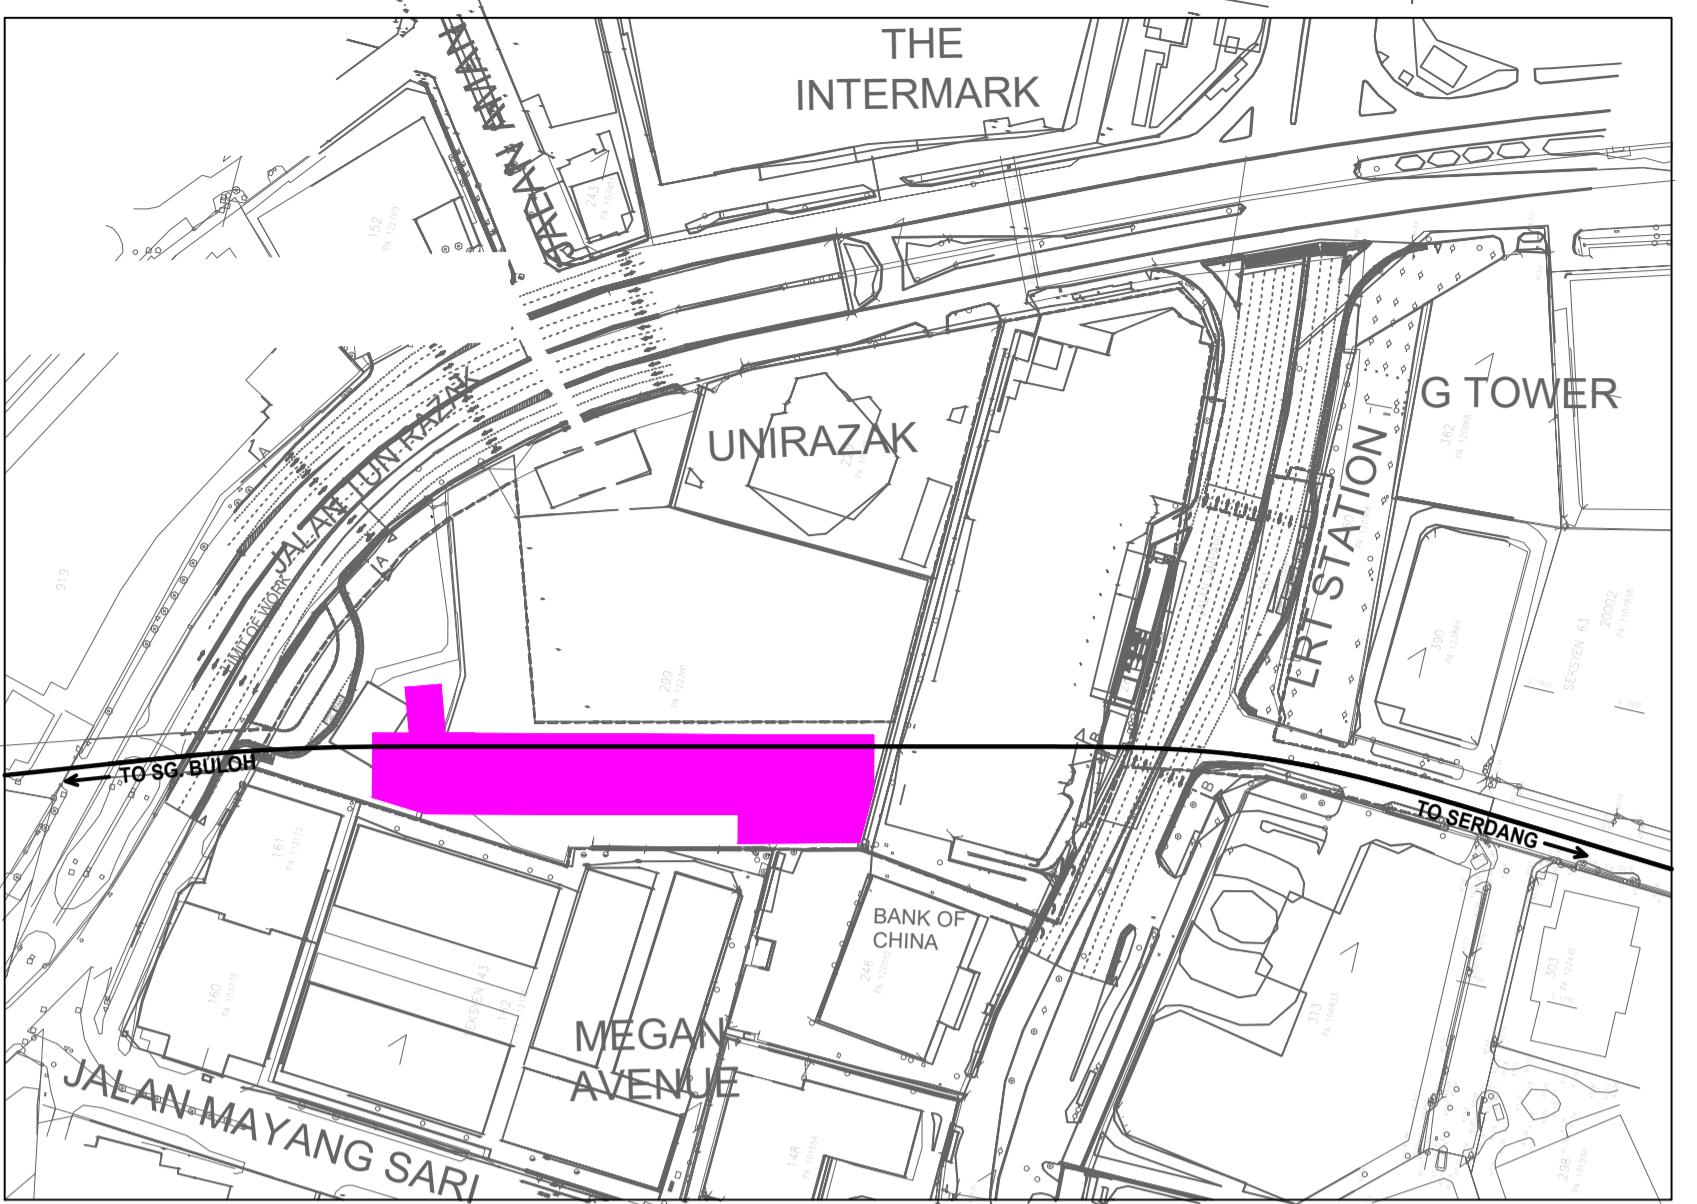

#### Changes in Ampang Park

- a) At-grade common concourse between MRT and LRT stations to be built.  
Underground common concourse with paid-to-paid link to be built in the future.



KERAJAAN MALAYSIA

PROJECT TITLE:  
PROJECT MASS RAPID TRANSIT LALUAN 2:  
PUTRAJAYA LINE  
(formerly known as PROJEK MRT LALUAN 2:  
SG BULOH - SERDANG - PUTRAJAYA (SSP))

PROJECT PACKAGE:  
UNDERGROUND

SUPERVISING AGENCY :  
**AGENSI PENGANGKUTAN AWAM DARAT (APAD)**  
LAND PUBLIC TRANSPORT AGENCY (APAD)  
AGENSI PENGANGKUTAN AWAM DARAT (A.P.A.D.)


ARAS G, M DAN 20, MENARA TUN ISMAIL MOHAMED ALI,  
NO. 25, JALAN RAJA LAUT,  
50470 KUALA LUMPUR.  
Tel (ARAS G): 603-2603 6700 / Tel (ARAS 20): 603-2603 6600  
Fax : 603-26036710

PROJECT OWNER :  
**MRT CORP**  
Mass Rapid Transit Corporation Sdn Bhd  
(902884-V)  
5th FLOOR MENARA I&P 1,  
JALAN DUNGUN, DAMANSARA HEIGHTS,  
50490 KUALA LUMPUR.

Drawing Title :

S20  
AMPANG PARK

North  
Key Plan (n.t.s)

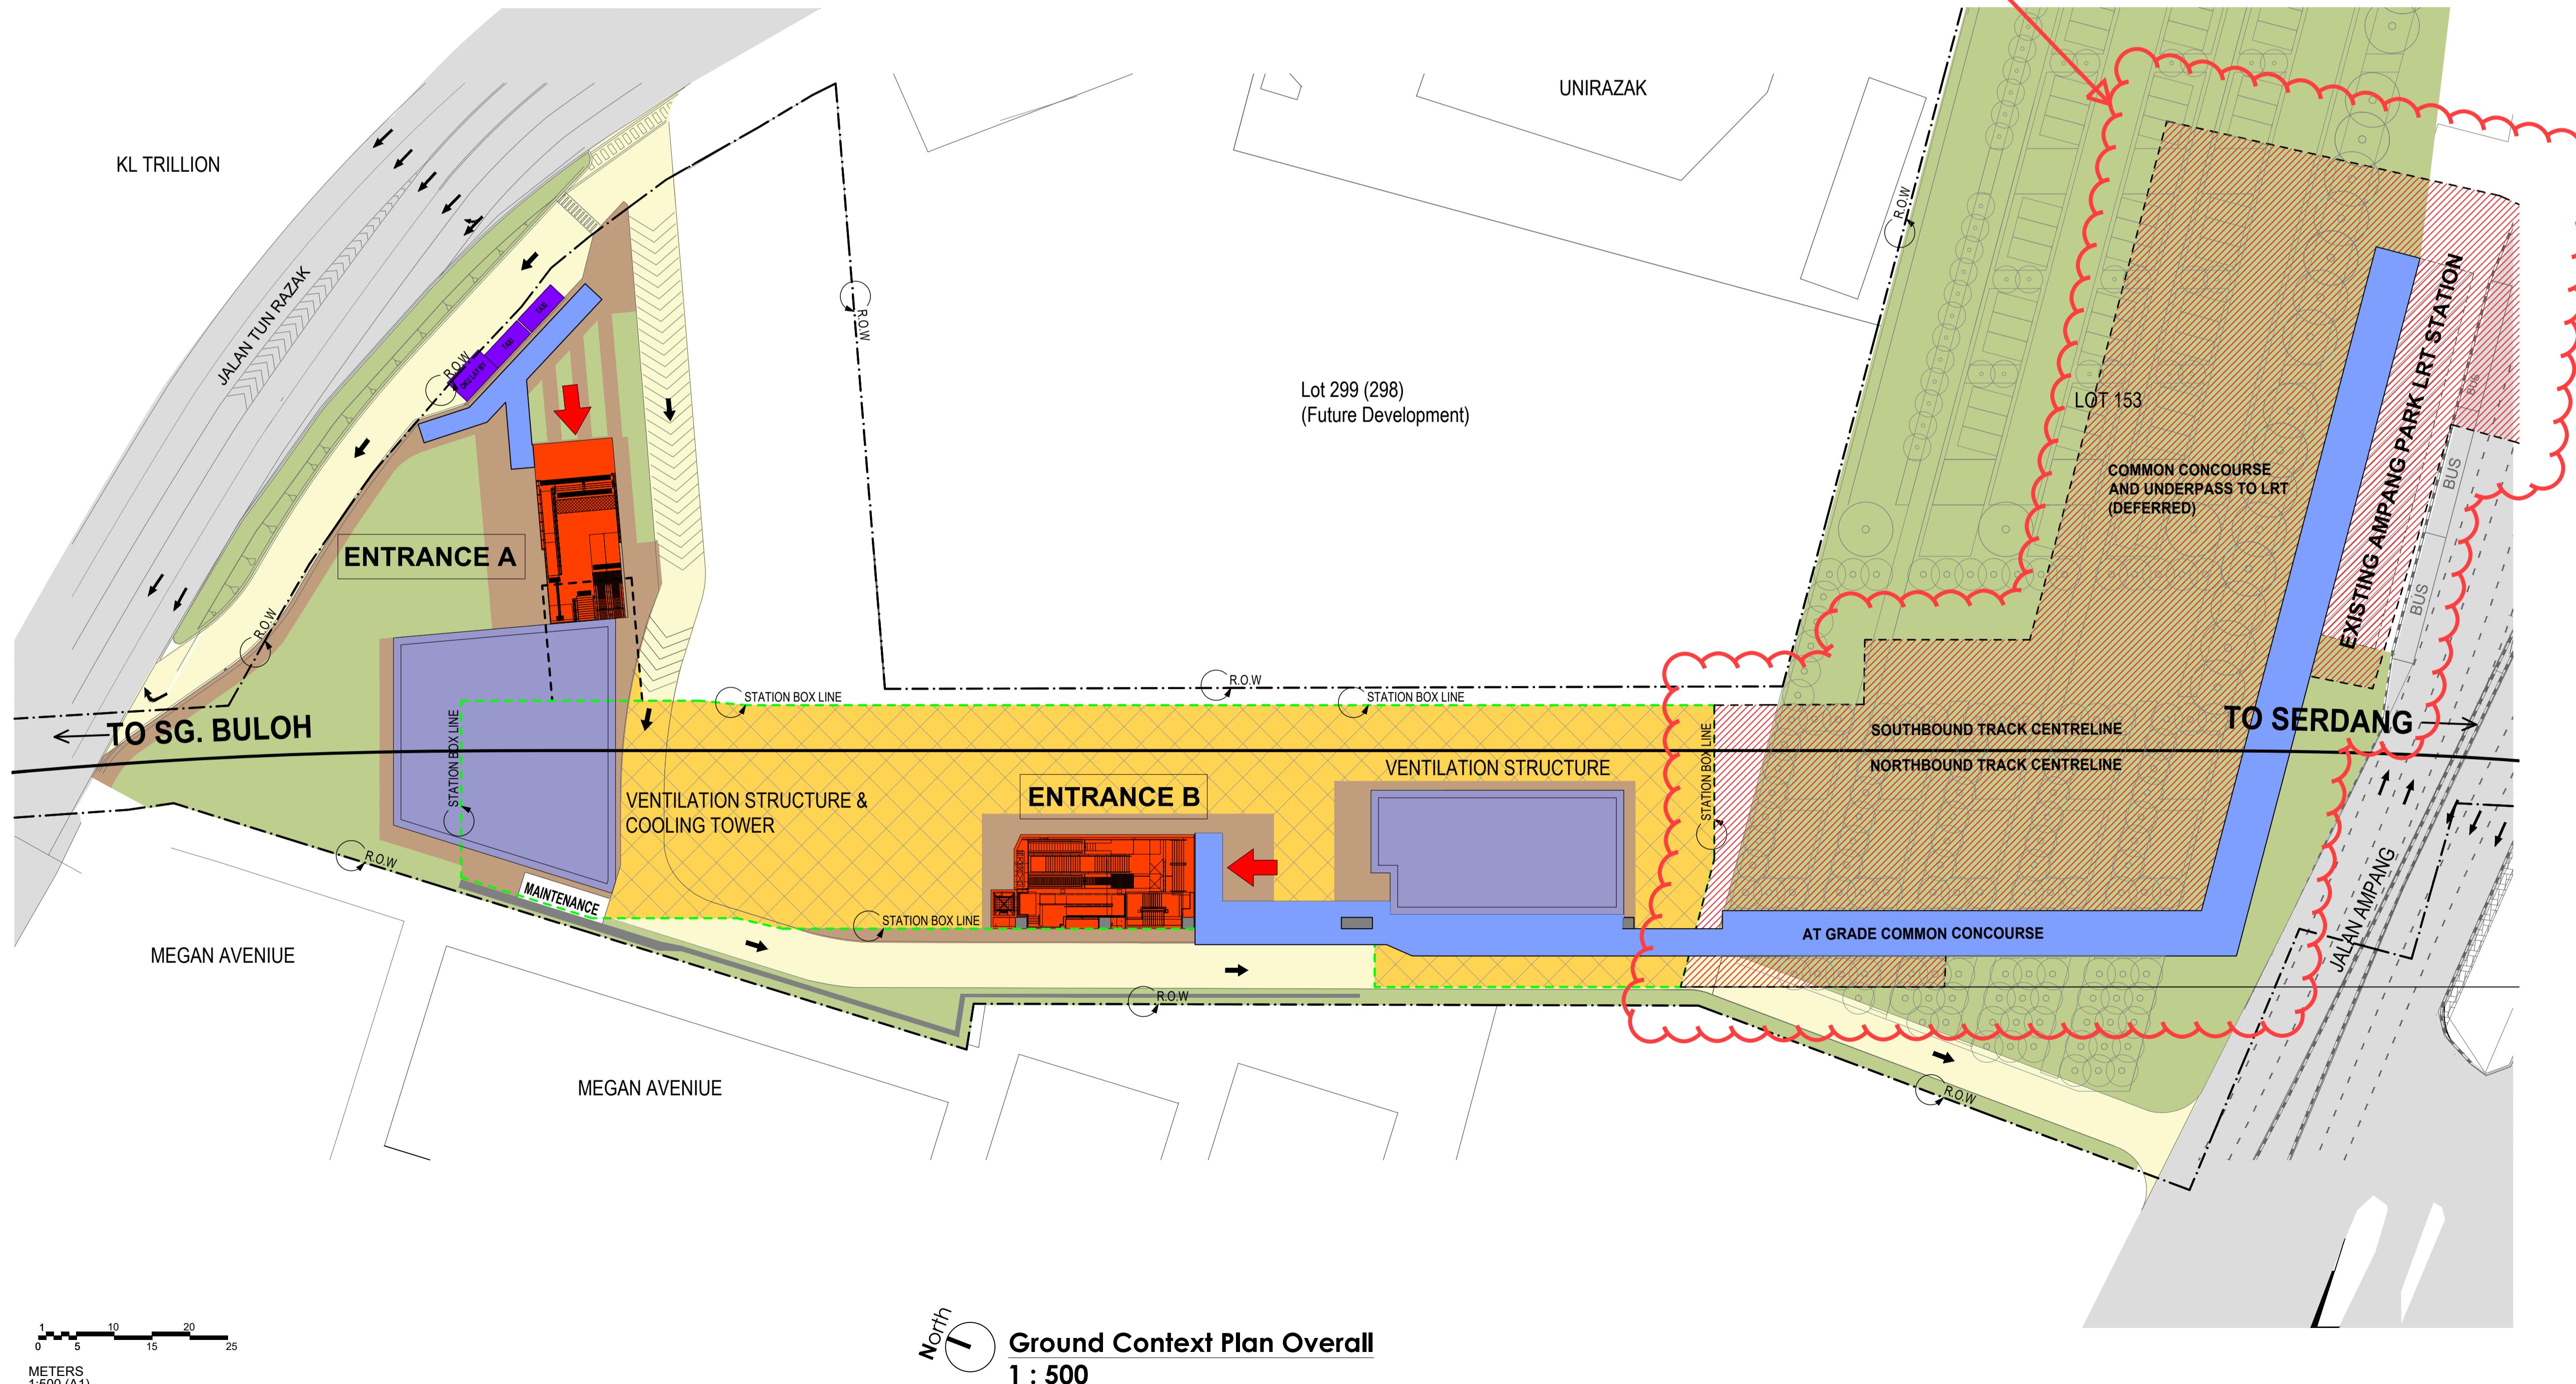



KERAJAAN MALAYSIA


PROJECT TITLE:  
PROJECT MASS RAPID TRANSIT LALUAN 2:  
PUTRAJAYA LINE  
(formerly known as PROJEK MRT LALUAN 2:  
SG BULOH - SERDANG - PUTRAJAYA (SSP))

PROJECT PACKAGE:  
UNDERGROUND

SUPERVISING AGENCY :  
**AGENSI PENGANGKUTAN AWAM DARAT (APAD)**  
LAND PUBLIC TRANSPORT AGENCY (APAD)  
AGENSI PENGANGKUTAN AWAM DARAT (A.P.A.D.)

ARAS G, M DAN 20, MENARA TUN ISMAIL MOHAMED ALI,  
NO. 25, JALAN RAJA LAUT,  
50470 KUALA LUMPUR.  
Tel (ARAS G): 603-2603 6700 / Tel (ARAS 20): 603-2603 6600  
Fax : 603-26036710


PROJECT OWNER :  
**MRT CORP**  
Mass Rapid Transit Corporation Sdn Bhd  
(902884-V)  
5th FLOOR MENARA I&P 1,  
JALAN DUNGUN, DAMANSARA HEIGHTS,  
50490 KUALA LUMPUR.

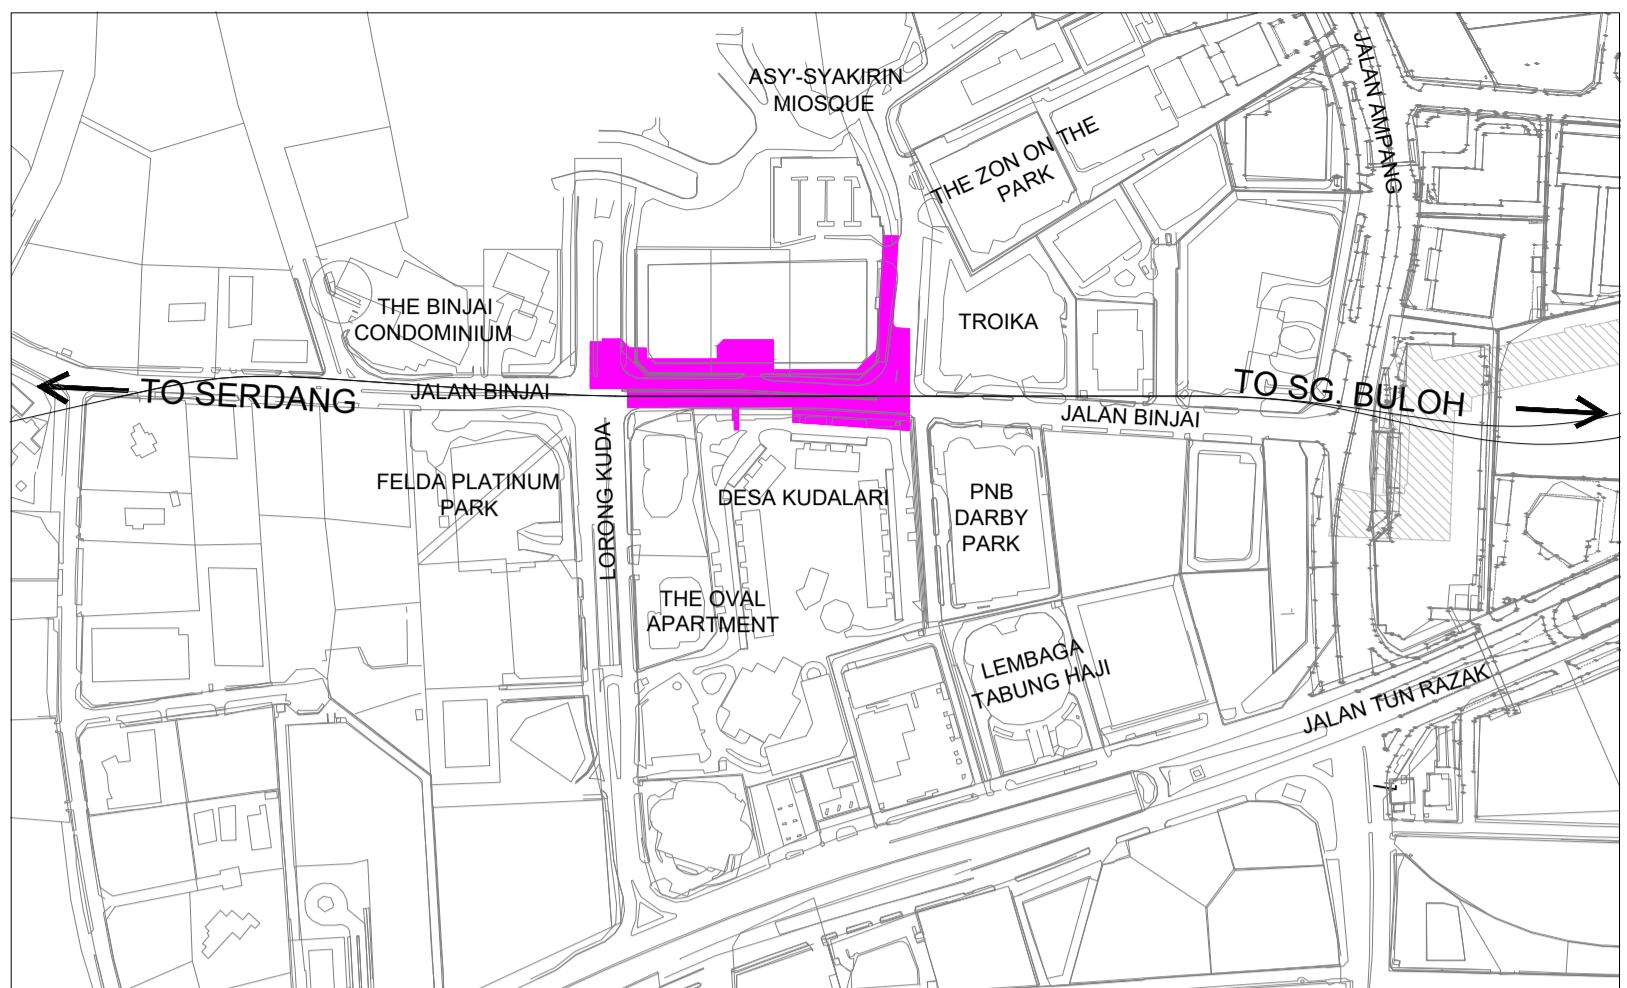

- Station, Link Bridge, Entrances
- Entrance's Facilities (Lift, Stairs, Escalator)
- Commuter's Facilities
- Covered Facilities (MEP/MSPR/Ancillary)
- Covered Walkway
- Walkway
- Landscape
- Main Road
- MRT Access Road & Road Widening
- Deferred / Omitted / Relocated


**Changes in Persiaran KLCC (KLCC East)**

- Station name to change to Persiaran KLCC.
- Entrance A to be built in the future by other party.
- Entrance C to be located within future development.

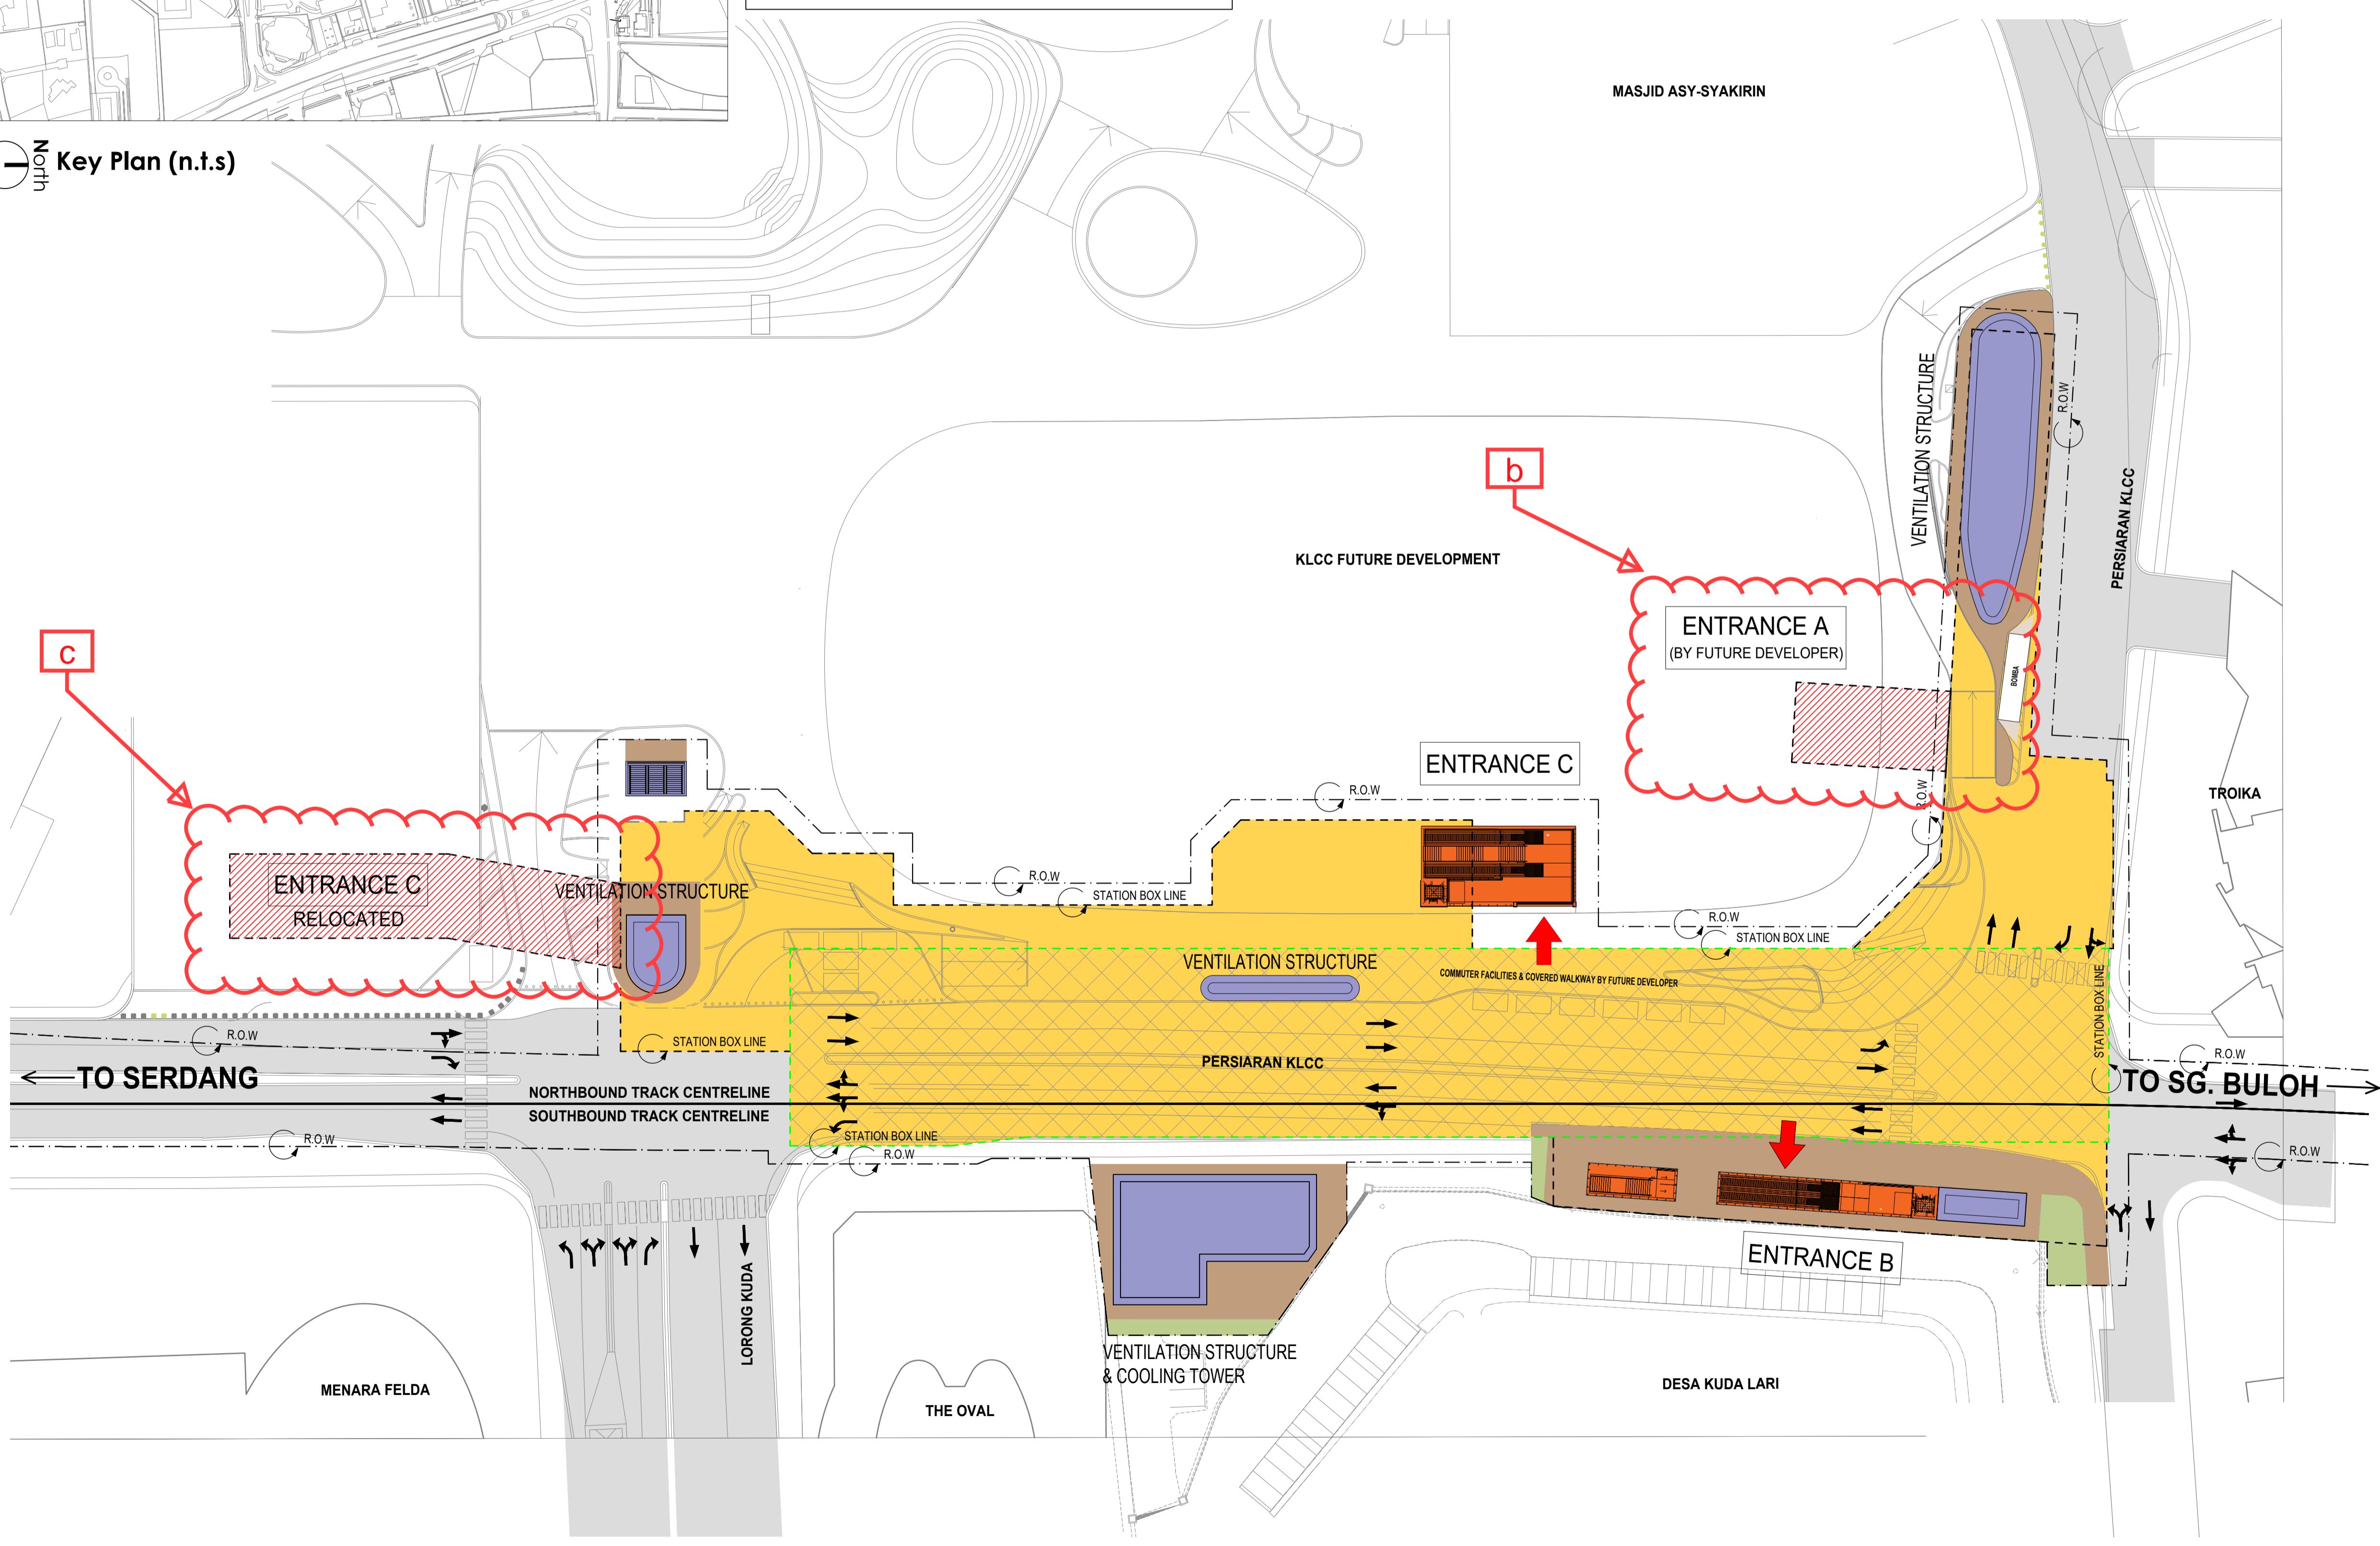

Ground Context Plan Overall  
1 : 500

Drawing Title :  
**S21**  
PERSIARAN KLCC  
(PREVIOUSLY KNOWN AS KLCC EAST)

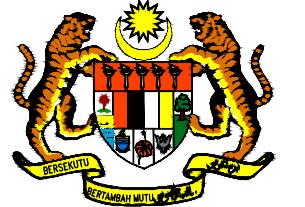

**KERAJAAN MALAYSIA**

PROJECT TITLE:  
PROJECT MASS RAPID TRANSIT LALUAN 2:  
PUTRAJAYA LINE  
(formerly known as PROJEK MRT LALUAN 2:  
SG BULOH - SERDANG - PUTRAJAYA (SSP))

PROJECT PACKAGE:  
**UNDERGROUND**

SUPERVISING AGENCY :  
**AGENSI PENGANGKUTAN AWAM DARAT (APAD)**  
LAND PUBLIC TRANSPORT AGENCY (APAD)  
**AGENSI PENGANGKUTAN AWAM DARAT (A.P.A.D.)**

ARAS G, M DAN 20, MENARA TUN ISMAIL MOHAMED ALI,  
NO. 25, JALAN RAJA LAUT,  
50470 KUALA LUMPUR,  
Tel (ARAS G): 603-2603 6700 / Tel (ARAS 20): 603-2603 6600  
Fax : 603-26036710


PROJECT OWNER :



**Mass Rapid Transit Corporation Sdn Bhd**  
(902884-V)  
5TH FLOOR MENARA I&P 1,  
JALAN DUNGUN, DAMANSARA HEIGHTS,  
50490 KUALA LUMPUR.


Drawing Title :

S22  
CONLAY

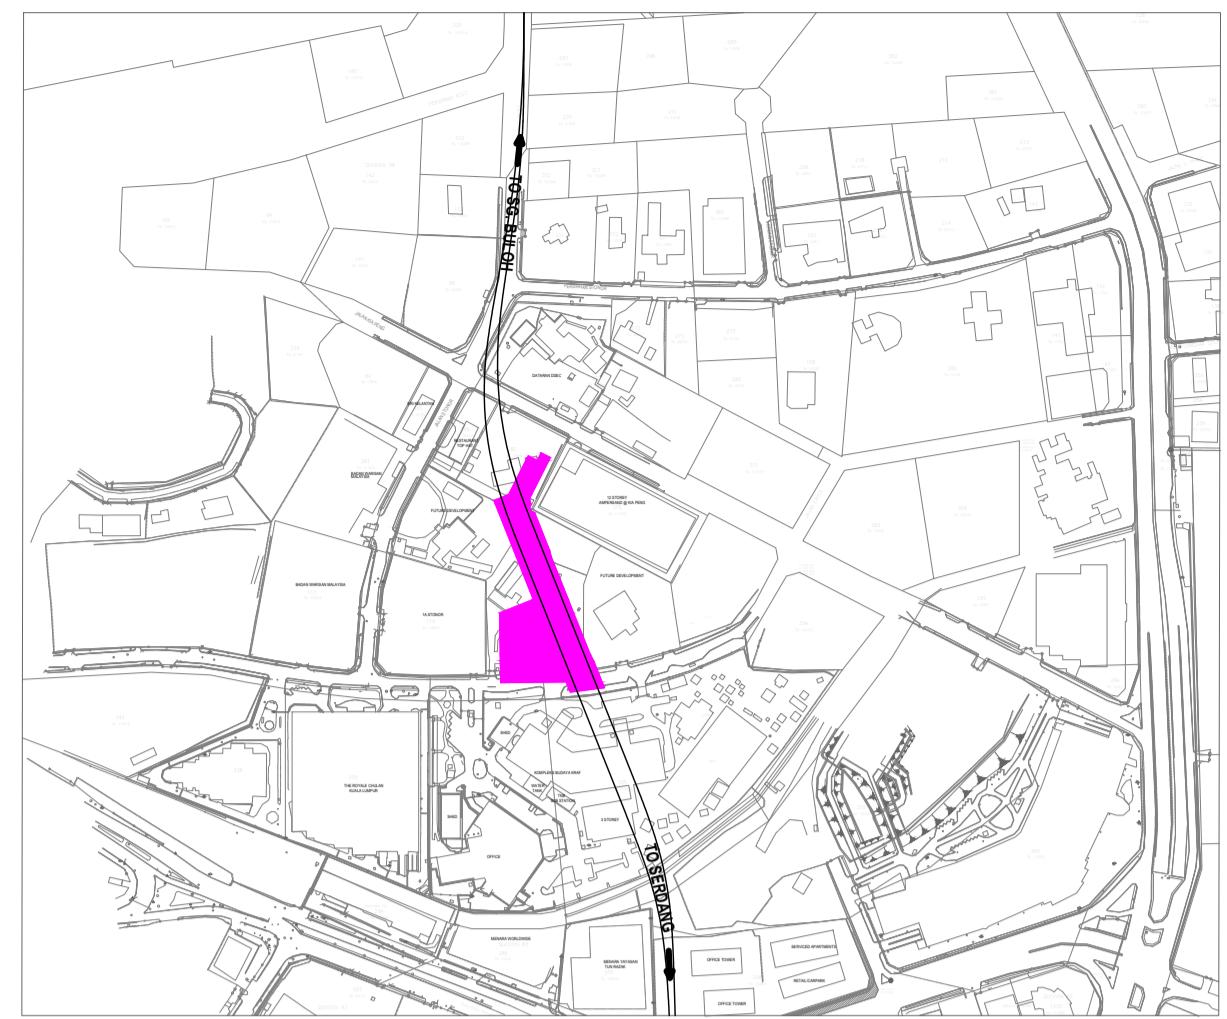

- Station, Link Bridge, Entrances
- Entrance's Facilities (Lift,Stairs,Escalator)
- Commuter's Facilities
- Covered Facilities (MEP/MSPR/Ancillary)
- Covered Walkway
- Walkway
- Landscape
- Main Road
- MRT Access Road & Road Widening
- Deferred / Omitted / Relocated

Changes in Conlay  
a) No changes.

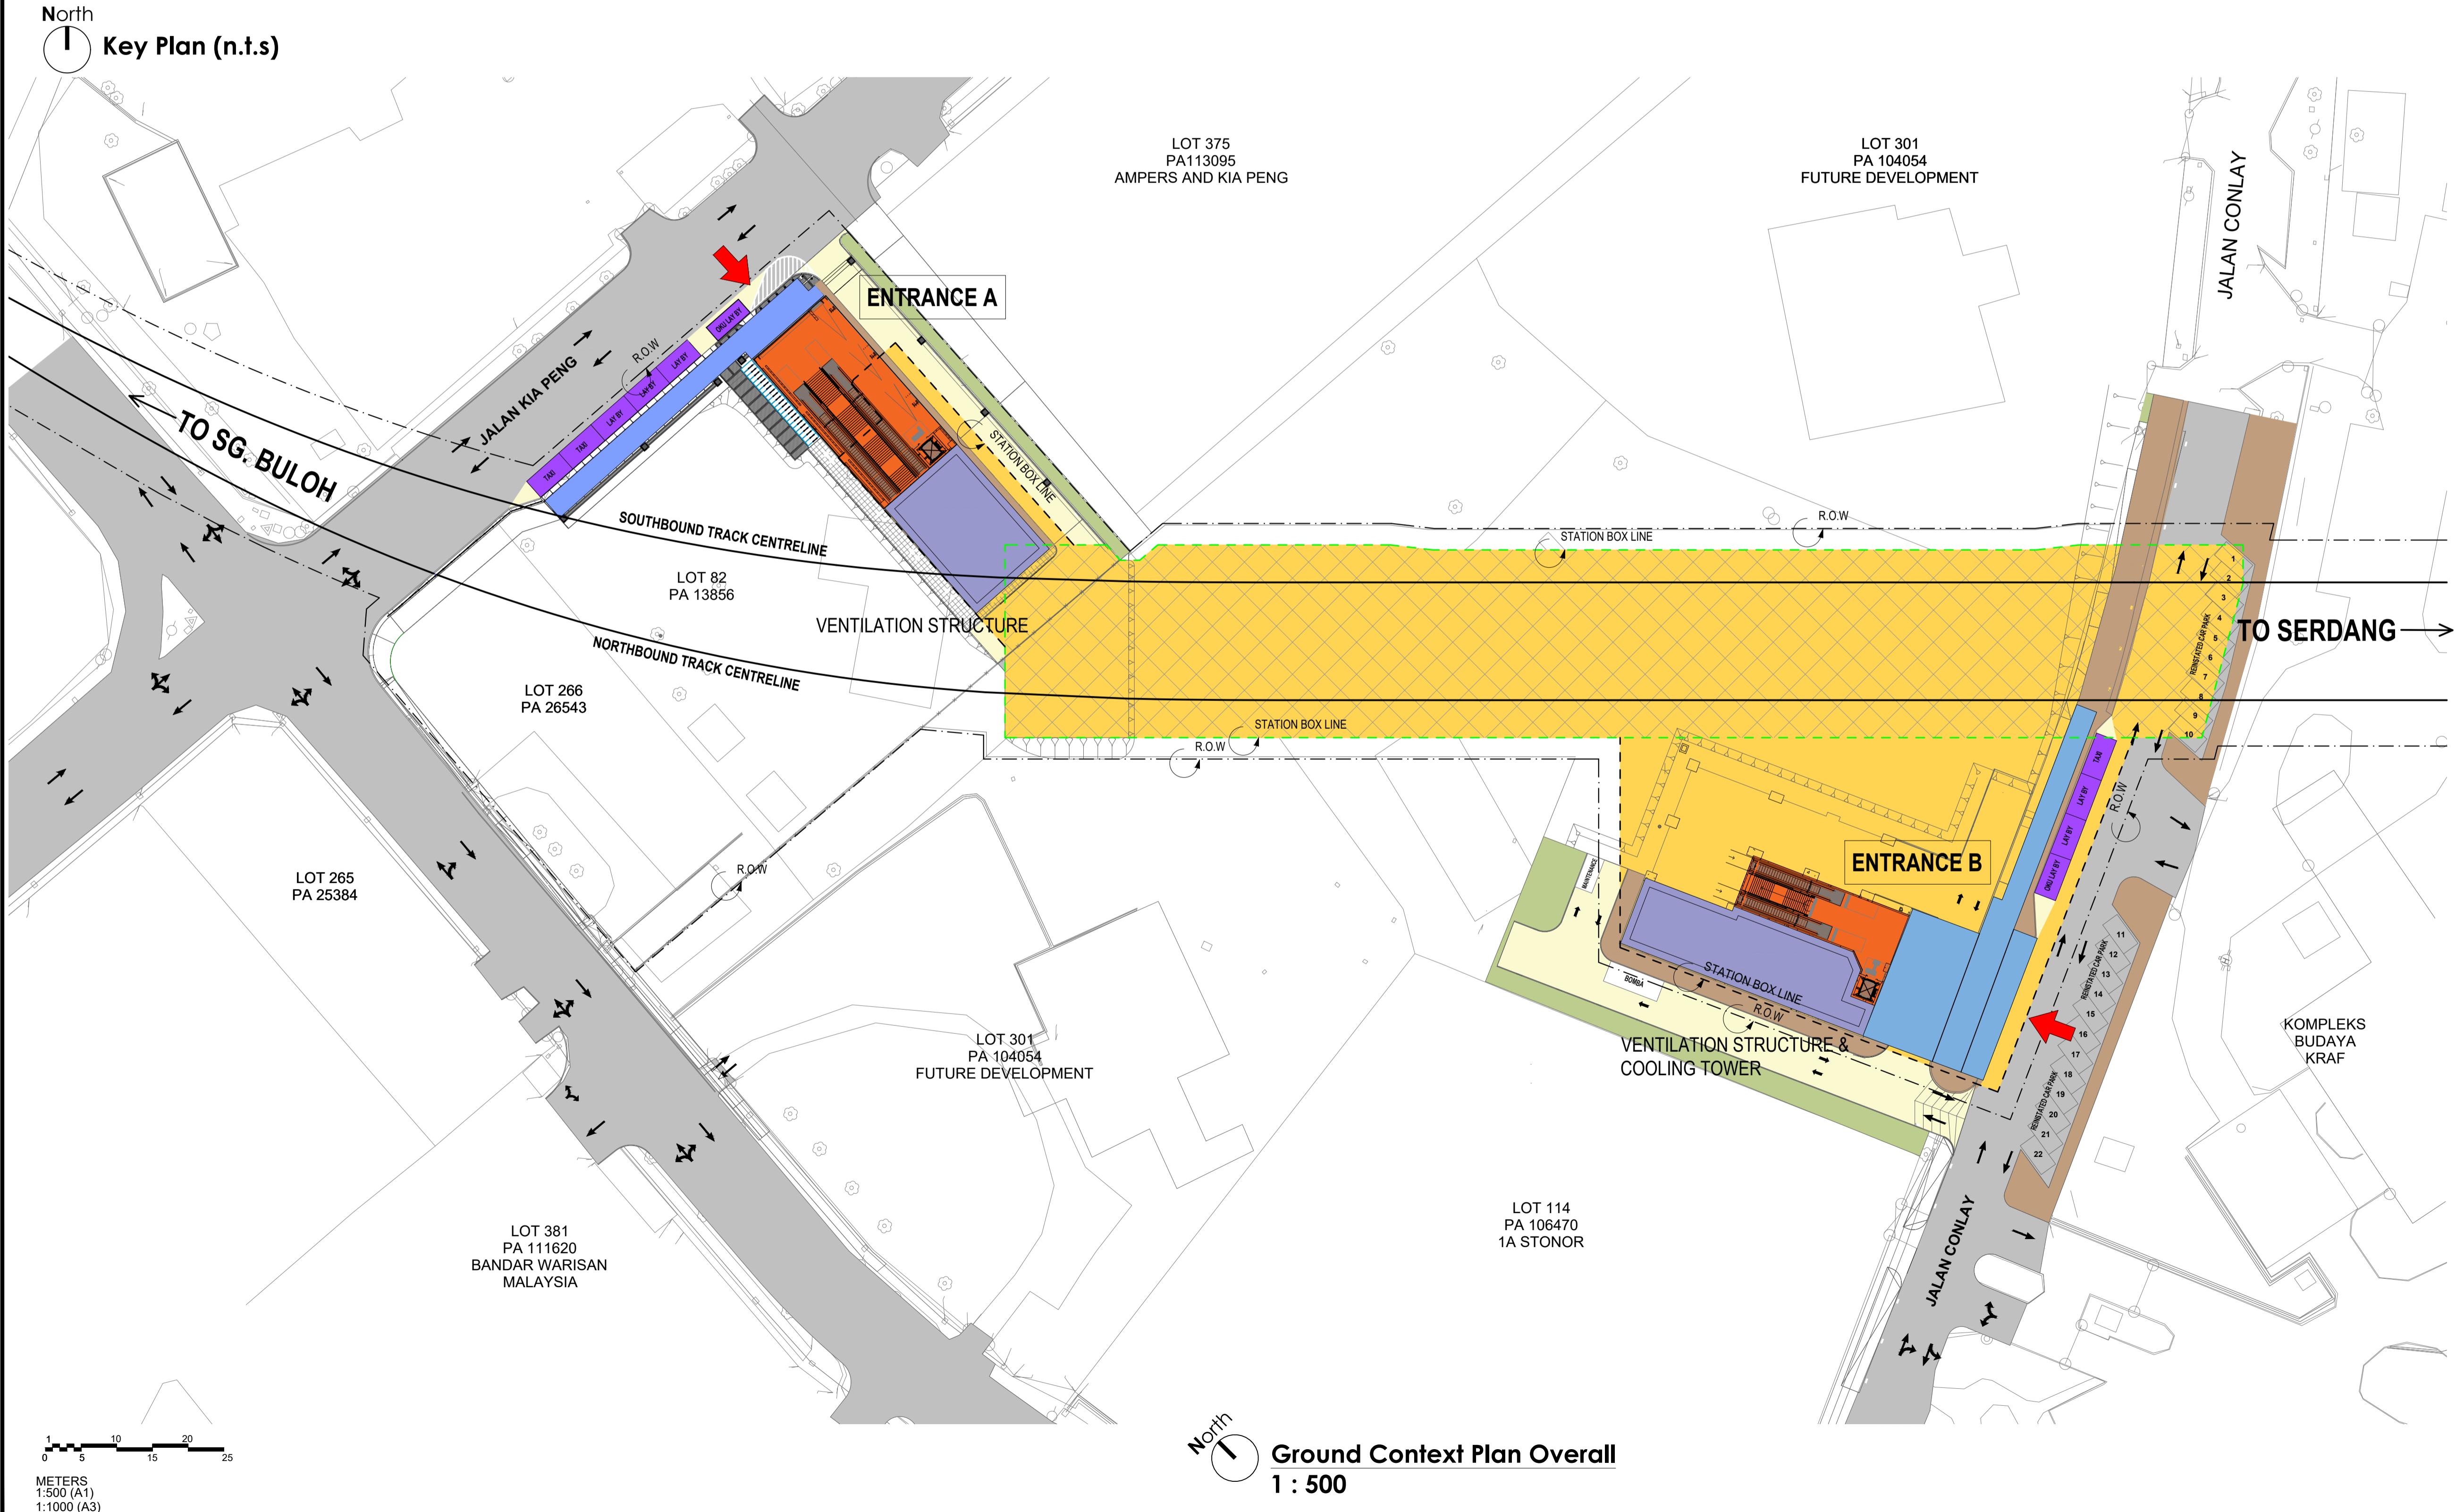



KERAJAAN MALAYSIA


PROJECT TITLE:  
PROJECT MASS RAPID TRANSIT LALUAN 2:  
PUTRAJAYA LINE  
(formerly known as PROJEK MRT LALUAN 2:  
SG BULOH - SERDANG - PUTRAJAYA (SSP))

PROJECT PACKAGE:  
UNDERGROUND

SUPERVISING AGENCY :  
**AGENSI PENGANGKUTAN AWAM DARAT (APAD)**  
LAND PUBLIC TRANSPORT AGENCY (APAD)  
AGENSI PENGANGKUTAN AWAM DARAT (A.P.A.D.)

ARAS G, M DAN 20, MENARA TUN ISMAIL MOHAMED ALI,  
NO. 25, JALAN RAJA LAUT,  
50470 KUALA LUMPUR.  
Tel (ARAS G): 603-2603 6700 / Tel (ARAS 20): 603-2603 6600  
Fax : 603-26036710

PROJECT OWNER :  
**MRT CORP**  
Mass Rapid Transit Corporation Sdn Bhd  
(902884-V)  
5th FLOOR MENARA I&P 1,  
JALAN DUNGUN, DAMANSARA HEIGHTS,  
50490 KUALA LUMPUR.

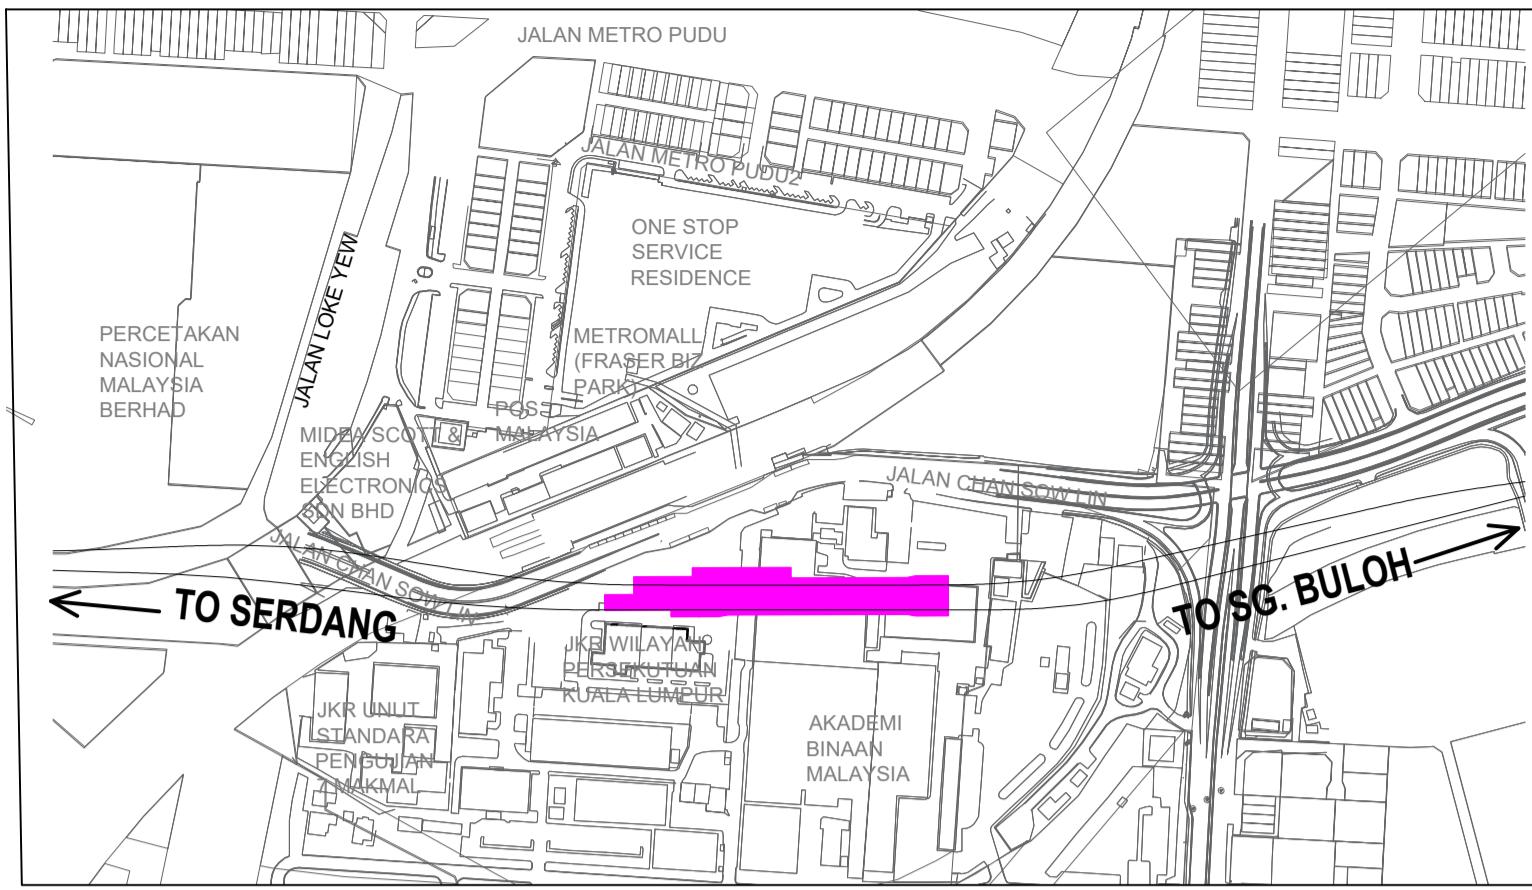


	Station, Link Bridge, Entrances
	Entrance's Facilities (Lift, Stairs, Escalator)
	Commuter's Facilities
	Covered Facilities (MEP/MSPR/Ancillary)
	Covered Walkway
	Walkway
	Landscape
	Main Road
	MRT Access Road & Road Widening
	Deferred / Omitted / Relocated

#### Changes in Chan Sow Lin

- Entrance A location to be changed.
- New paid-to-paid linkway between MRT and LRT station, linking Entrance B and new Entrance C to be built.
- New Entrance C to be built with lift and staircase, including provision for future escalators.


Key Plan (n.t.s)

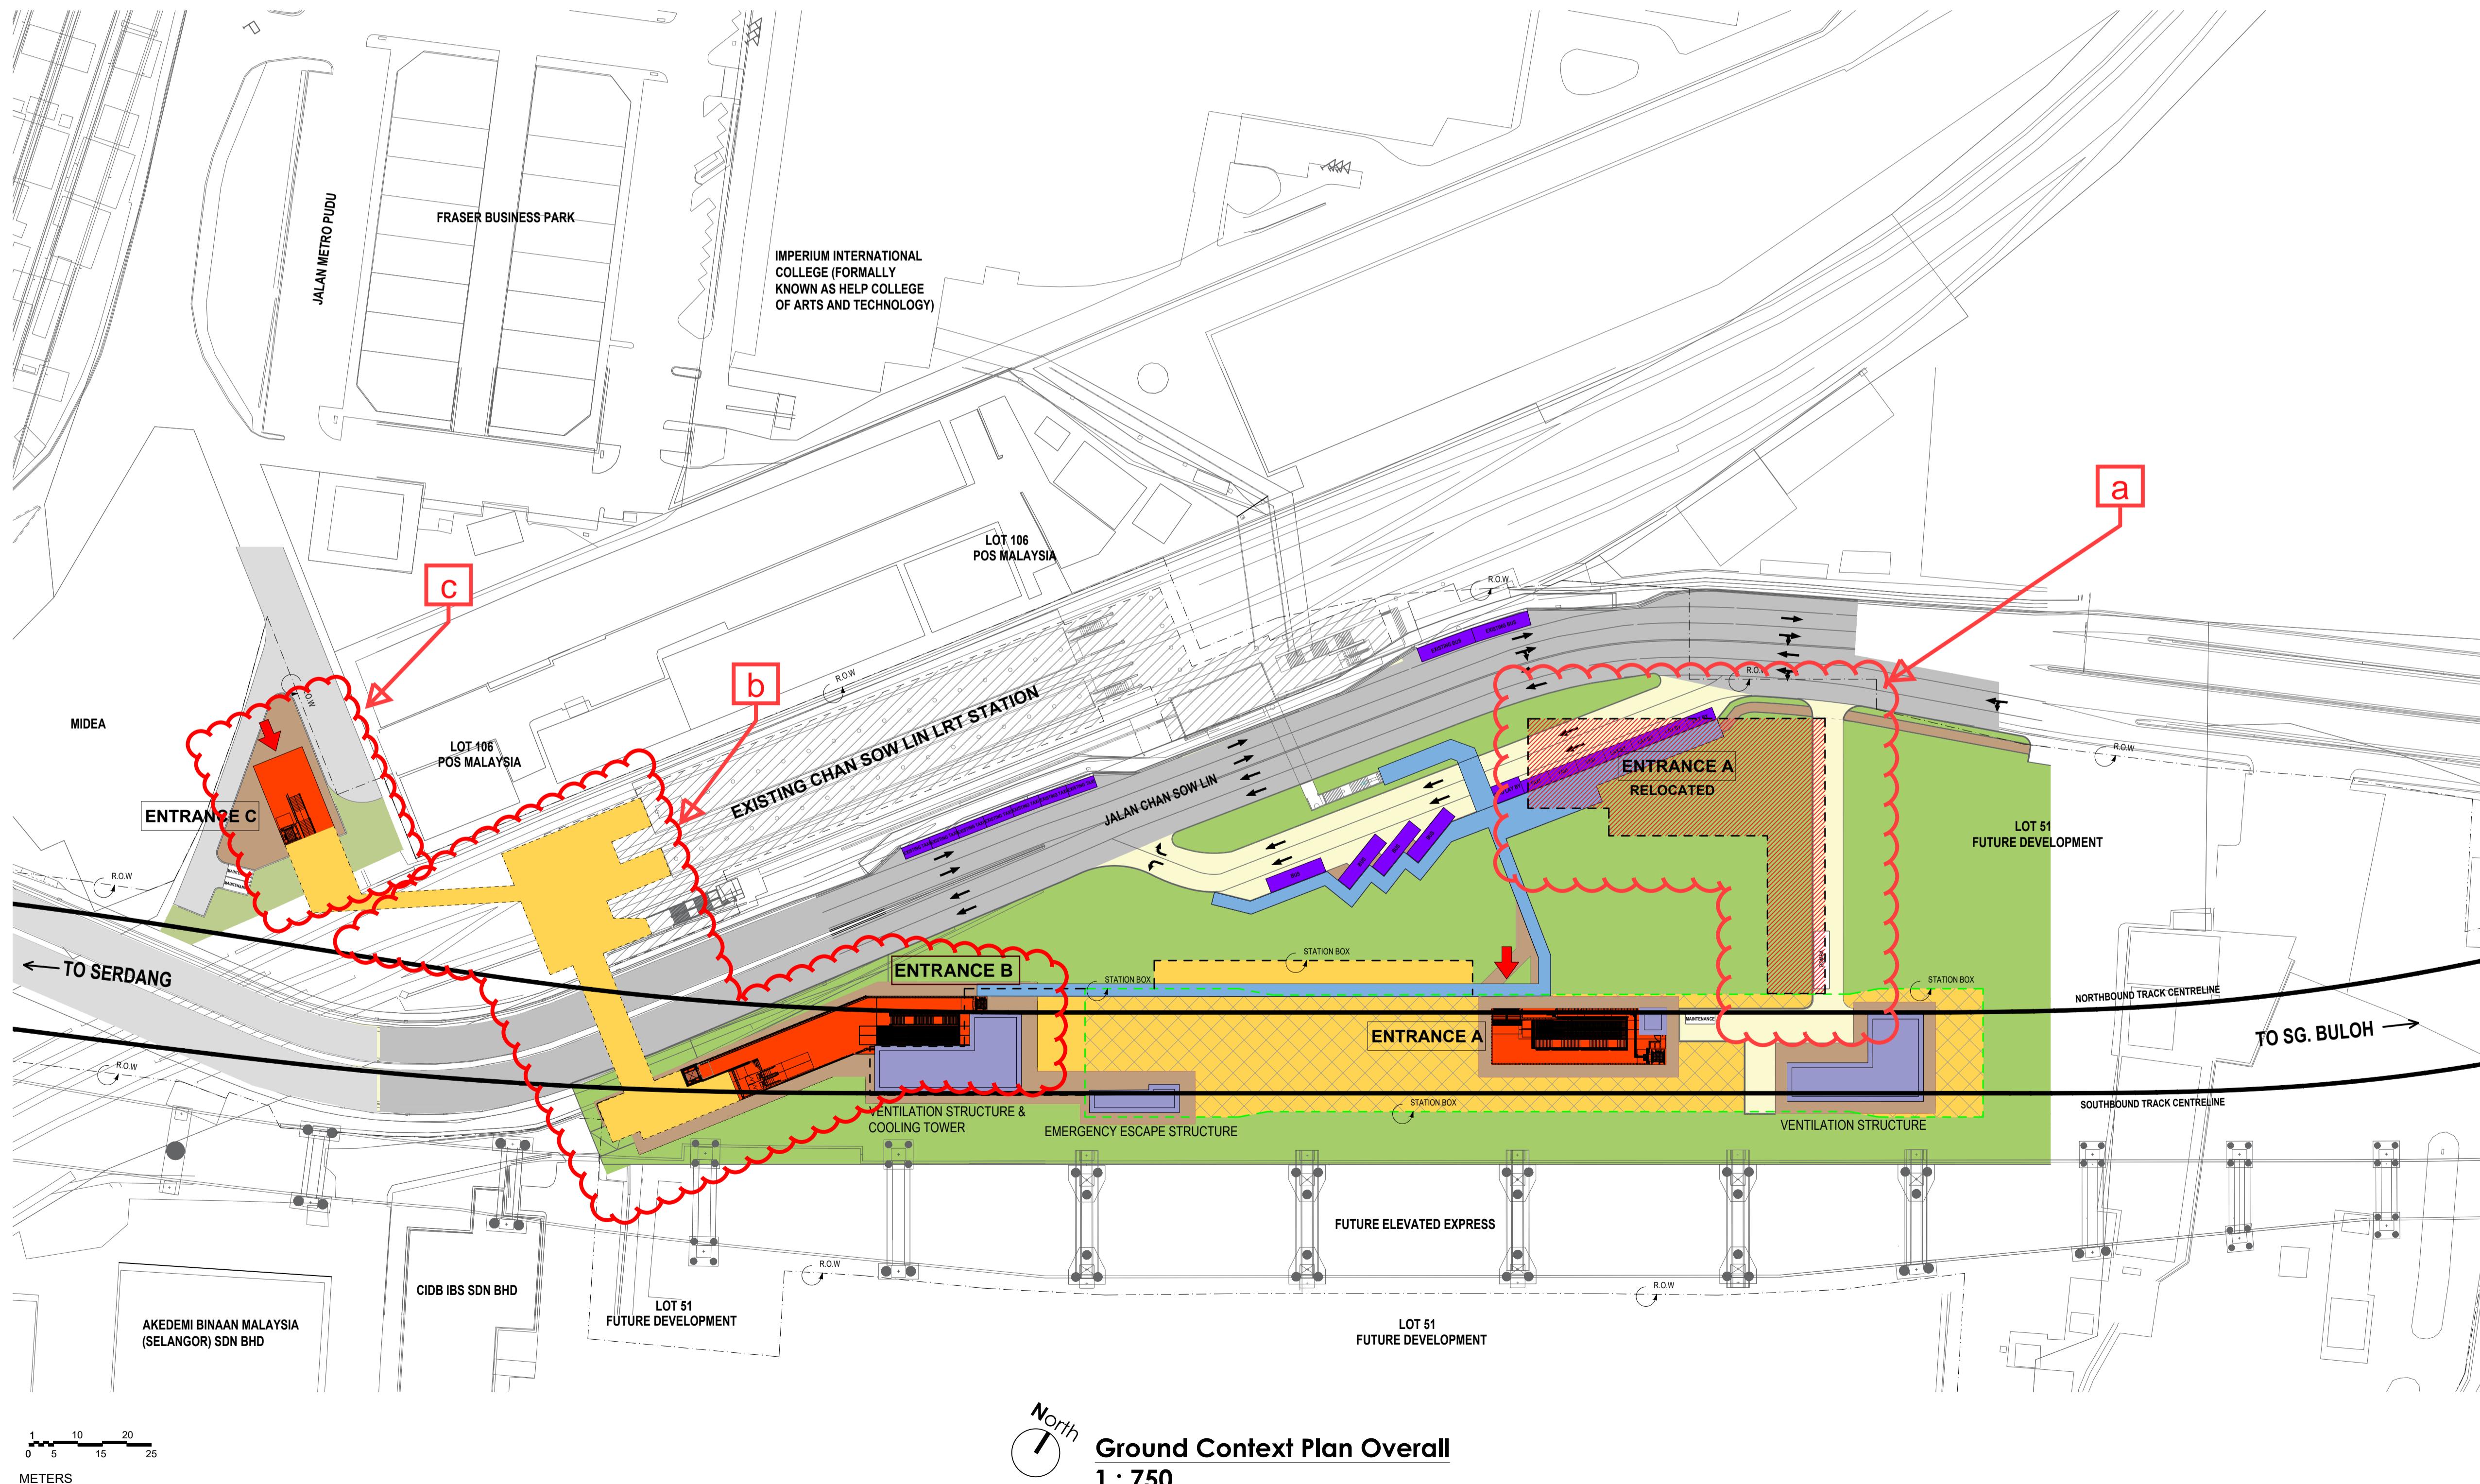

Ground Context Plan Overall  
1 : 750

Drawing Title :

S24  
CHAN SOW LIN

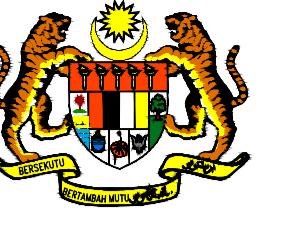

**KERAJAAN MALAYSIA**


PROJECT TITLE:  
PROJECT MASS RAPID TRANSIT LALUAN 2:  
PUTRAJAYA LINE  
(formerly known as PROJEK MRT LALUAN 2:  
SG BULOH - SERDANG - PUTRAJAYA (SSP))

PROJECT PACKAGE:  
**UNDERGROUND**

SUPERVISING AGENCY :  
**AGENSI PENGANGKUTAN AWAM DARAT (APAD)**  
LAND PUBLIC TRANSPORT AGENCY (APAD)  
**AGENSI PENGANGKUTAN AWAM DARAT (A.P.A.D.)**

ARAS G, M DAN 20, MENARA TUN ISMAIL MOHAMED ALI,  
NO. 25, JALAN RAJA LAUT,  
50470 KUALA LUMPUR.  
Tel (ARAS G): 603-2603 6700 / Tel (ARAS 20): 603-2603 6600  
Fax : 603-26036710

PROJECT OWNER :  
**MRT CORP**  
**Mass Rapid Transit Corporation Sdn Bhd**  
(902884-V)  
5th FLOOR MENARA I&P 1,  
JALAN DUNGUN, DAMANSARA HEIGHTS,  
50490 KUALA LUMPUR.

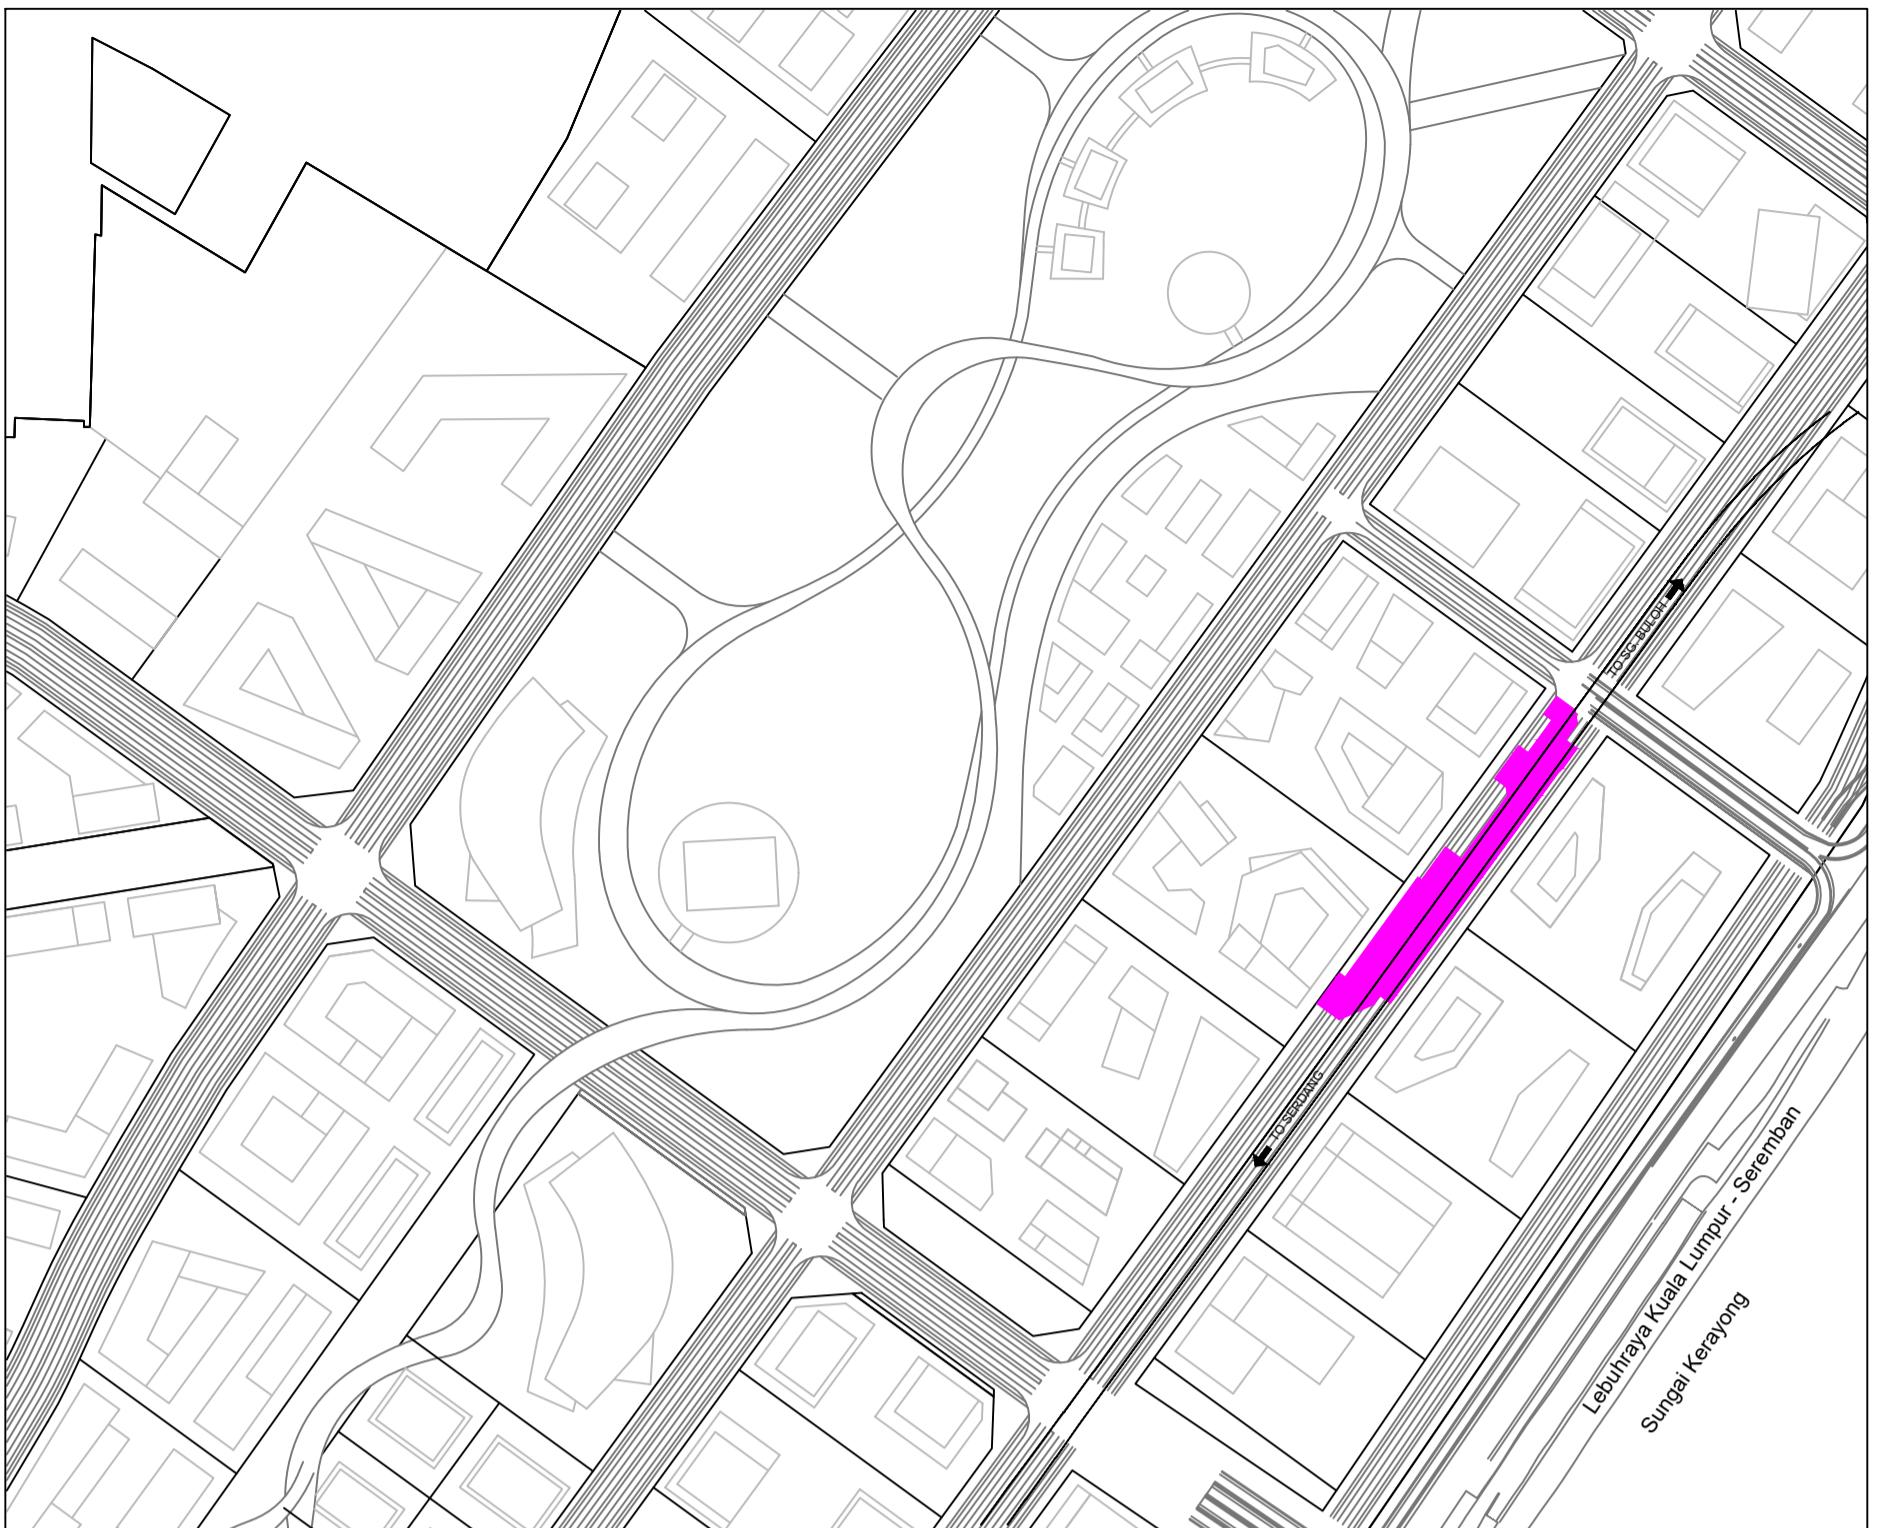


**Key Plan (n.t.s)**

<b>Station, Link Bridge, Entrances</b>
<b>Entrance's Facilities (Lift,Stairs,Escalator)</b>
<b>Commuter's Facilities</b>
<b>Covered Facilities (MEP/MSPR/Ancillary)</b>
<b>Covered Walkway</b>
<b>Walkway</b>
<b>Landscape</b>
<b>Main Road</b>
<b>MRT Access Road &amp; Road Widening</b>
<b>Structural Provision (Up To Flood Protection Level (For Future Vent Structure / Entrance</b>

**Changes in Bandar Malaysia Utara (Bandar Malaysia North)**

- a) Station name to change to Bandar Malaysia Utara.
- b) Station becomes a provisional station and to be opened in the future.

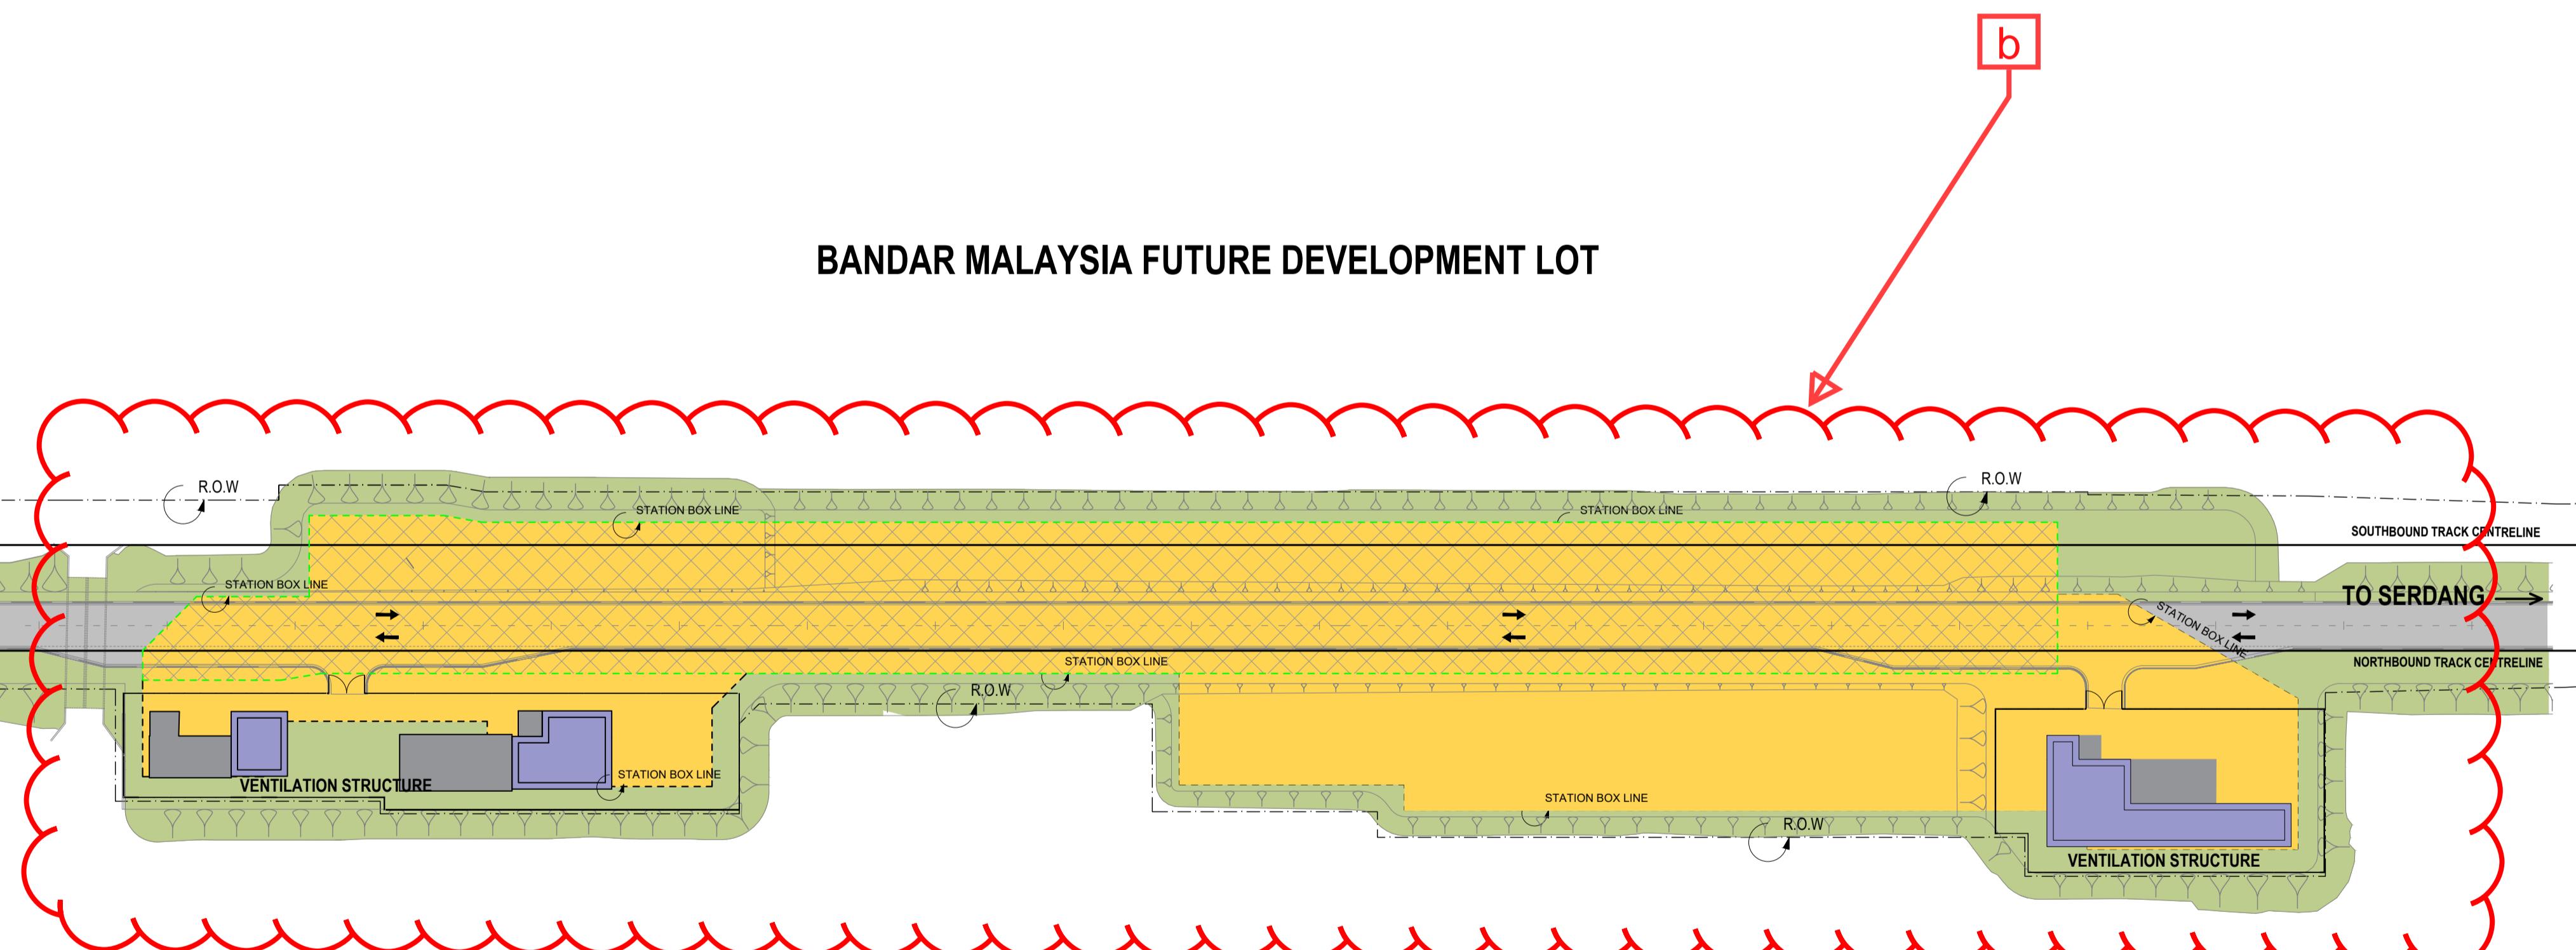

**BANDAR MALAYSIA FUTURE DEVELOPMENT LOT**

**BANDAR MALAYSIA FUTURE DEVELOPMENT LOT**



**Ground Context Plan Overall**  
1 : 750

1  
0 5 10 15 20 25  
METERS  
1:750 (A1)  
1:1500 (A3)

**S25**  
**BANDAR MALAYSIA UTARA**  
(PREVIOUSLY KNOWN AS BANDAR MALAYSIA  
NORTH)



**KERAJAAN MALAYSIA**


PROJECT TITLE:  
PROJECT MASS RAPID TRANSIT LALUAN 2:  
PUTRAJAYA LINE  
(formerly known as PROJEK MRT LALUAN 2;  
SG BULOH - SERDANG - PUTRAJAYA (SSP))

PROJECT PACKAGE:  
UNDERGROUND

SUPERVISING AGENCY :  
**AGENSI PENGANGKUTAN AWAM DARAT (APAD)**  
LAND PUBLIC TRANSPORT AGENCY (APAD)  
**AGENSI PENGANGKUTAN AWAM DARAT (A.P.A.D.)**

ARAS G, M DAN 20, MENARA TUN ISMAIL MOHAMED ALI,  
NO. 25, JALAN RAJA LAUT,  
50470 KUALA LUMPUR.  
Tel (ARAS G): 603-2603 6700 / Tel (ARAS 20): 603-2603 6600  
Fax : 603-26036710

PROJECT OWNER :  
**MRT CORP**  
Mass Rapid Transit Corporation Sdn Bhd  
(902884-V)  
5th FLOOR MENARA I&P 1,  
JALAN DUNGUN, DAMANSARA HEIGHTS,  
50490 KUALA LUMPUR.

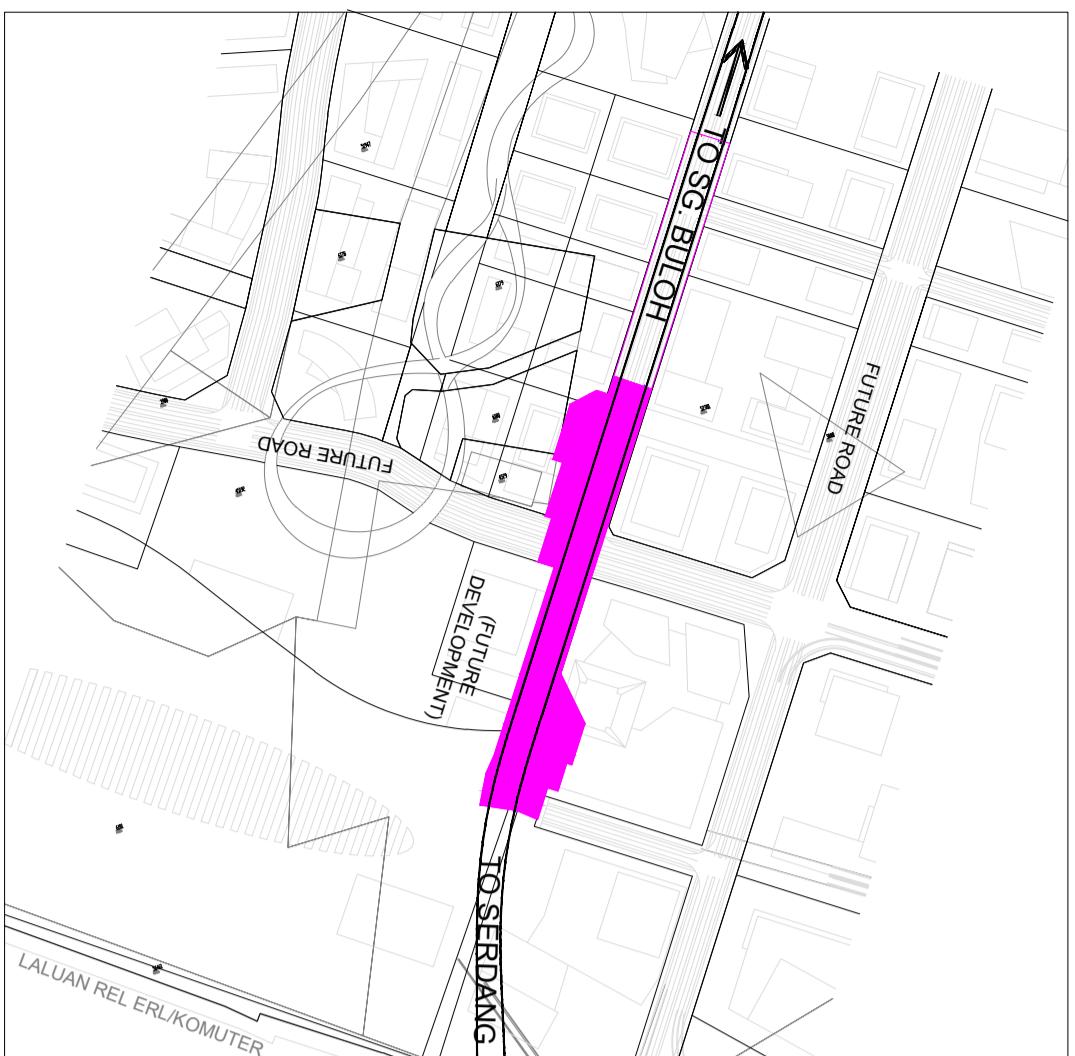


<b>Station, Link Bridge, Entrances</b>
<b>Entrance's Facilities (Lift,Stairs,Escalator)</b>
<b>Commuter's Facilities</b>
<b>Covered Facilities (MEP/MSPR/Ancillary)</b>
<b>Covered Walkway</b>
<b>Walkway</b>
<b>Landscape</b>
<b>Main Road</b>
<b>MRT Access Road &amp; Road Widening</b>
<b>Structural Provision (Up To Flood Protection Level (For Future Vent Structure / Entrance</b>

**Changes in Bandar Malaysia Selatan (Bandar Malaysia South)**  
a) Station name to change to Bandar Malaysia Selatan.  
b) Station becomes a provisional station and to be opened in the future.

North

**Key Plan (n.t.s)**

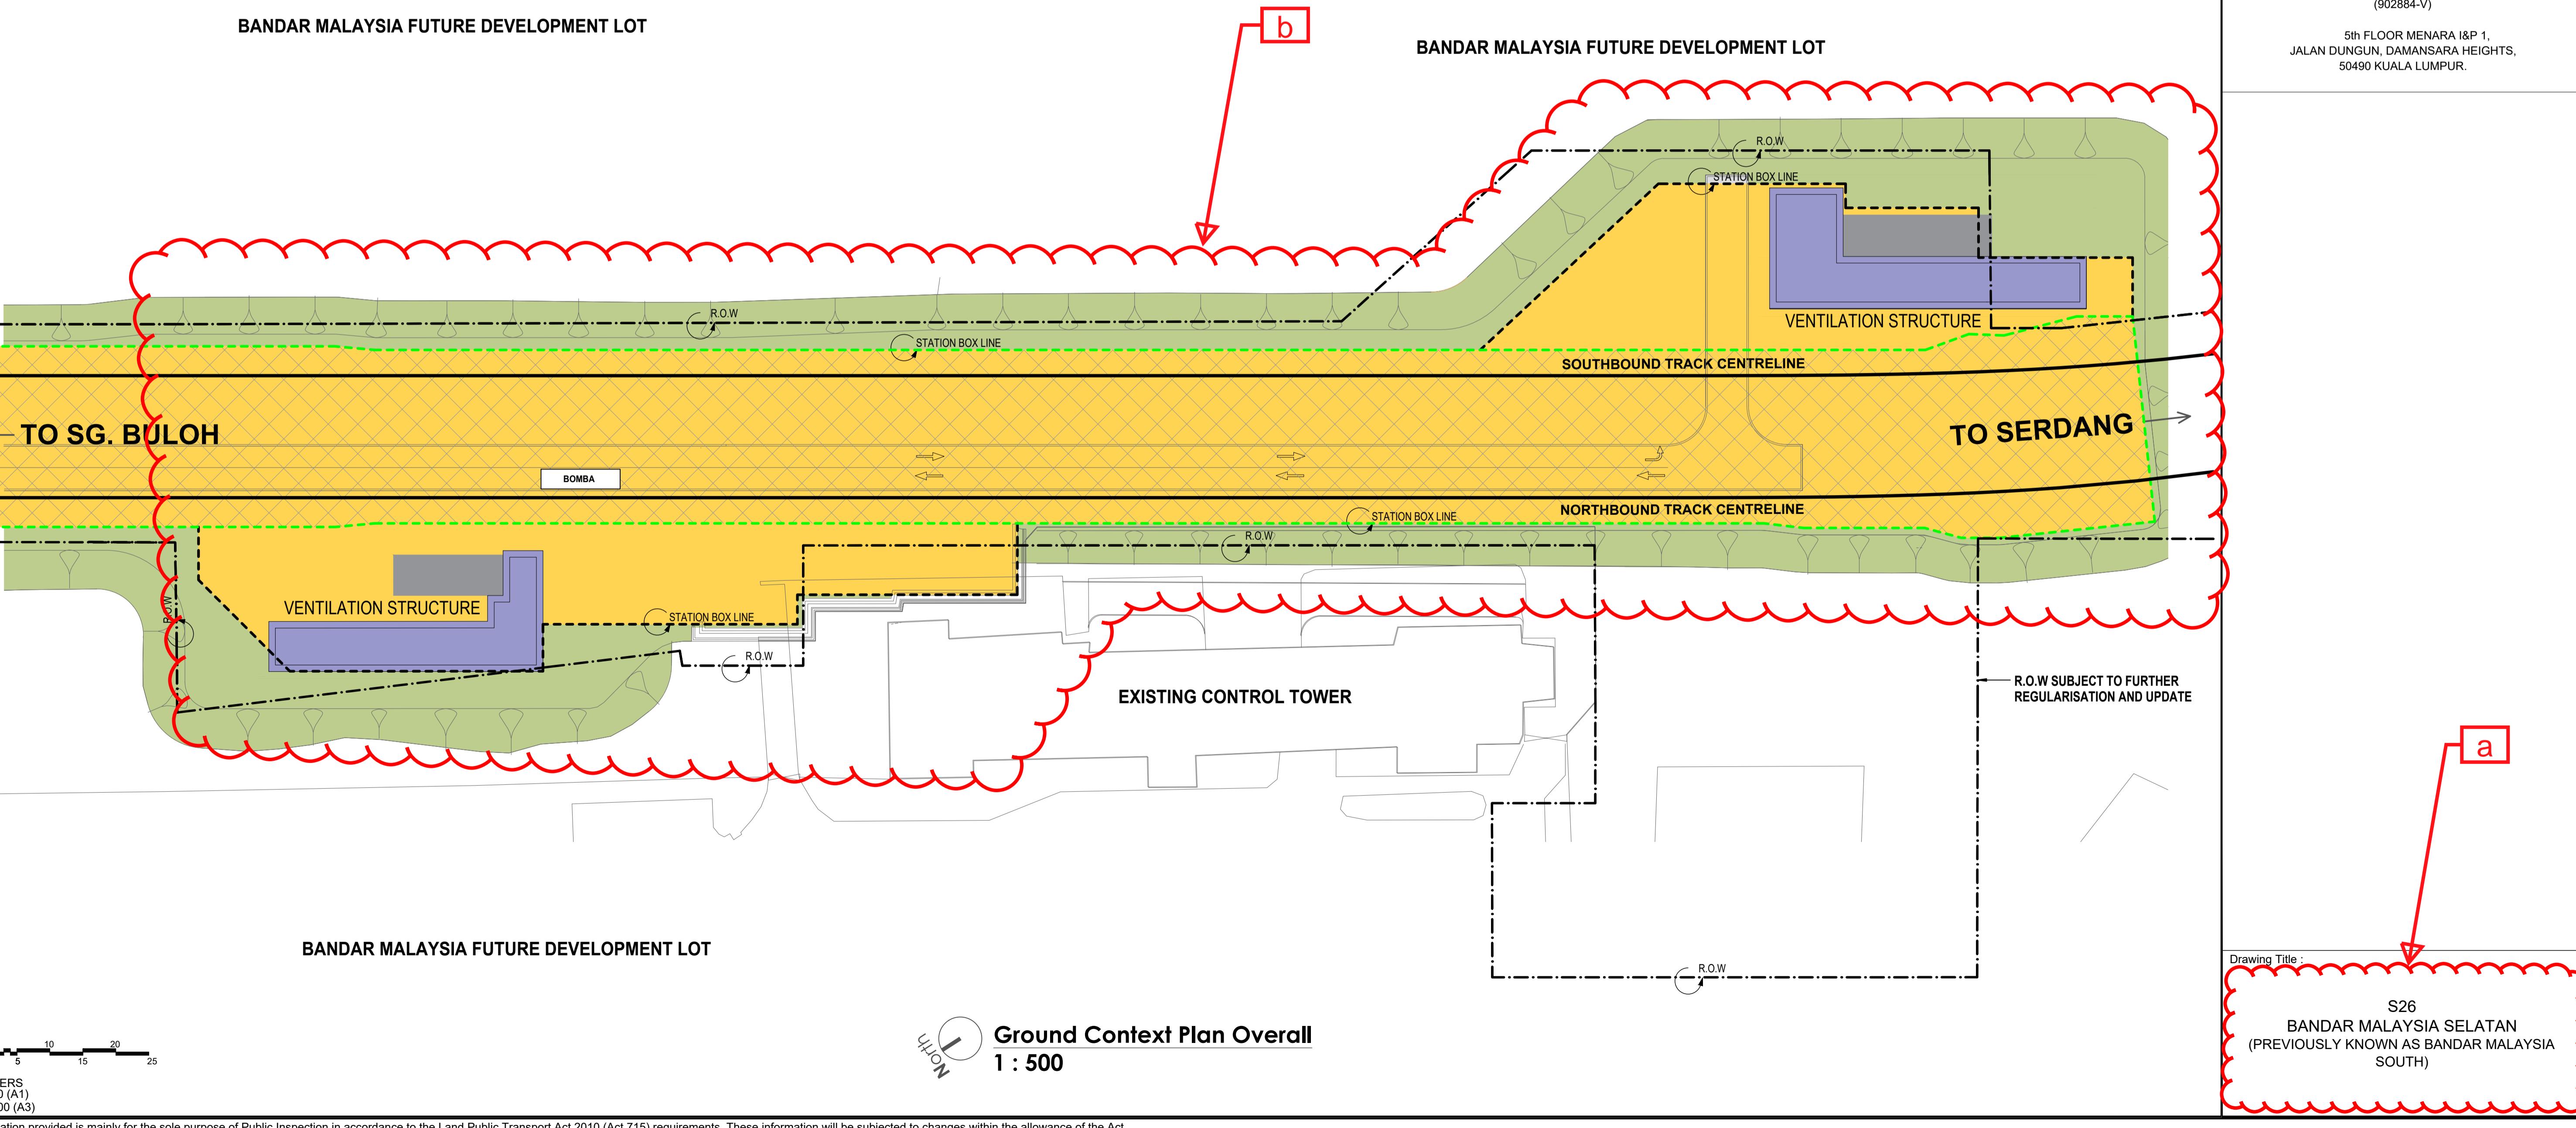

**MRT PUTRAJAYA LINE**  
**(PREVIOUSLY KNOWN AS SG BULOH – SERDANG – PUTRAJAYA)**



**KERAJAAN MALAYSIA**

**STATION CONTEXT PLAN  
(SOUTHERN)**


SUPERVISING AGENCY:



PROJECT AND ASSET OWNER:



MASS RAPID TRANSIT  
CORPORATION SDN BHD

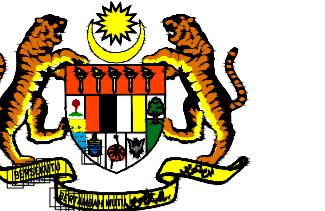

KERAJAAN MALAYSIA

PROJECT TITLE:  
PROJEK MASS RAPID TRANSIT LALUAN 2:  
PUTRAJAYA LINE  
(formerly known as PROJEK MRT LALUAN 2:  
SG BULOH - SERDANG - PUTRAJAYA (SSP))

PROJECT PACKAGE:  
ELEVATED SOUTH


SUPERVISING AGENCY :  
AGENSI PENGANGKUTAN AWAM DARAT (APAD)  
LAND PUBLIC TRANSPORT AGENCY (APAD)

AGENSI PENGANGKUTAN AWAM DARAT (APAD)

ARAS G, M DAN 20, MENARA TUN ISMAIL MOHAMED ALI,  
NO. 25, JALAN RAJA LAUT, 50350 KUALA LUMPUR,  
MALAYSIA.  
TEL (ARAS G): 603-2603 6700 / TEL (ARAS 20): 603-2603 6600

PROJECT OWNER :  
  
Mass Rapid Transit Corporation Sdn Bhd  
(902884-V)  
5th FLOOR MENARA I&P 1,  
JALAN DUNGUN, DAMANSARA HEIGHTS,  
50490 KUALA LUMPUR.


Key Plan (n.t.s)

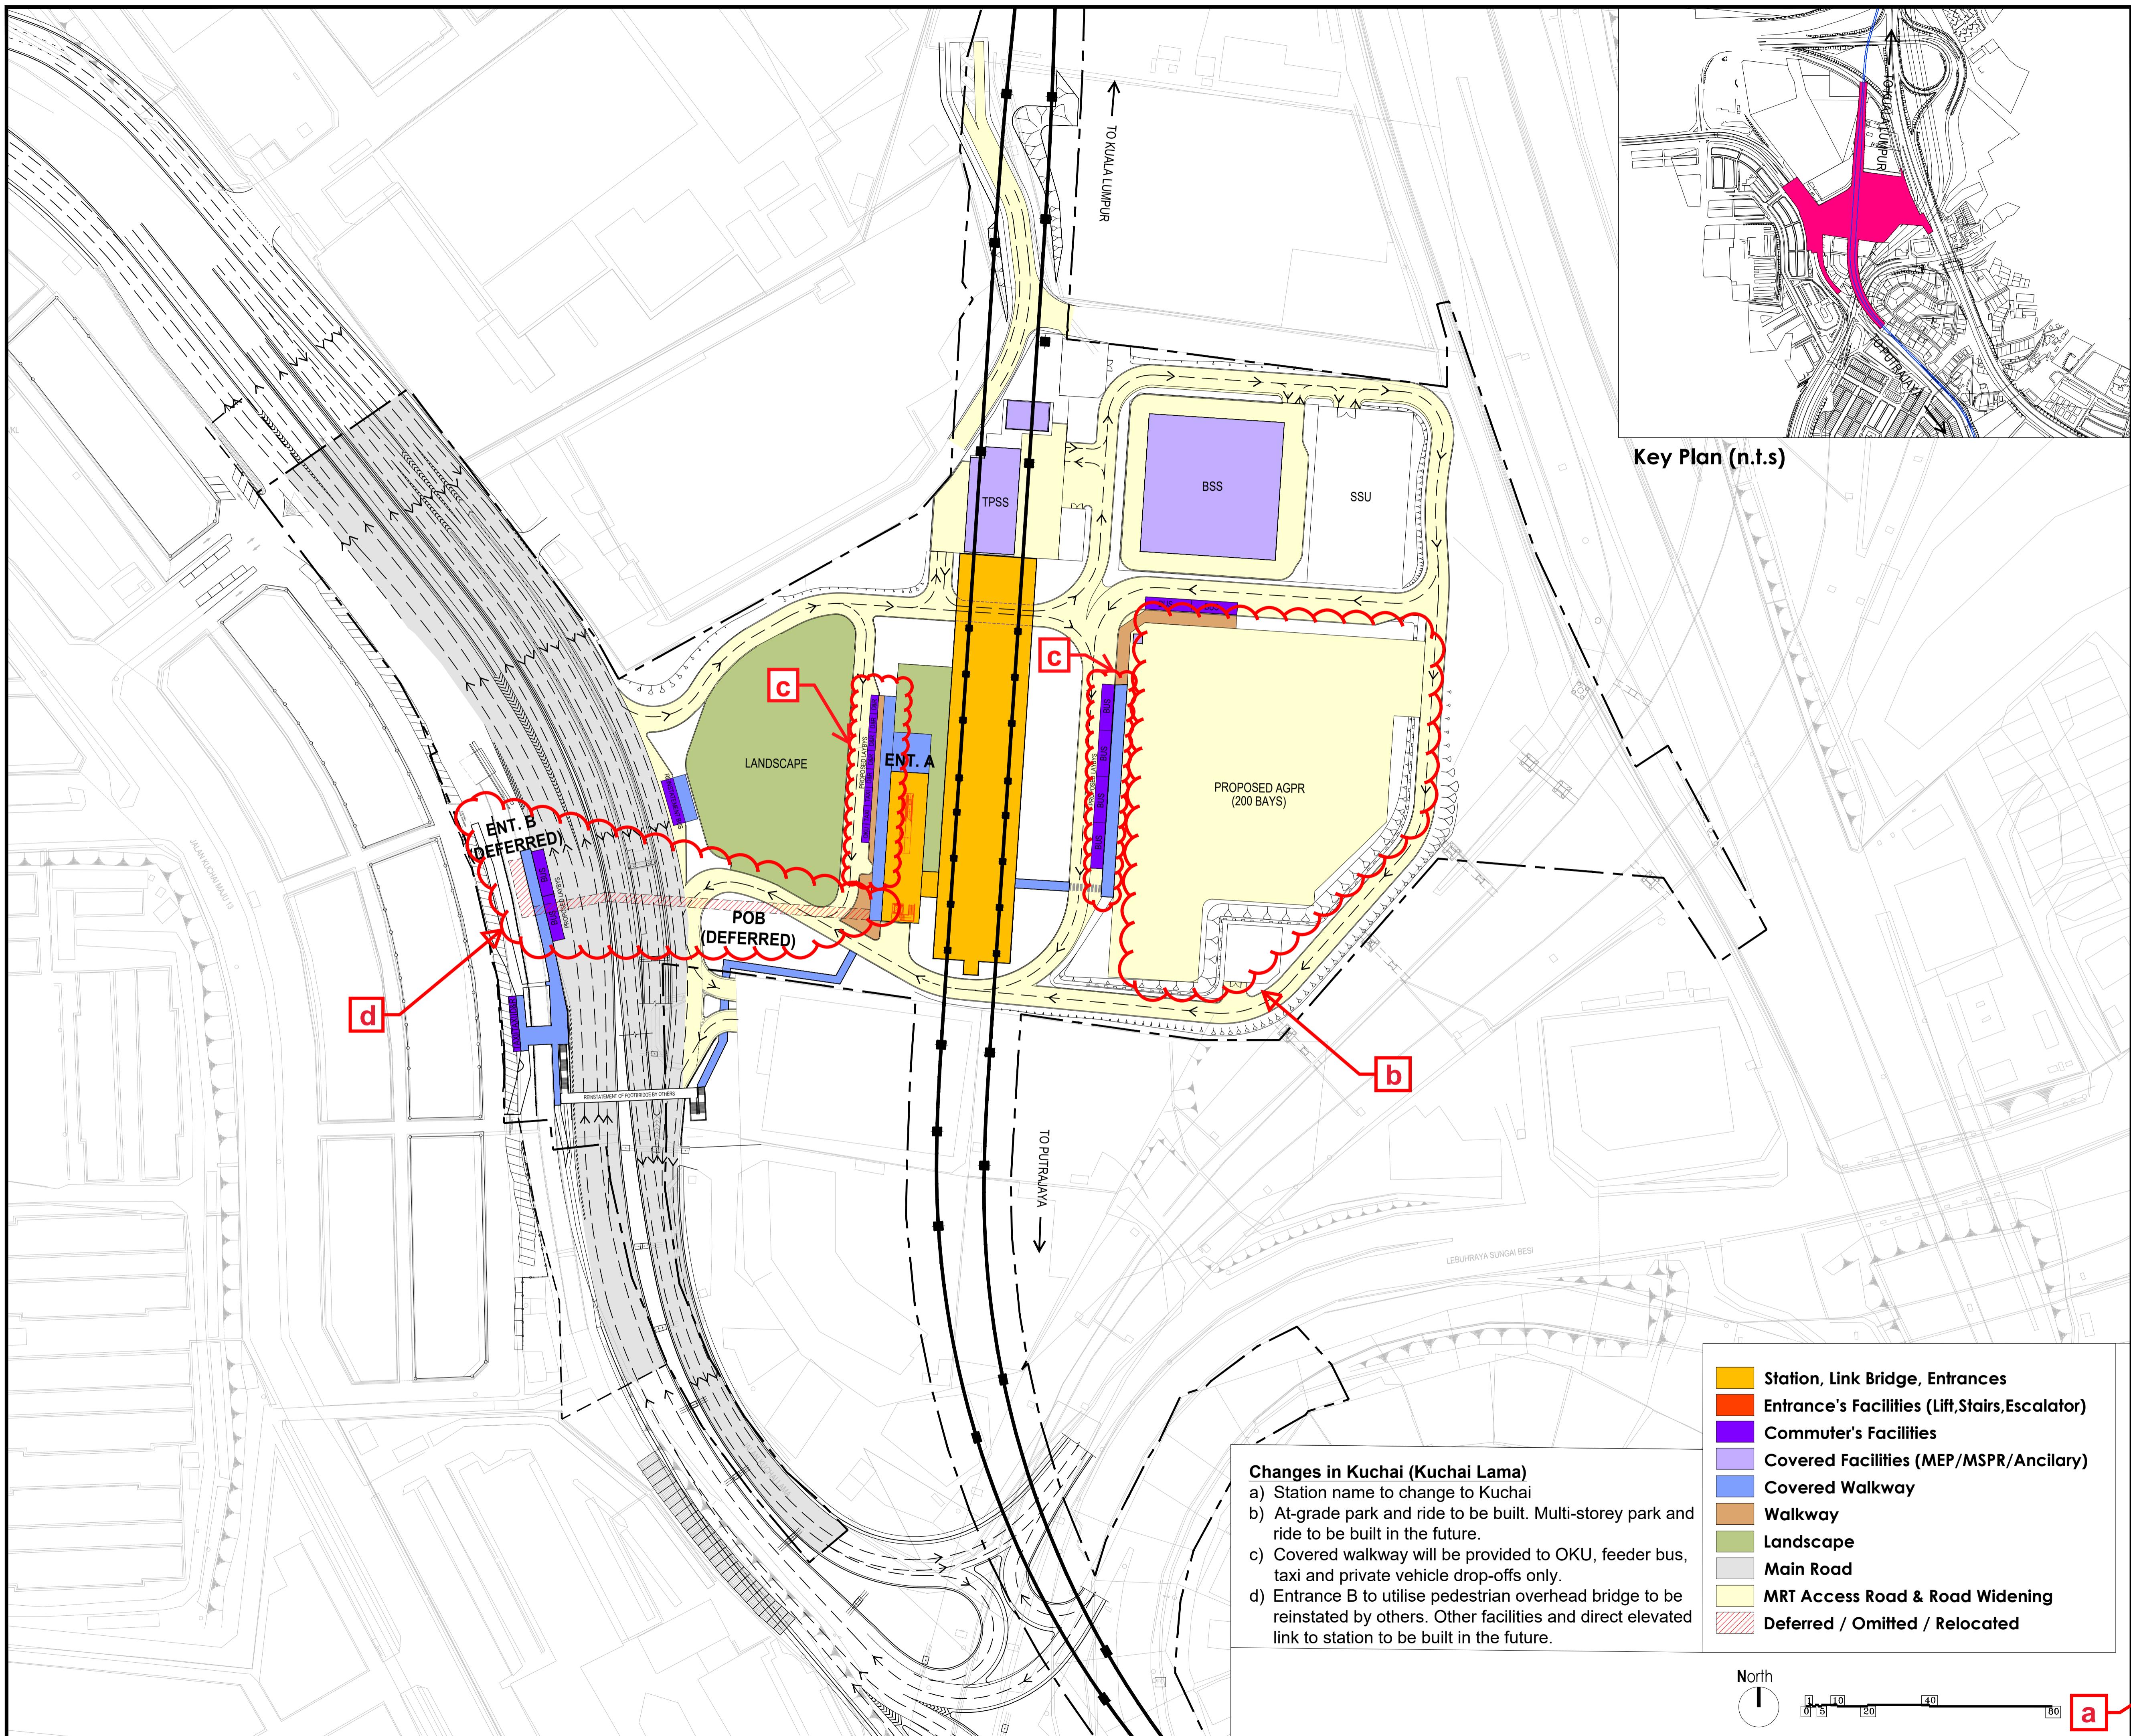

- |   |   |
|---|---|
| ■ | Station, Link Bridge, Entrances                 |
| ■ | Entrance's Facilities (Lift, Stairs, Escalator) |
| ■ | Commuter's Facilities                           |
| ■ | Covered Facilities (MEP/MSPR/Ancillary)         |
| ■ | Covered Walkway                                 |
| ■ | Walkway   |
| ■ | Landscape                                       |
| ■ | Main Road                                       |
| ■ | MRT Access Road & Road Widening                 |
| ■ | Deferred / Omitted / Relocated                  |



Drawing Title :  
S27  
KUCHAI  
(PREVIOUSLY KNOWN AS  
KUCHAI LAMA)

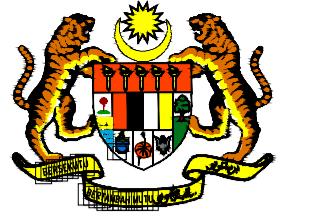

KERAJAAN MALAYSIA

PROJECT TITLE:  
PROJEK MASS RAPID TRANSIT LALUAN 2:  
PUTRAJAYA LINE  
(formerly known as PROJEK MRT LALUAN 2:  
SG BULOH - SERDANG - PUTRAJAYA(SSP))


PROJECT PACKAGE:  
ELEVATED SOUTH


SUPERVISING AGENCY :  
**AGENSI PENGANGKUTAN AWAM DARAT (APAD)**  
LAND PUBLIC TRANSPORT AGENCY (APAD)

AGENSI PENGANGKUTAN AWAM DARAT (APAD)

ARAS G, M DAN 20, MENARA TUN ISMAIL MOHAMED ALI,  
NO. 25, JALAN RAJA LAUT, 50350 KUALA LUMPUR,  
MALAYSIA.  
TEL (ARAS G): 603-2603 6700 / TEL (ARAS 20): 603-2603 6600

PROJECT OWNER :  
**MRT CORP**  
Mass Rapid Transit Corporation Sdn Bhd  
(902884-V)  
5th FLOOR MENARA I&P 1,  
JALAN DUNGUN, DAMANSARA HEIGHTS,  
50490 KUALA LUMPUR.

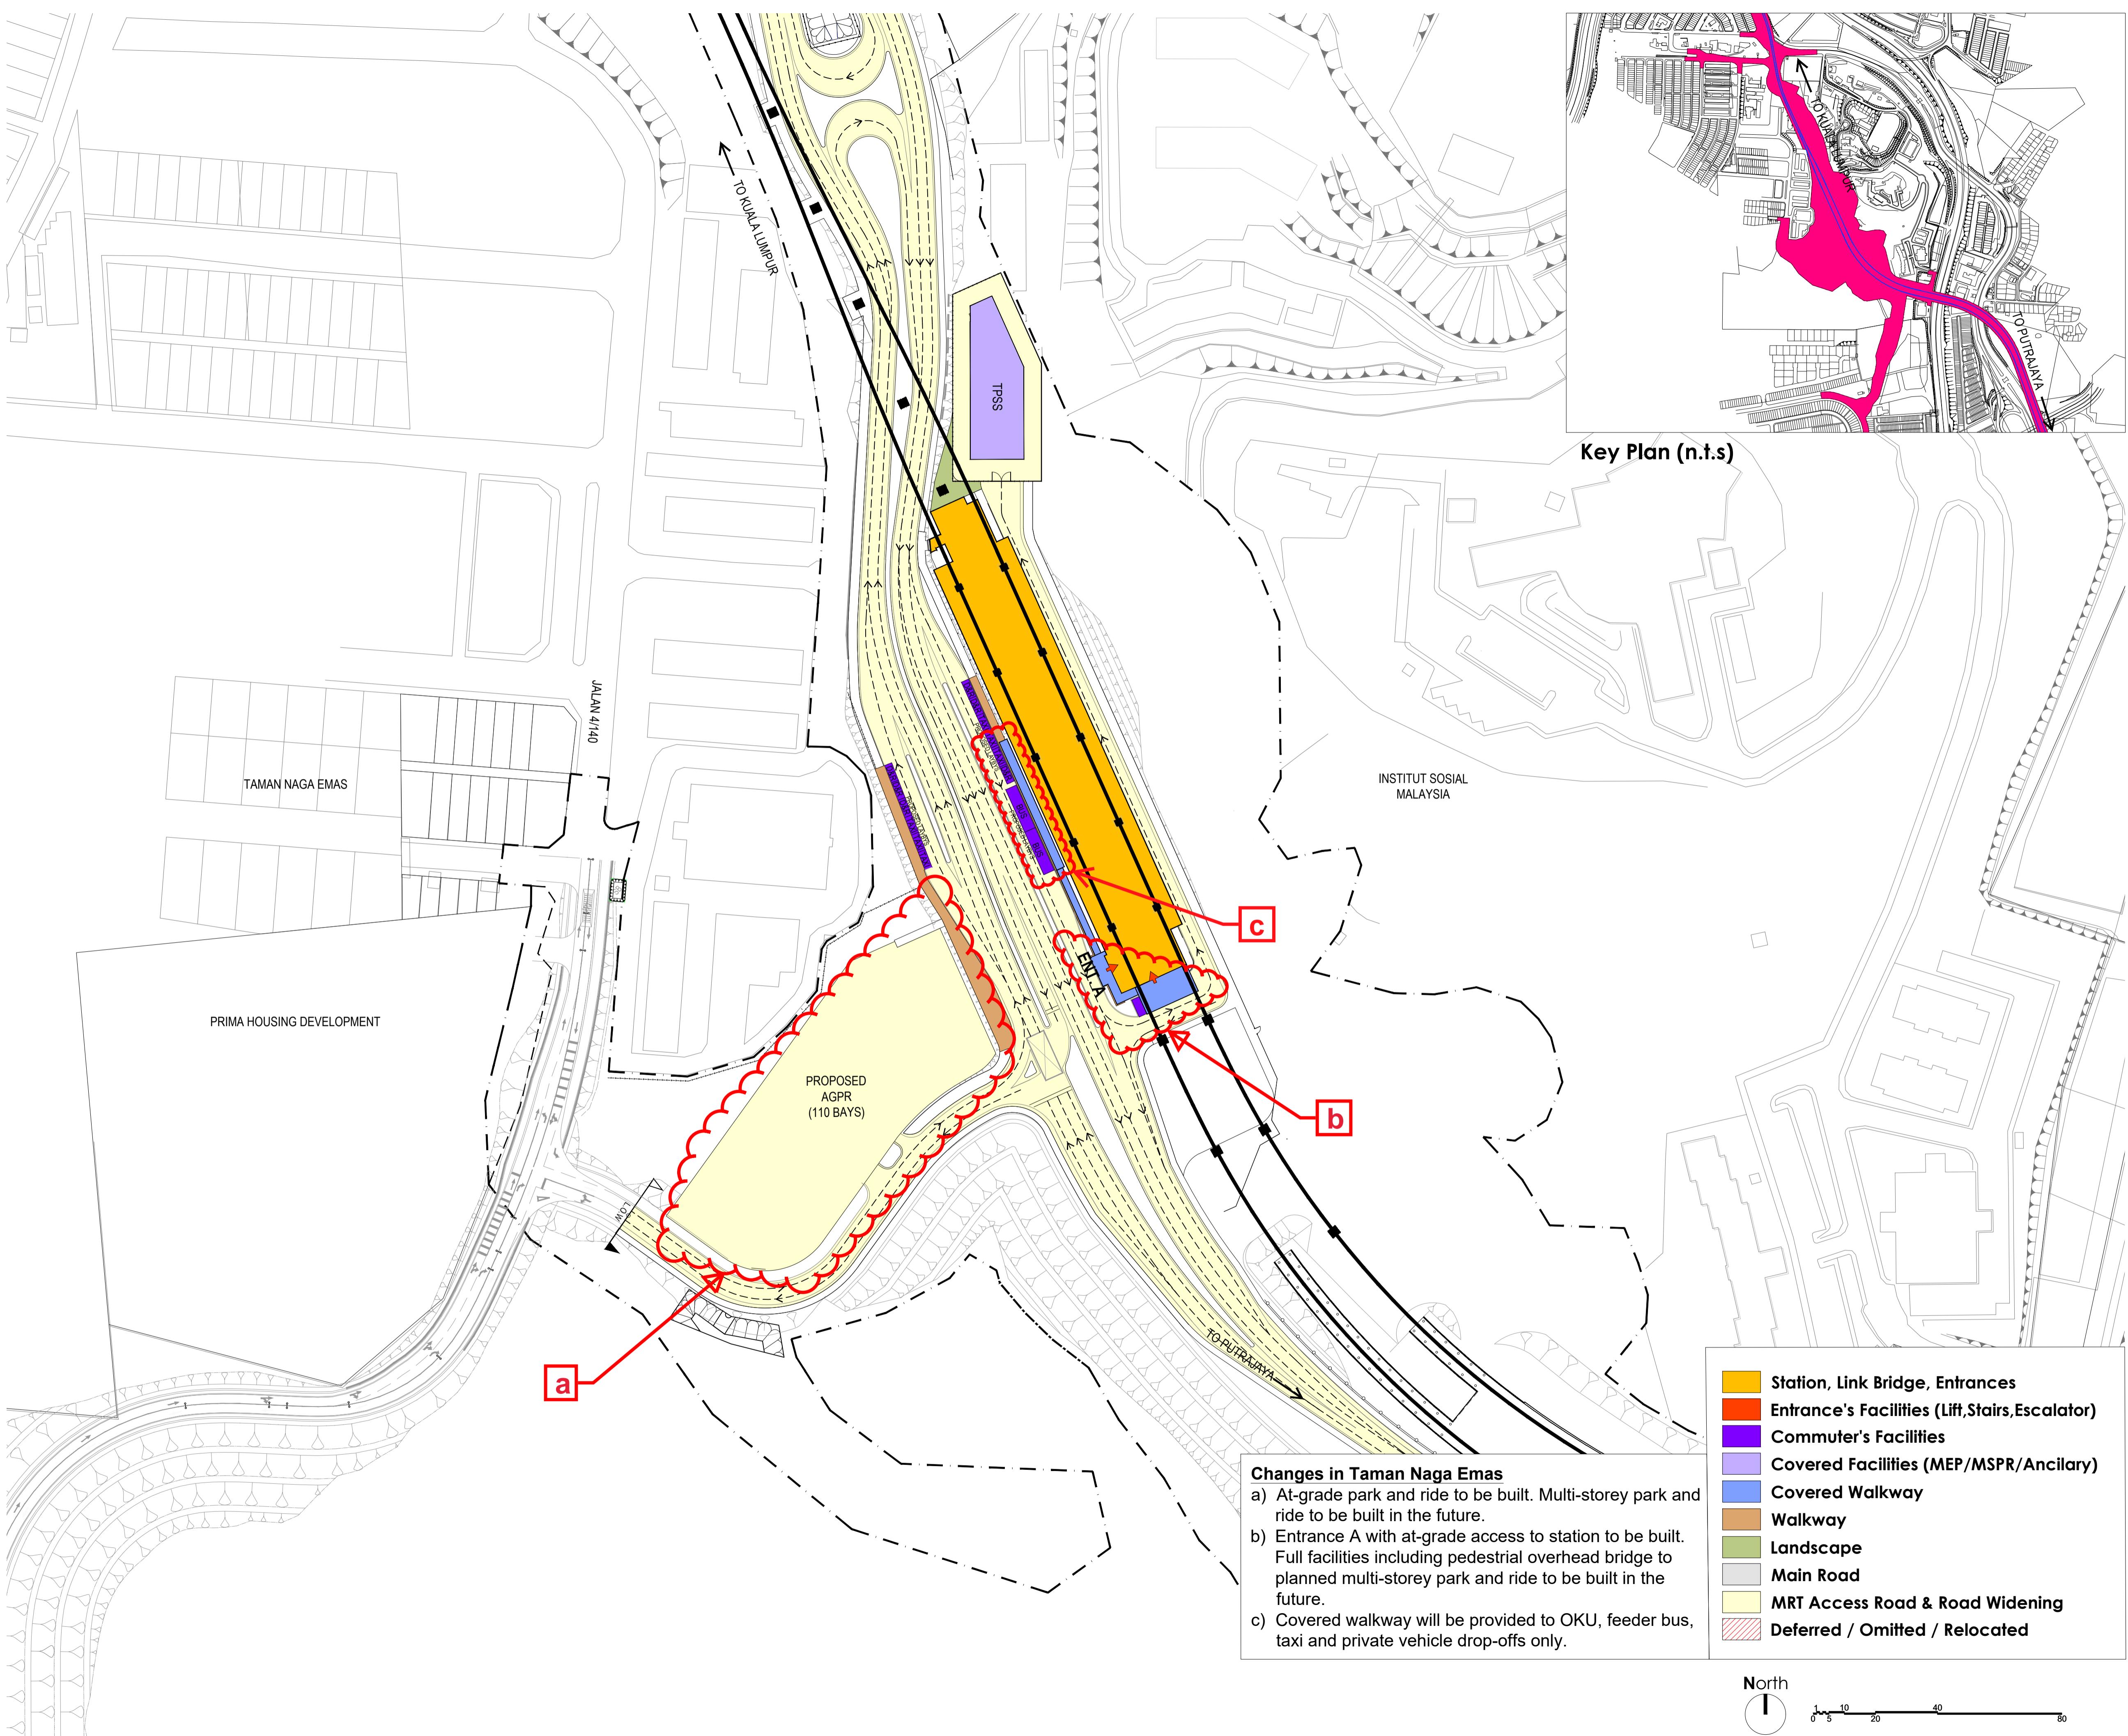

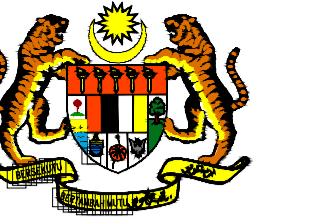

KERAJAAN MALAYSIA

PROJECT TITLE:  
PROJEK MASS RAPID TRANSIT LALUAN 2:  
PUTRAJAYA LINE  
(formerly known as PROJEK MRT LALUAN 2:  
SG BULOH - SERDANG - PUTRAJAYA (SSP))

PROJECT PACKAGE:  
ELEVATED SOUTH



SUPERVISING AGENCY :  
 AGENSI PENGANGKUTAN AWAM DARAT (APAD)  
LAND PUBLIC TRANSPORT AGENCY (APAD)

AGENSI PENGANGKUTAN AWAM DARAT  
(A.P.A.D.)


ARAS G, M DAN 20, MENARA TUN ISMAIL MOHAMED ALI,  
NO. 25, JALAN RAJA LAUT, 50350 KUALA LUMPUR,  
MALAYSIA.  
TEL (ARAS G): 603-2603 6700 / TEL (ARAS 20): 603-2603 6600

PROJECT OWNER :  
 MRT CORP  
Mass Rapid Transit Corporation Sdn Bhd  
(902884-V)  
5th FLOOR MENARA I&P 1,  
JALAN DUNGUN, DAMANSARA HEIGHTS,  
50490 KUALA LUMPUR.

Key Plan (n.t.s)

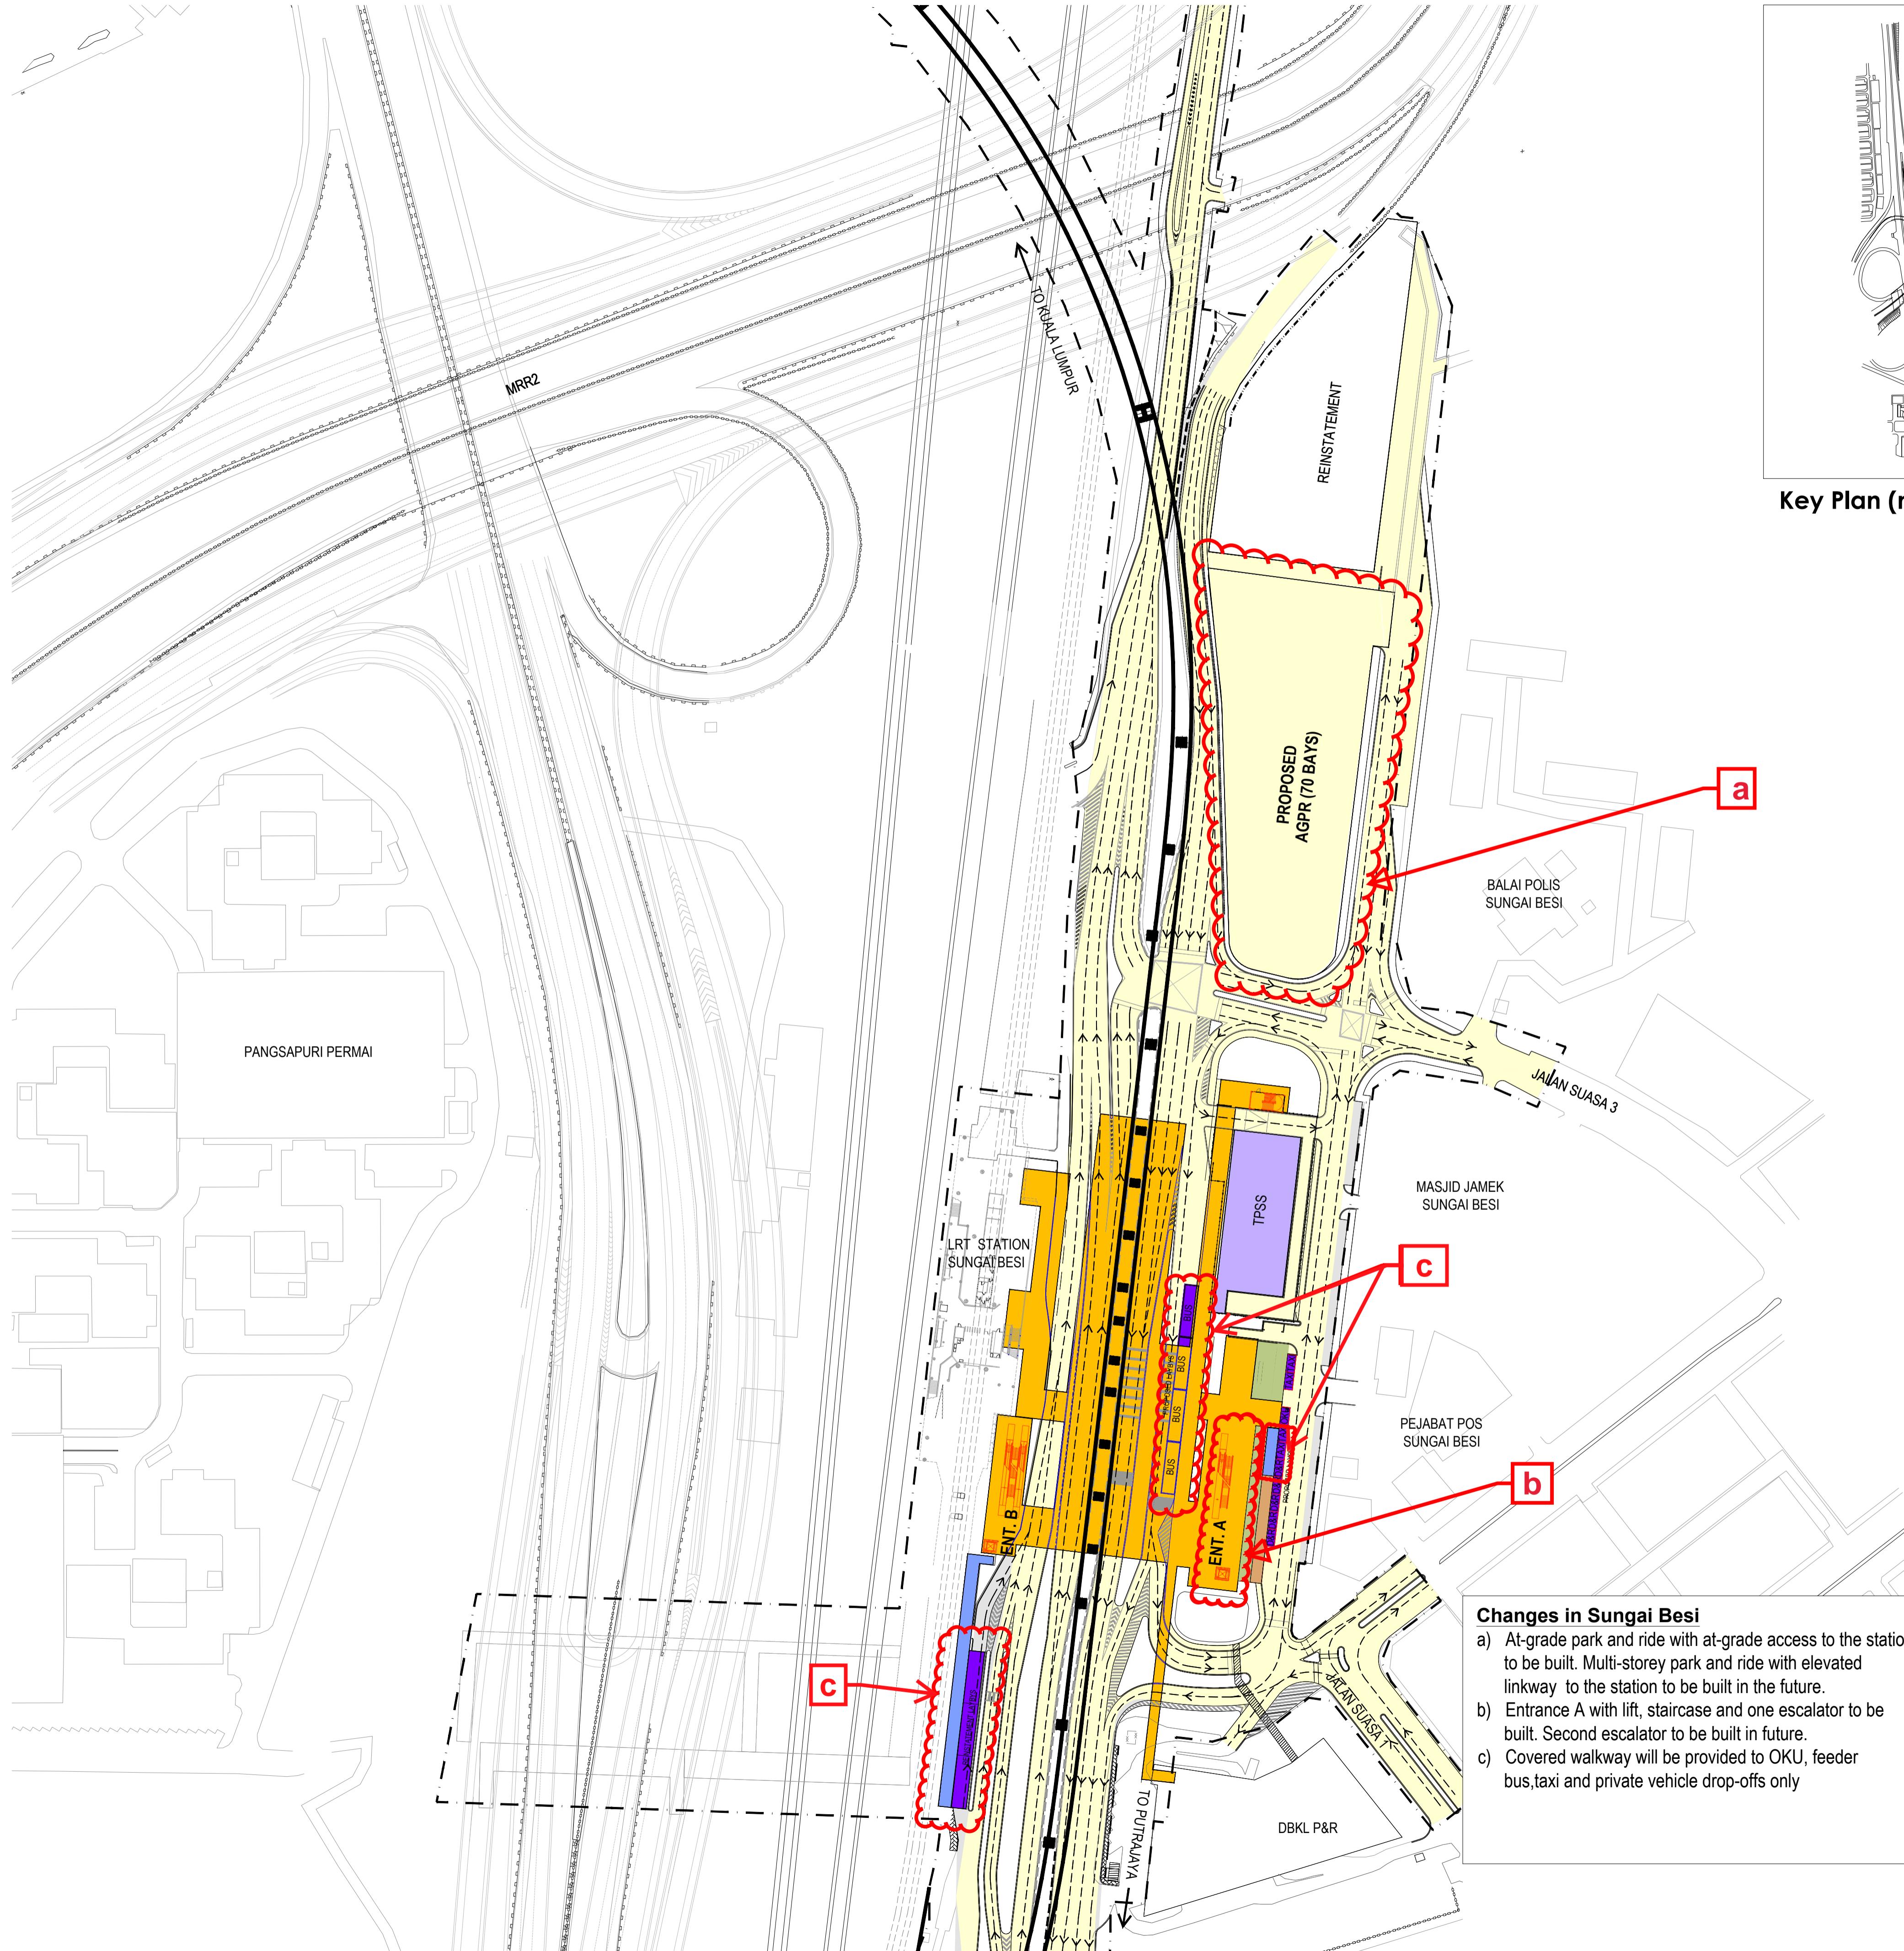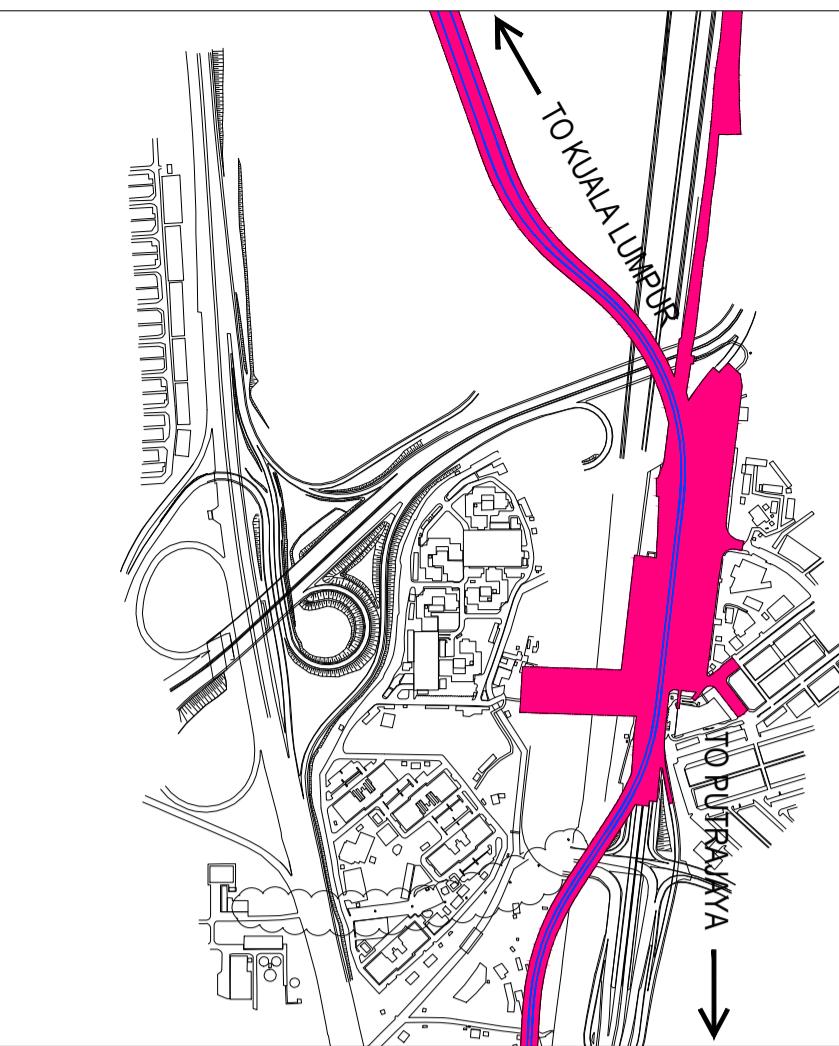


- |   |
|---|
| Station, Link Bridge, Entrances                 |
| Entrance's Facilities (Lift, Stairs, Escalator) |
| Commuter's Facilities                           |
| Covered Facilities (MEP/MSPR/Ancillary)         |
| Covered Walkway                                 |
| Walkway   |
| Landscape                                       |
| Main Road                                       |
| MRT Access Road & Road Widening                 |
| Deferred / Omitted / Relocated                  |

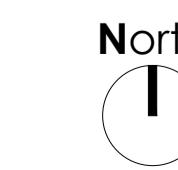

Drawing Title :

S29  
SUNGAI BESI

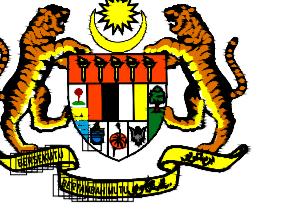

KERAJAAN MALAYSIA

PROJECT TITLE:  
PROJEK MASS RAPID TRANSIT LALUAN 2:  
PUTRAJAYA LINE  
(formerly known as PROJEK MRT LALUAN 2:  
SG BULOH - SERDANG - PUTRAJAYA(SSP))


PROJECT PACKAGE:  
ELEVATED SOUTH

SUPERVISING AGENCY :  
**AGENSI PENGANGKUTAN AWAM DARAT (APAD)**  
LAND PUBLIC TRANSPORT AGENCY (APAD)


**AGENSI PENGANGKUTAN AWAM DARAT (A.P.A.D.)**

ARAS G, M DAN 20, MENARA TUN ISMAIL MOHAMED ALI,  
NO. 25, JALAN RAJA LAUT, 50350 KUALA LUMPUR,  
MALAYSIA.  
TEL (ARAS G): 603-2603 6700 / TEL (ARAS 20): 603-2603 6600

PROJECT OWNER :  
**MRT CORP**  
Mass Rapid Transit Corporation Sdn Bhd  
(902884-V)  
5th FLOOR MENARA I&P 1,  
JALAN DUNGUN, DAMANSARA HEIGHTS,  
50490 KUALA LUMPUR.

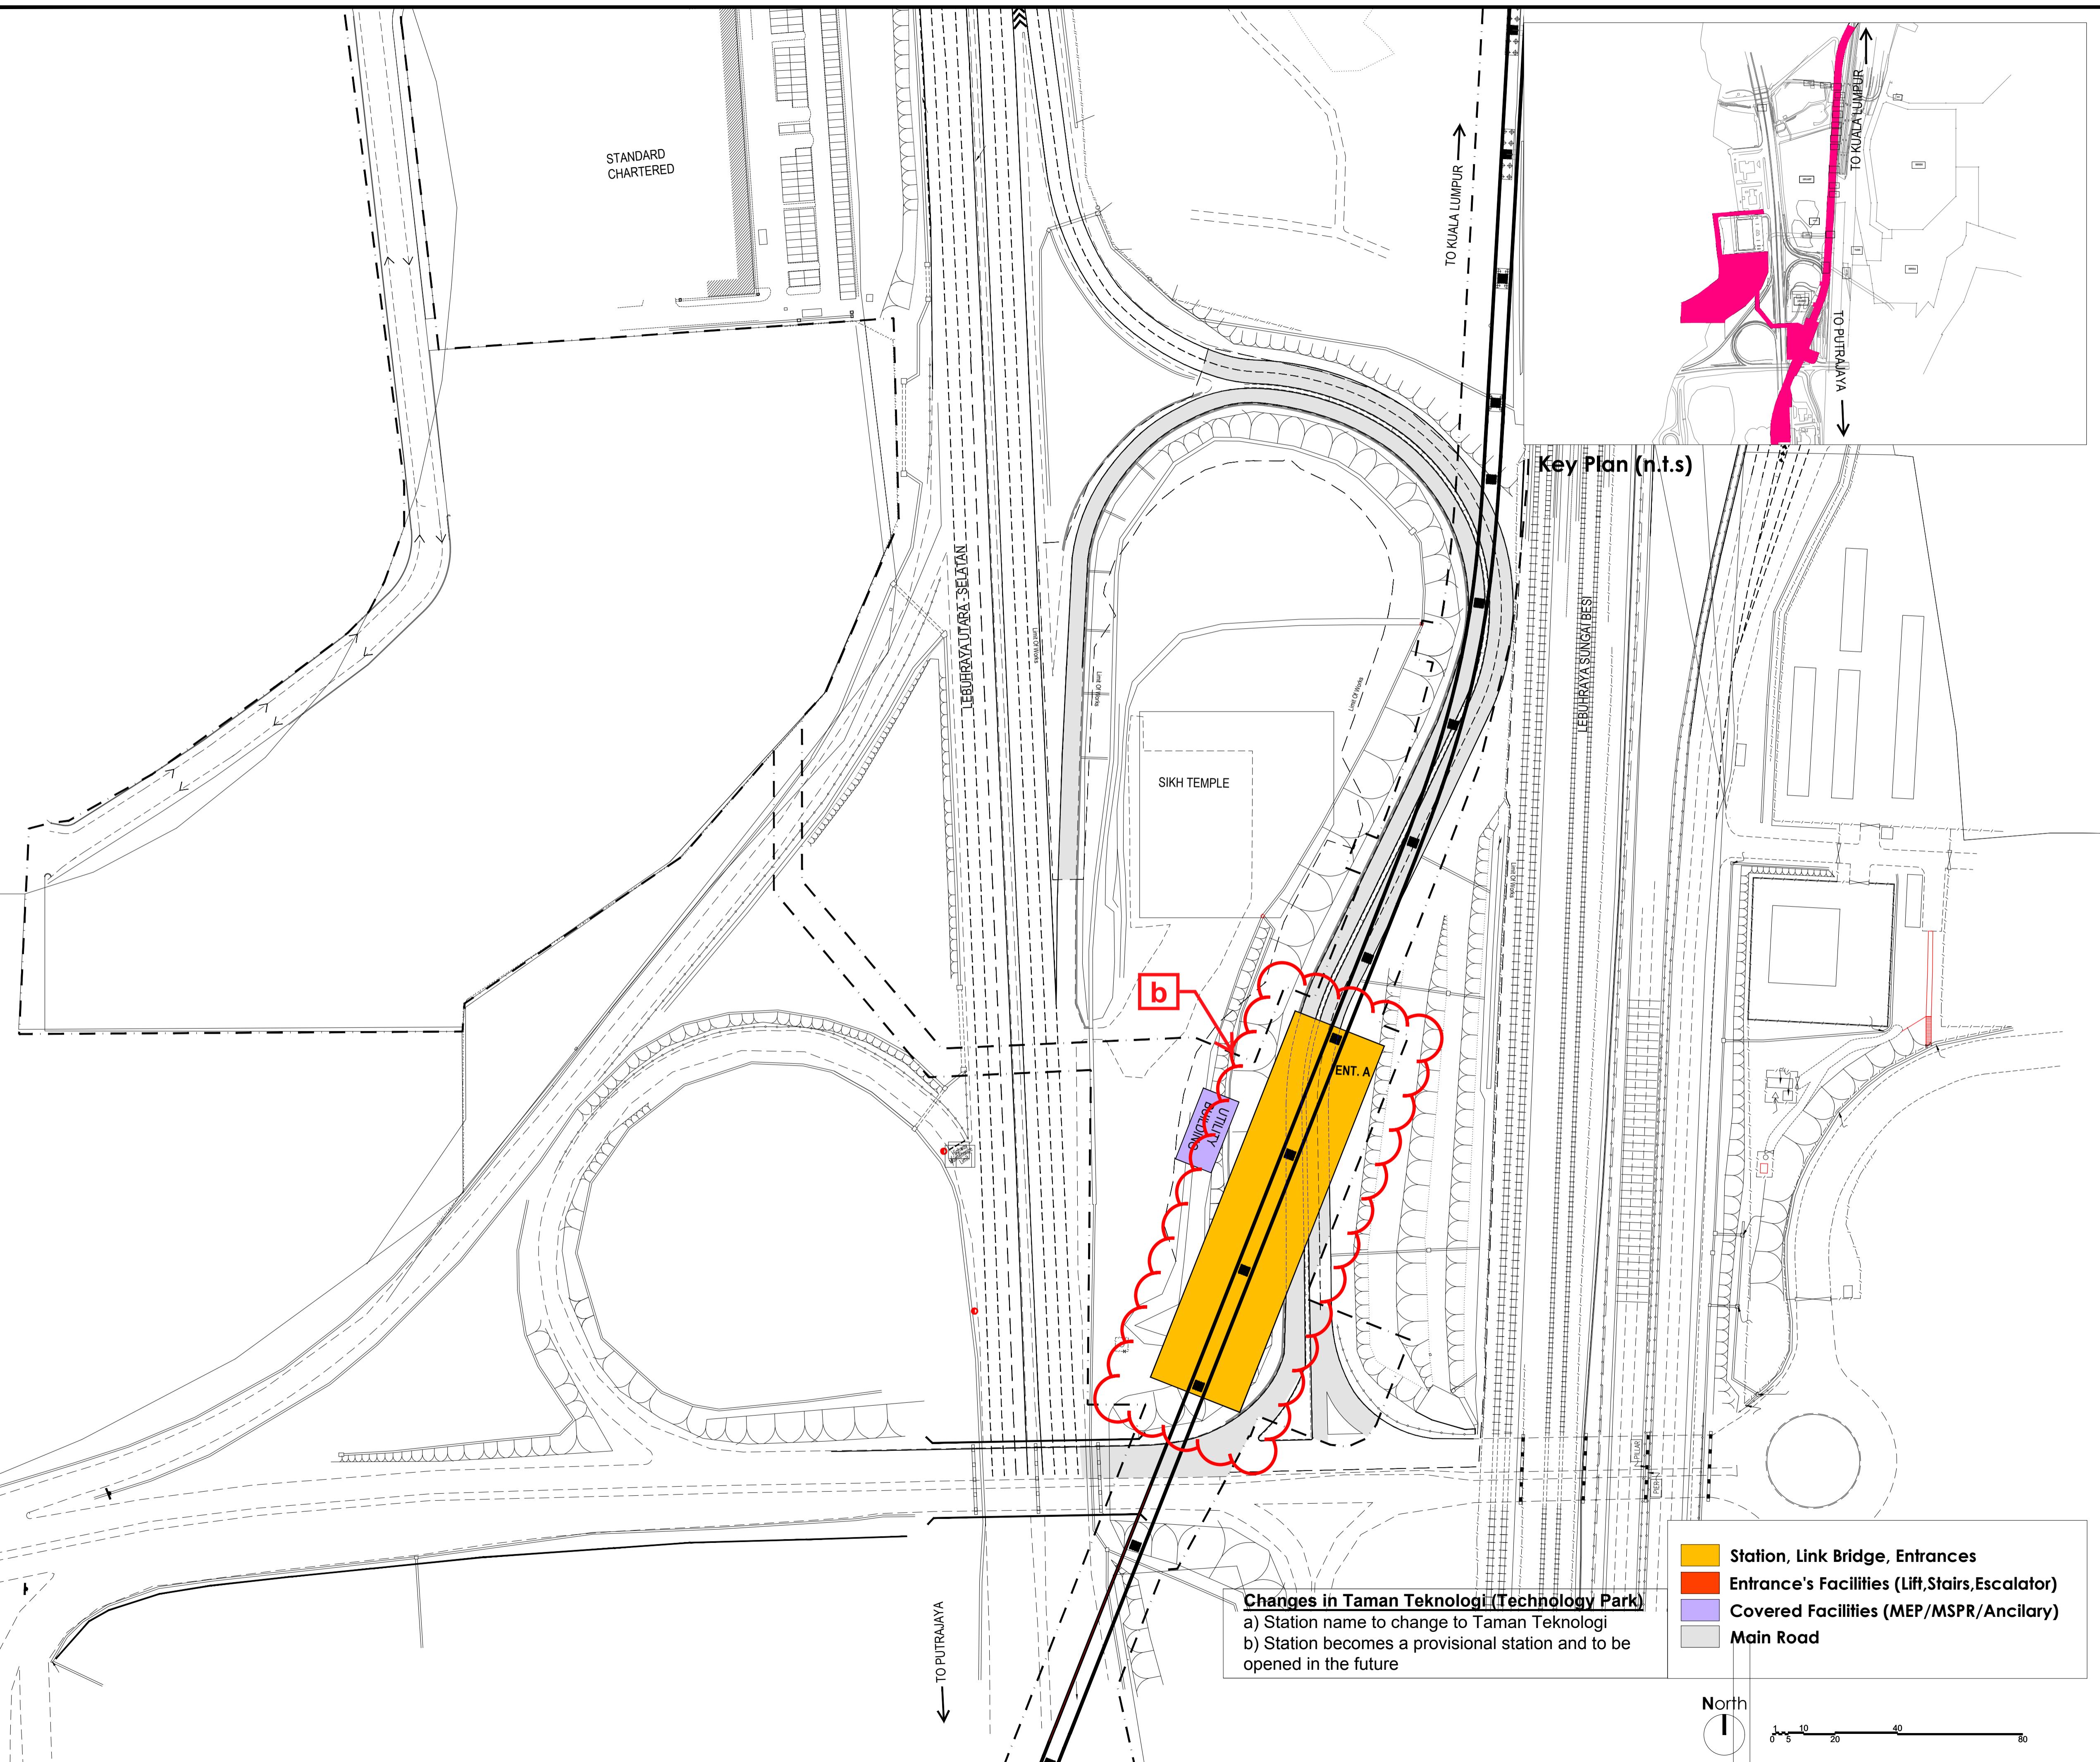

Drawing Title :  
**S30**  
**TAMAN TEKNOLOGI**  
(PREVIOUSLY KNOWN AS  
TECHNOLOGY PARK )

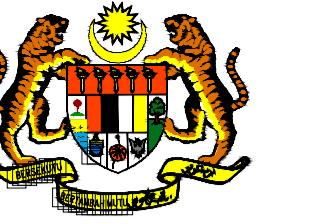

KERAJAAN MALAYSIA

PROJECT TITLE:  
PROJEK MASS RAPID TRANSIT LALUAN 2:  
PUTRAJAYA LINE  
(formerly known as PROJEK MRT LALUAN 2:  
SG BULOH - SERDANG - PUTRAJAYA (SSP))


PROJECT PACKAGE:  
ELEVATED SOUTH


SUPERVISING AGENCY :  
AGENSI PENGANGKUTAN  
AWAM DARAT (APAD)  
LAND PUBLIC TRANSPORT  
A G E N C Y ( A P A D )

AGENSI PENGANGKUTAN AWAM DARAT  
(A.P.A.D.)

ARAS G, M DAN 20, MENARA TUN ISMAIL MOHAMED ALI,  
NO. 25, JALAN RAJA LAUT, 50350 KUALA LUMPUR,  
MALAYSIA.  
TEL (ARAS G): 603-2603 6700 / TEL (ARAS 20): 603-2603 6600

PROJECT OWNER :  
**MRT**  
Mass Rapid Transit Corporation Sdn Bhd  
(902884-V)  
5th FLOOR MENARA I&P 1,  
JALAN DUNGUN, DAMANSARA HEIGHTS,  
50490 KUALA LUMPUR.

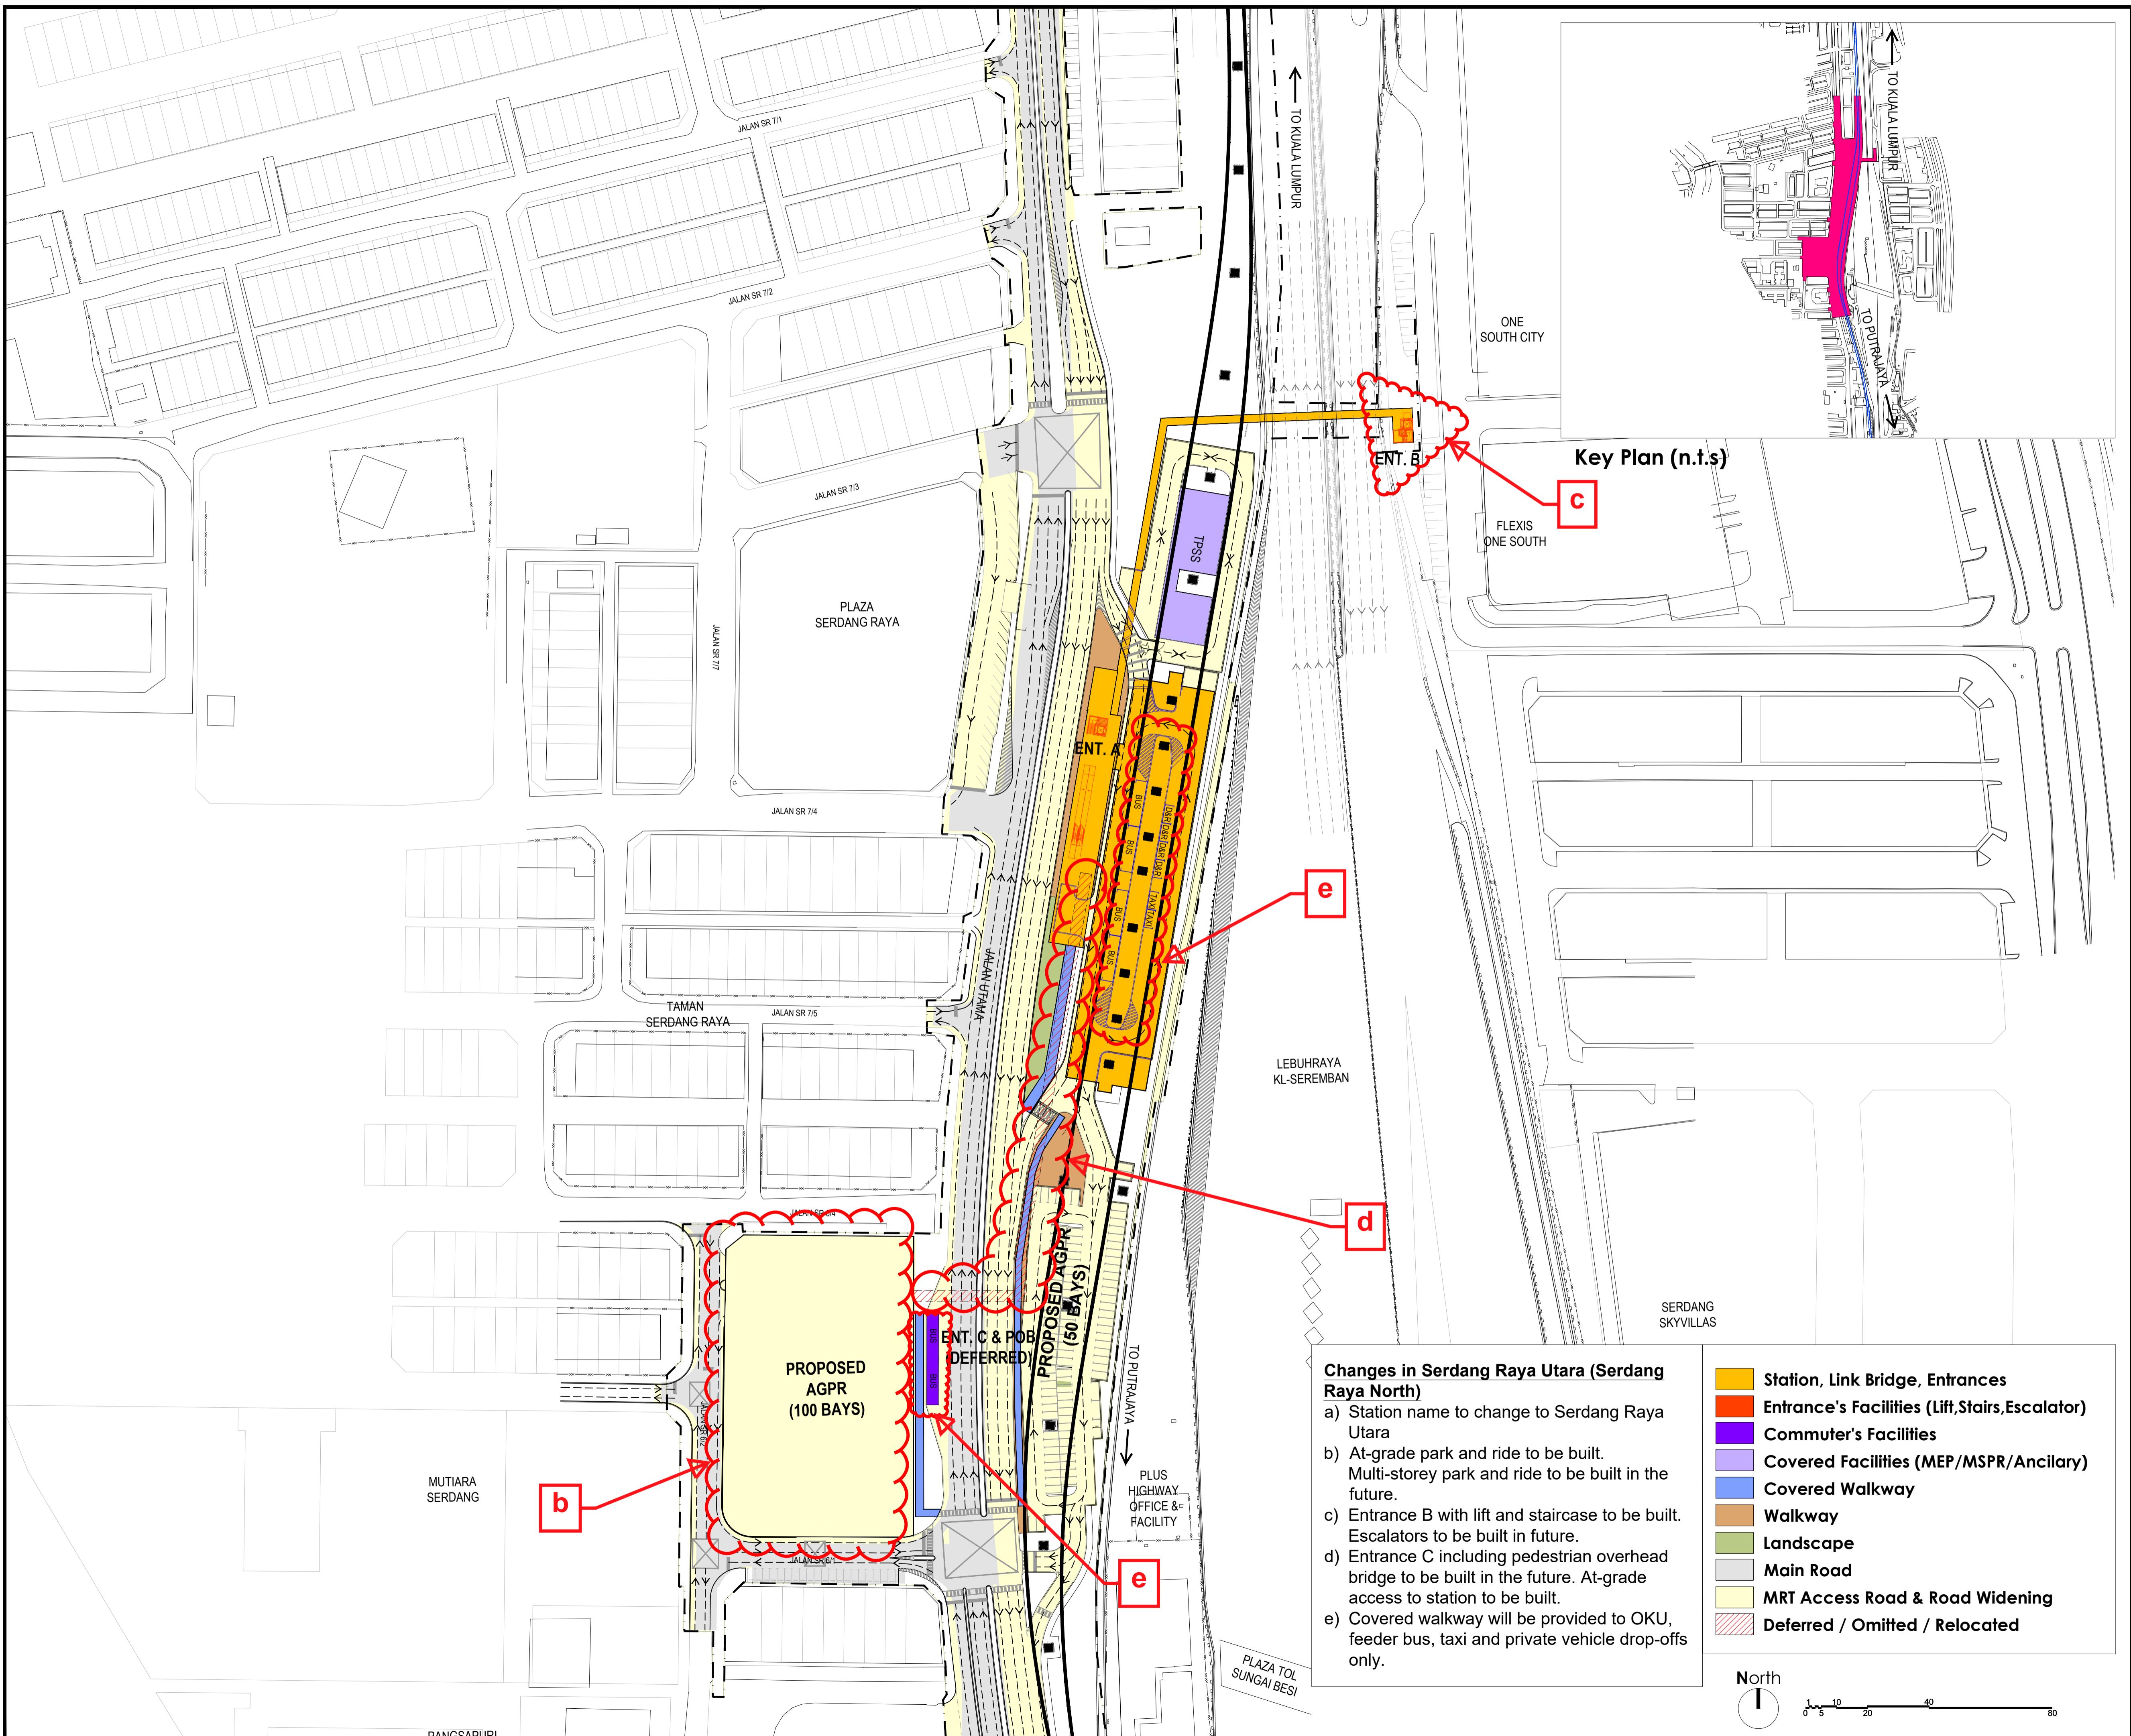

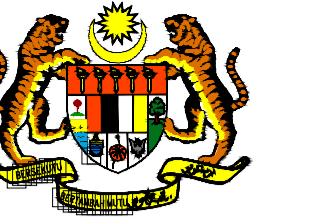

KERAJAAN MALAYSIA

PROJECT TITLE:  
PROJEK MASS RAPID TRANSIT LALUAN 2:  
PUTRAJAYA LINE  
(formerly known as PROJEK MRT LALUAN 2:  
SG BULOH - SERDANG - PUTRAJAYA (SSP))

PROJECT PACKAGE:  
ELEVATED SOUTH



SUPERVISING AGENCY :  
**AGENSI PENGANGKUTAN AWAM DARAT (APAD)**  
LAND PUBLIC TRANSPORT AGENCY (APAD)

**AGENSI PENGANGKUTAN AWAM DARAT (A.P.A.D.)**

ARAS G, M DAN 20, MENARA TUN ISMAIL MOHAMED ALI,  
NO. 25, JALAN RAJA LAUT, 50350 KUALA LUMPUR,  
MALAYSIA.  
TEL (ARAS G): 603-2603 6700 / TEL (ARAS 20): 603-2603 6600

PROJECT OWNER :  
**MRT CORP**  
Mass Rapid Transit Corporation Sdn Bhd  
(902884-V)  
5th FLOOR MENARA I&P 1,  
JALAN DUNGUN, DAMANSARA HEIGHTS,  
50490 KUALA LUMPUR.

Key Plan (n.t.s)

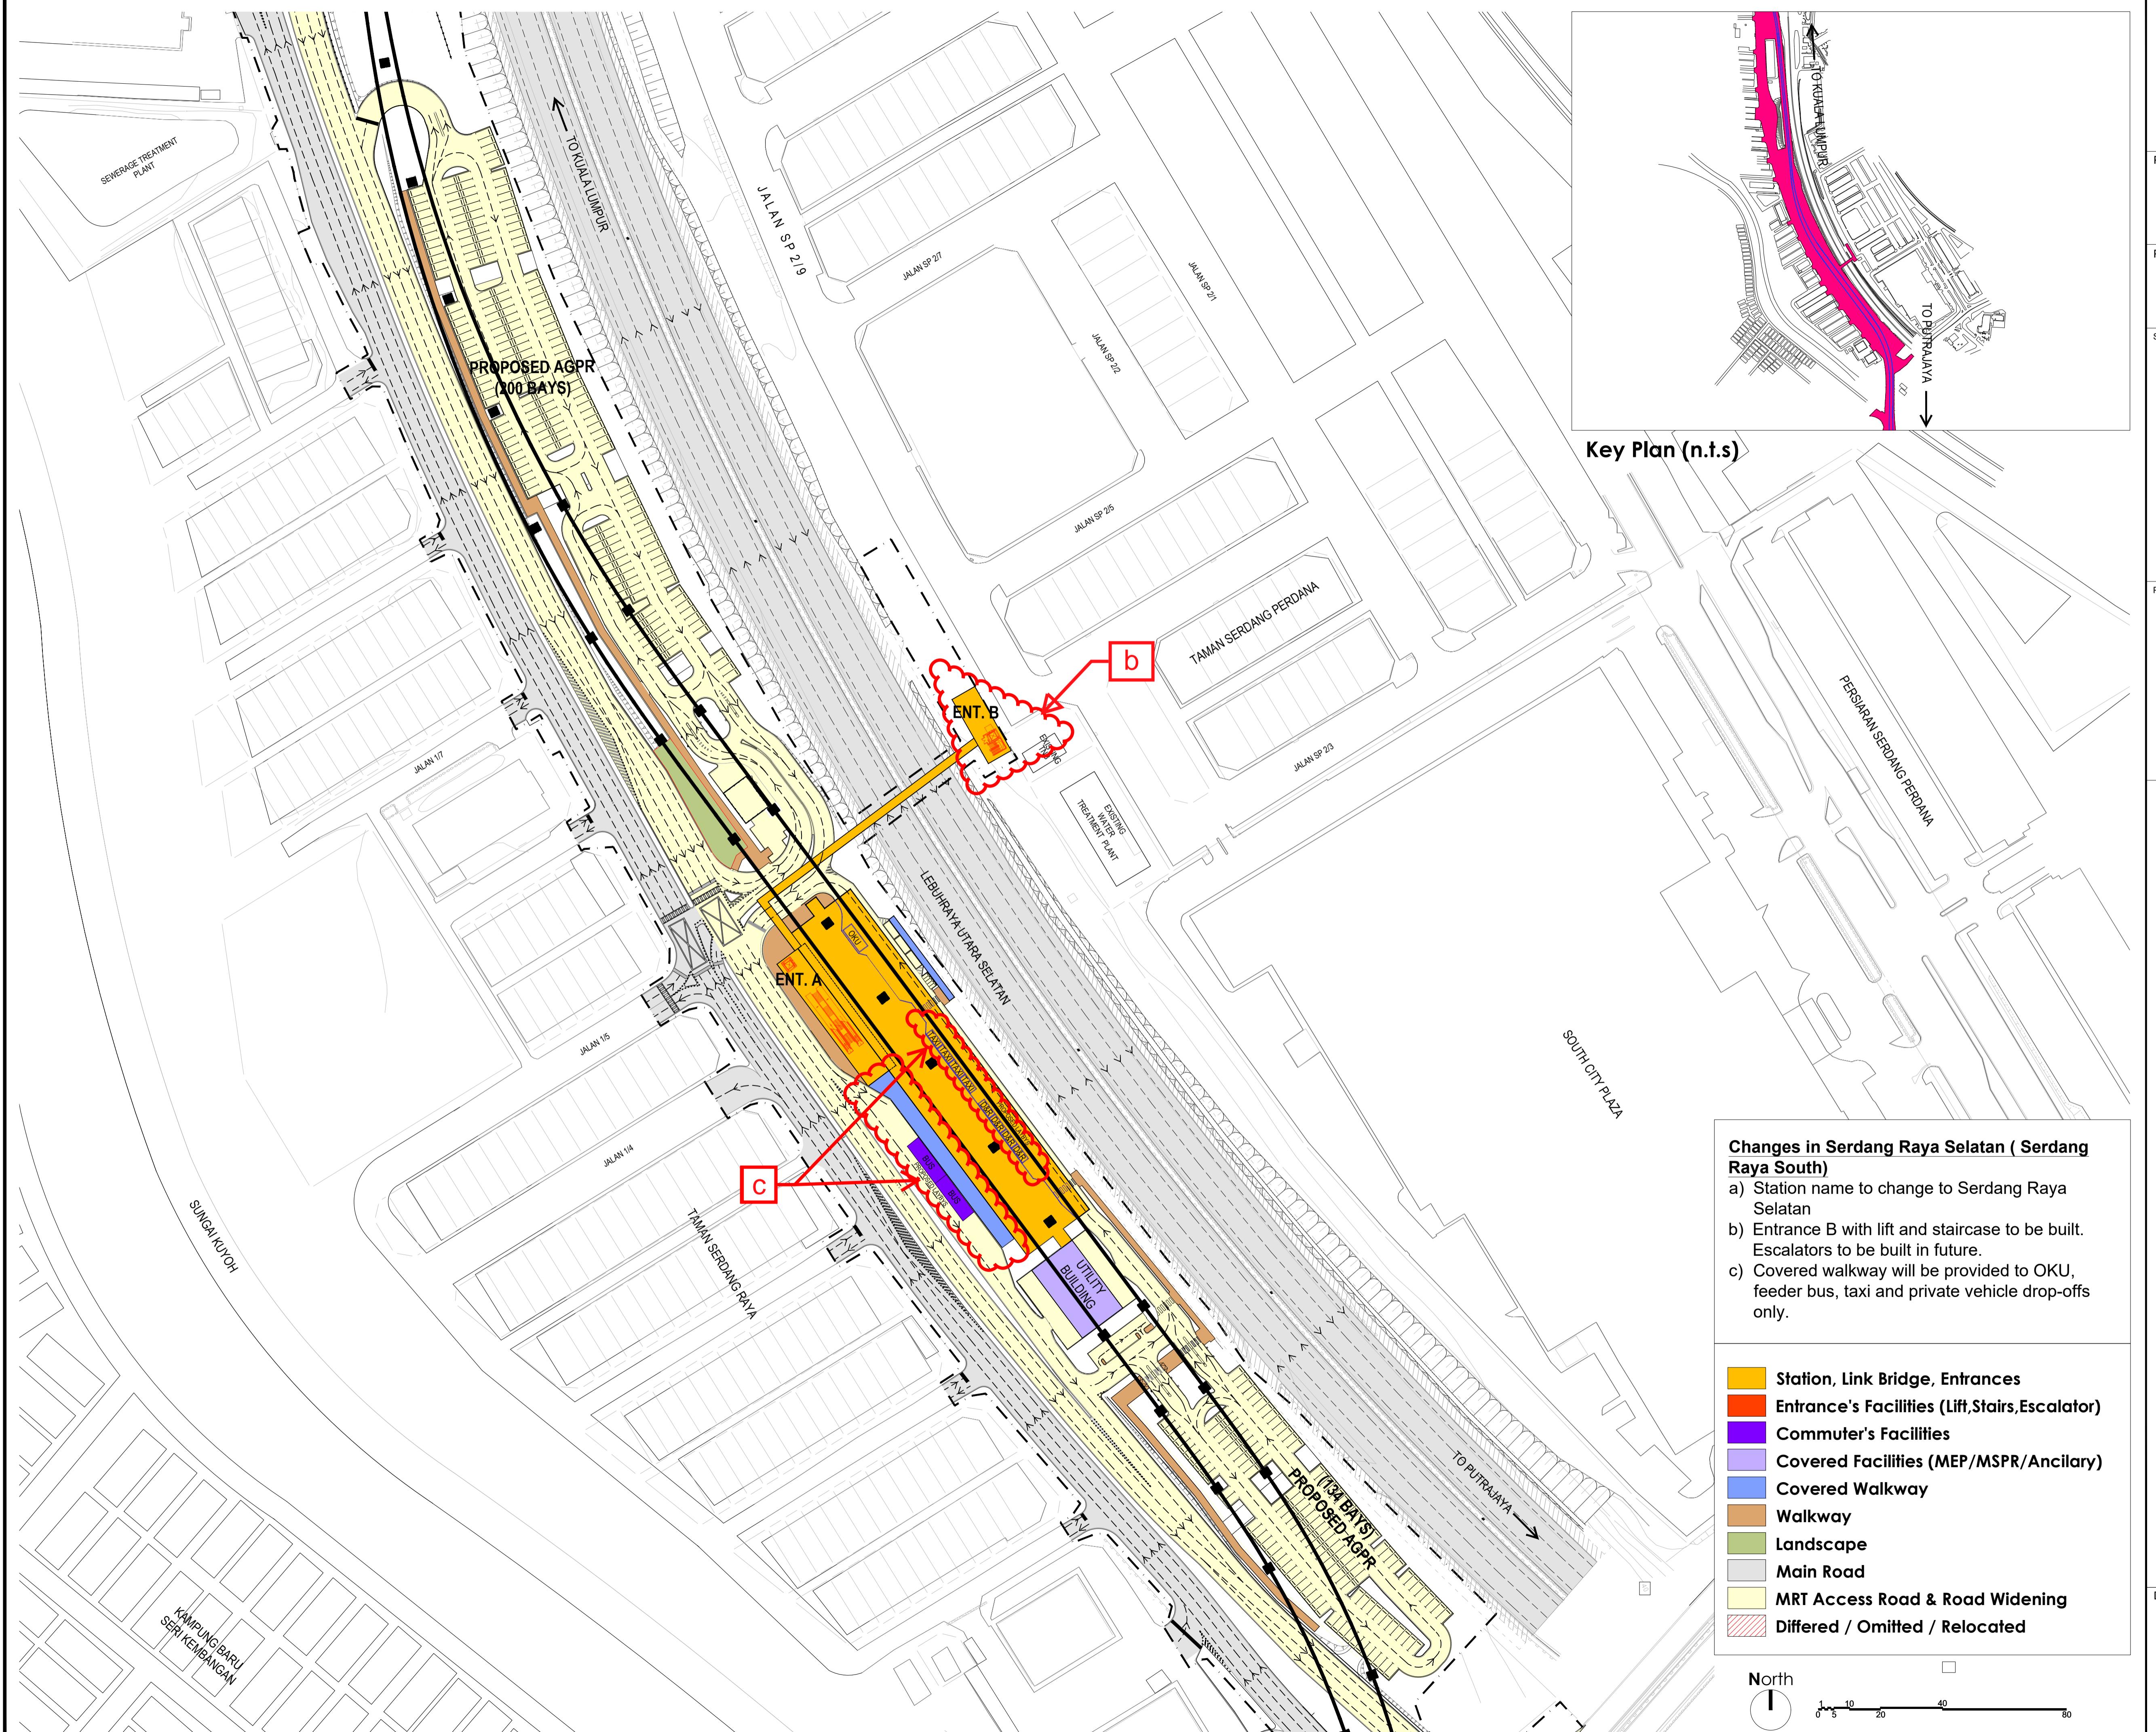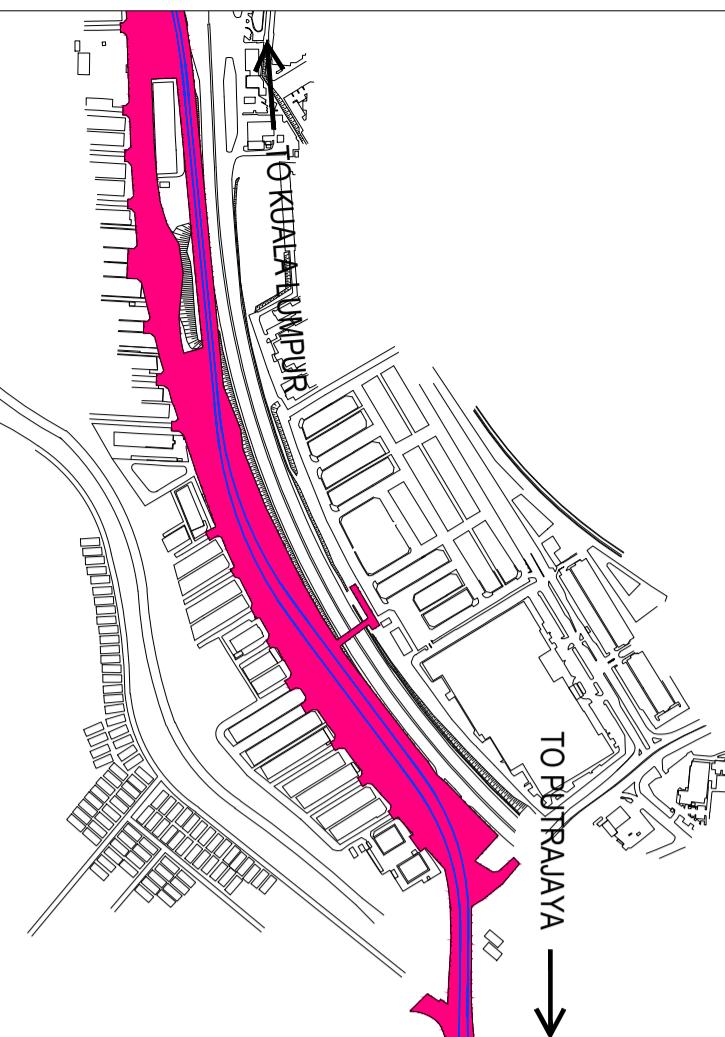



KERAJAAN MALAYSIA


PROJECT TITLE:  
PROJEK MASS RAPID TRANSIT LALUAN 2:  
PUTRAJAYA LINE  
(formerly known as PROJEK MRT LALUAN 2:  
SG BULOH - SERDANG - PUTRAJAYA (SSP))


PROJECT PACKAGE:  
ELEVATED SOUTH

SUPERVISING AGENCY :  
**AGENSI PENGANGKUTAN AWAM DARAT (APAD)**  
LAND PUBLIC TRANSPORT AGENCY (APAD)  
AGENSI PENGANGKUTAN AWAM DARAT (A.P.A.D.)

ARAS G, M DAN 20, MENARA TUN ISMAIL MOHAMED ALI,  
NO. 25, JALAN RAJA LAUT, 50350 KUALA LUMPUR,  
MALAYSIA.  
TEL (ARAS G): 603-2603 6700 / TEL (ARAS 20): 603-2603 6600

PROJECT OWNER :  
**MRT CORP**  
Mass Rapid Transit Corporation Sdn Bhd  
(902884-V)  
5th FLOOR MENARA I&P 1,  
JALAN DUNGUN, DAMANSARA HEIGHTS,  
50490 KUALA LUMPUR.

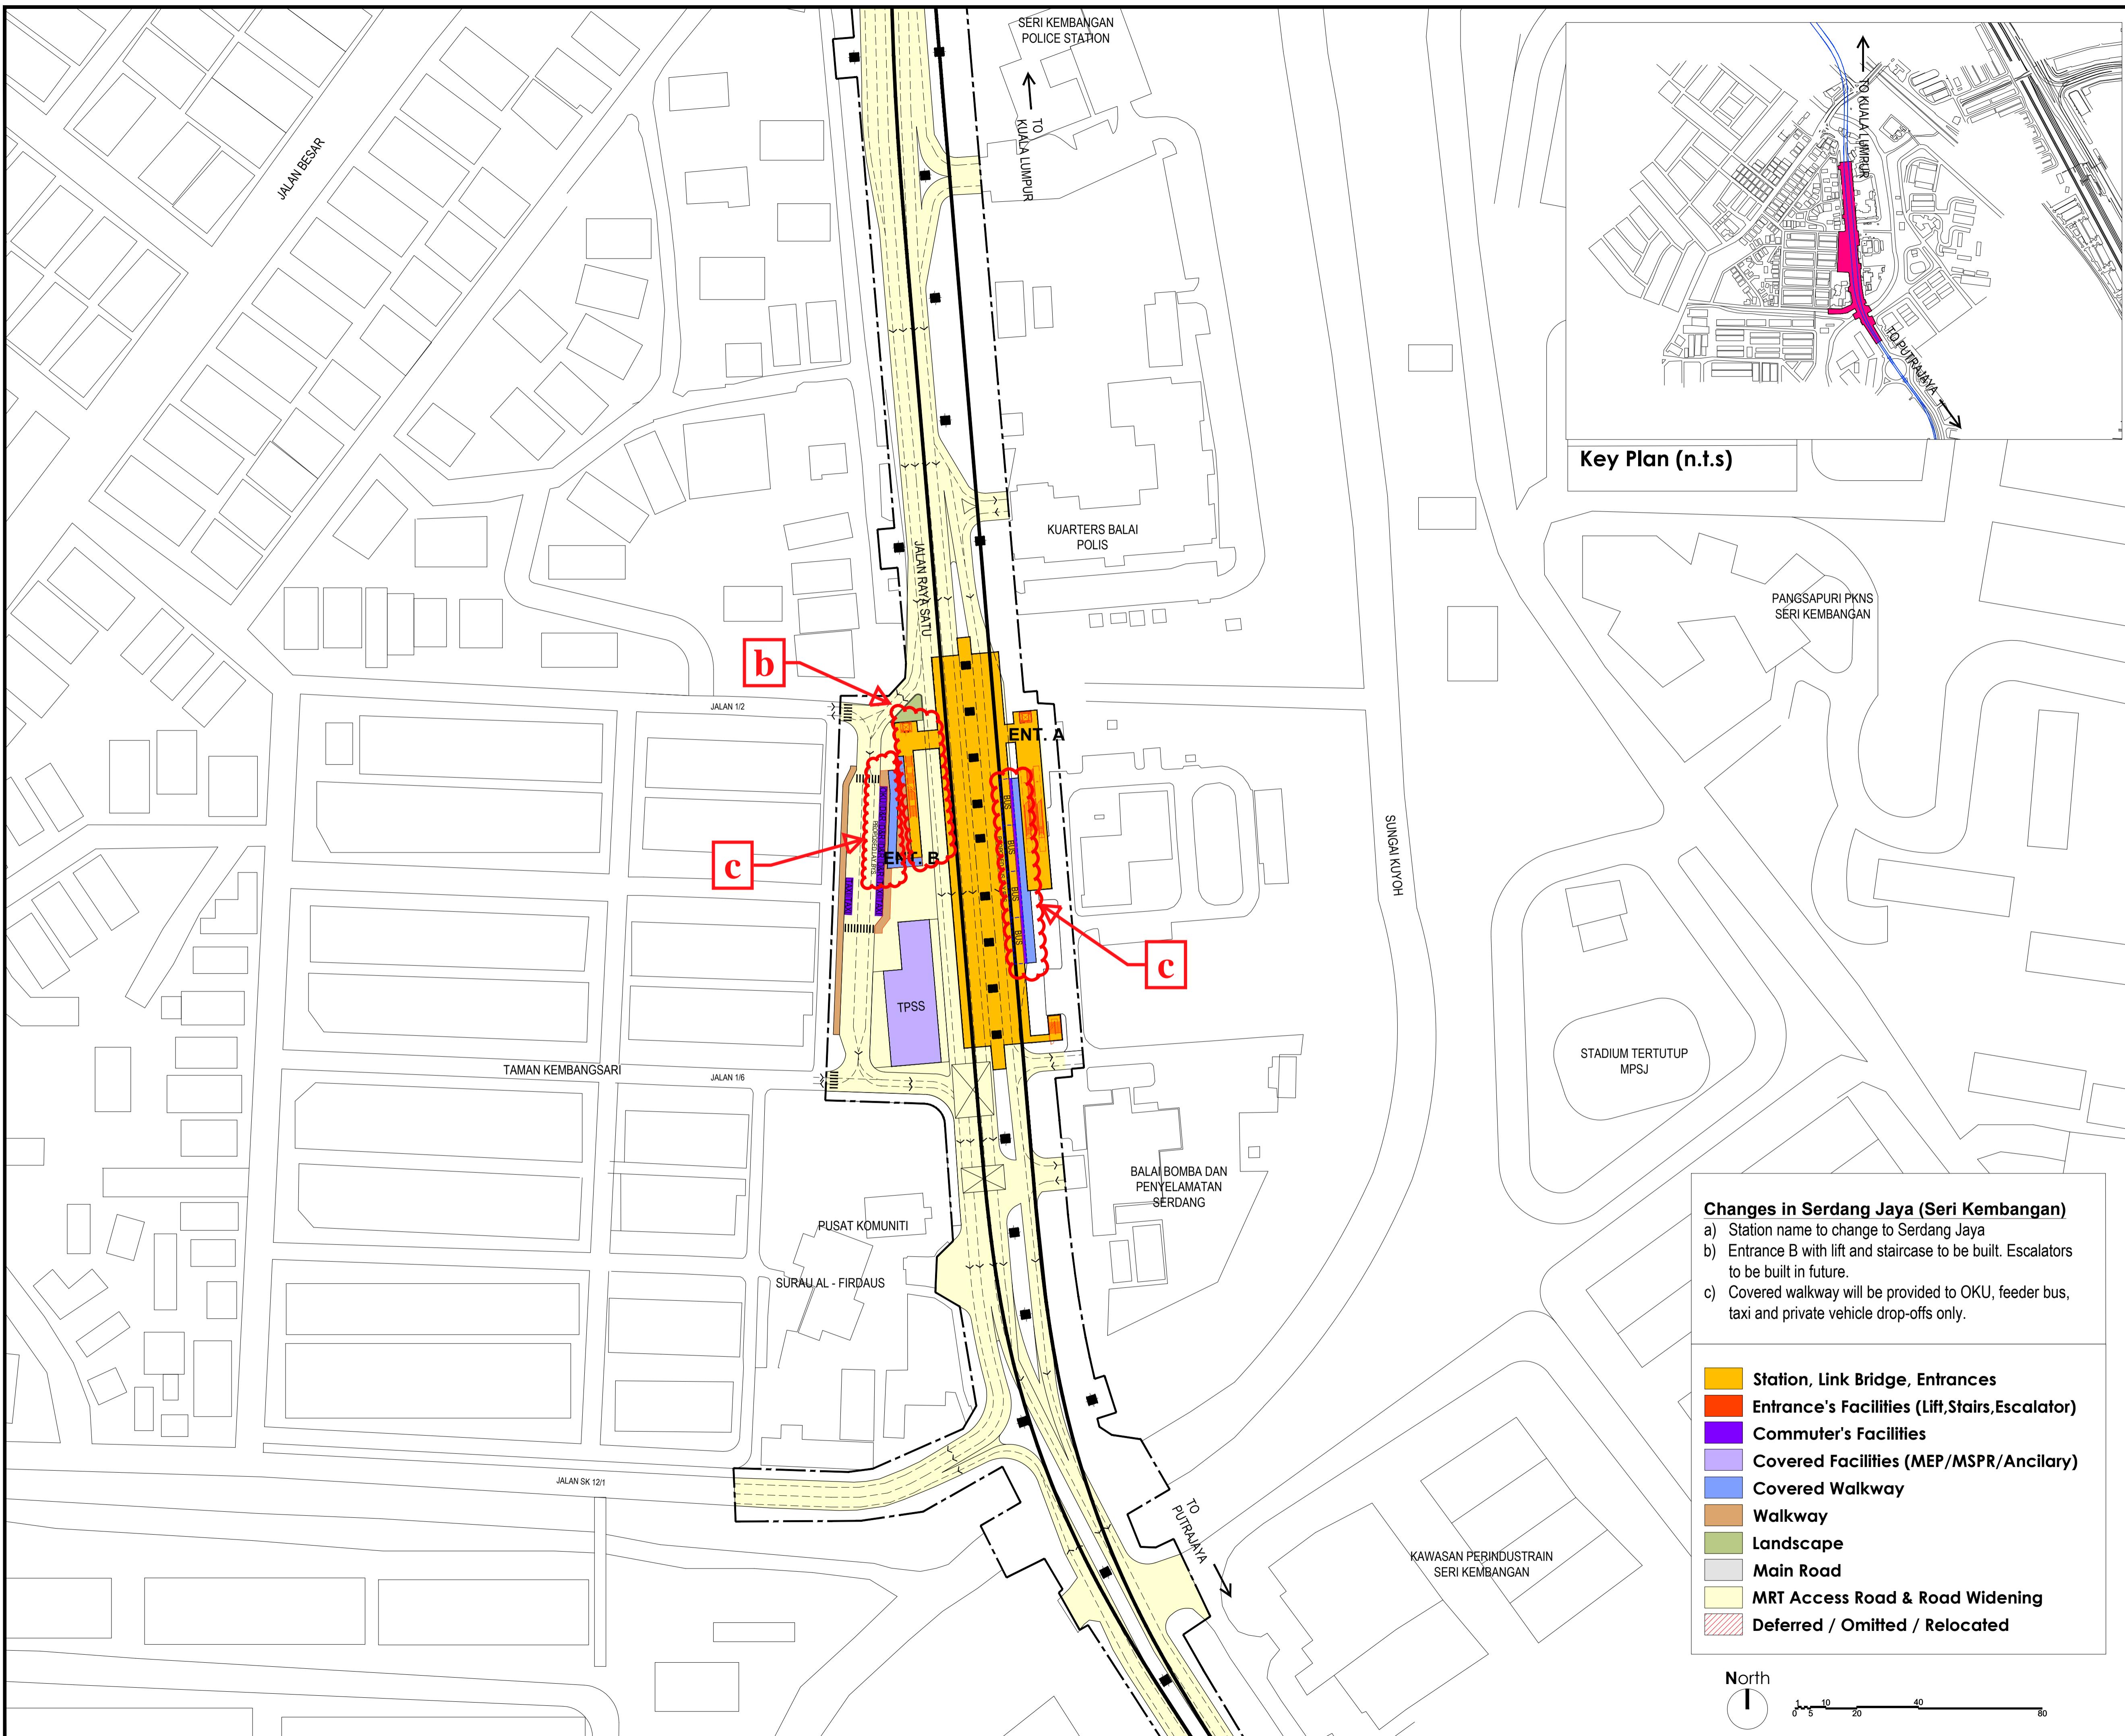

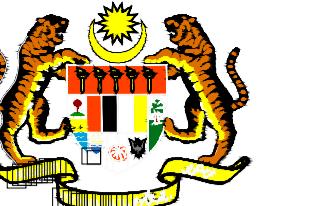

KERAJAAN MALAYSIA

PROJECT TITLE:  
PROJEK MASS RAPID TRANSIT LALUAN 2:  
PUTRAJAYA LINE  
(formerly known as PROJEK MRT LALUAN 2:  
SG BULOH - SERDANG - PUTRAJAYA (SSP))

PROJECT PACKAGE:  
ELEVATED SOUTH

AGENSI PENGANGKUTAN  
AWAM DARAT (APAD)  
LAND PUBLIC TRANSPORT  
A G E N C Y ( A P A D )

AGENSI PENGANGKUTAN AWAM DARAT  
(A.P.A.D.)


ARAS G, M DAN 20, MENARA TUN ISMAIL MOHAMED ALI,  
NO. 25, JALAN RAJA LAUT, 50350 KUALA LUMPUR,  
MALAYSIA.  
TEL (ARAS G): 603-2603 6700 / TEL (ARAS 20): 603-2603 6600


PROJECT OWNER :



Mass Rapid Transit Corporation Sdn Bhd  
(902884-V)

5th FLOOR MENARA I&P 1,  
JALAN DUNGUN, DAMANSARA HEIGHTS,  
50490 KUALA LUMPUR.

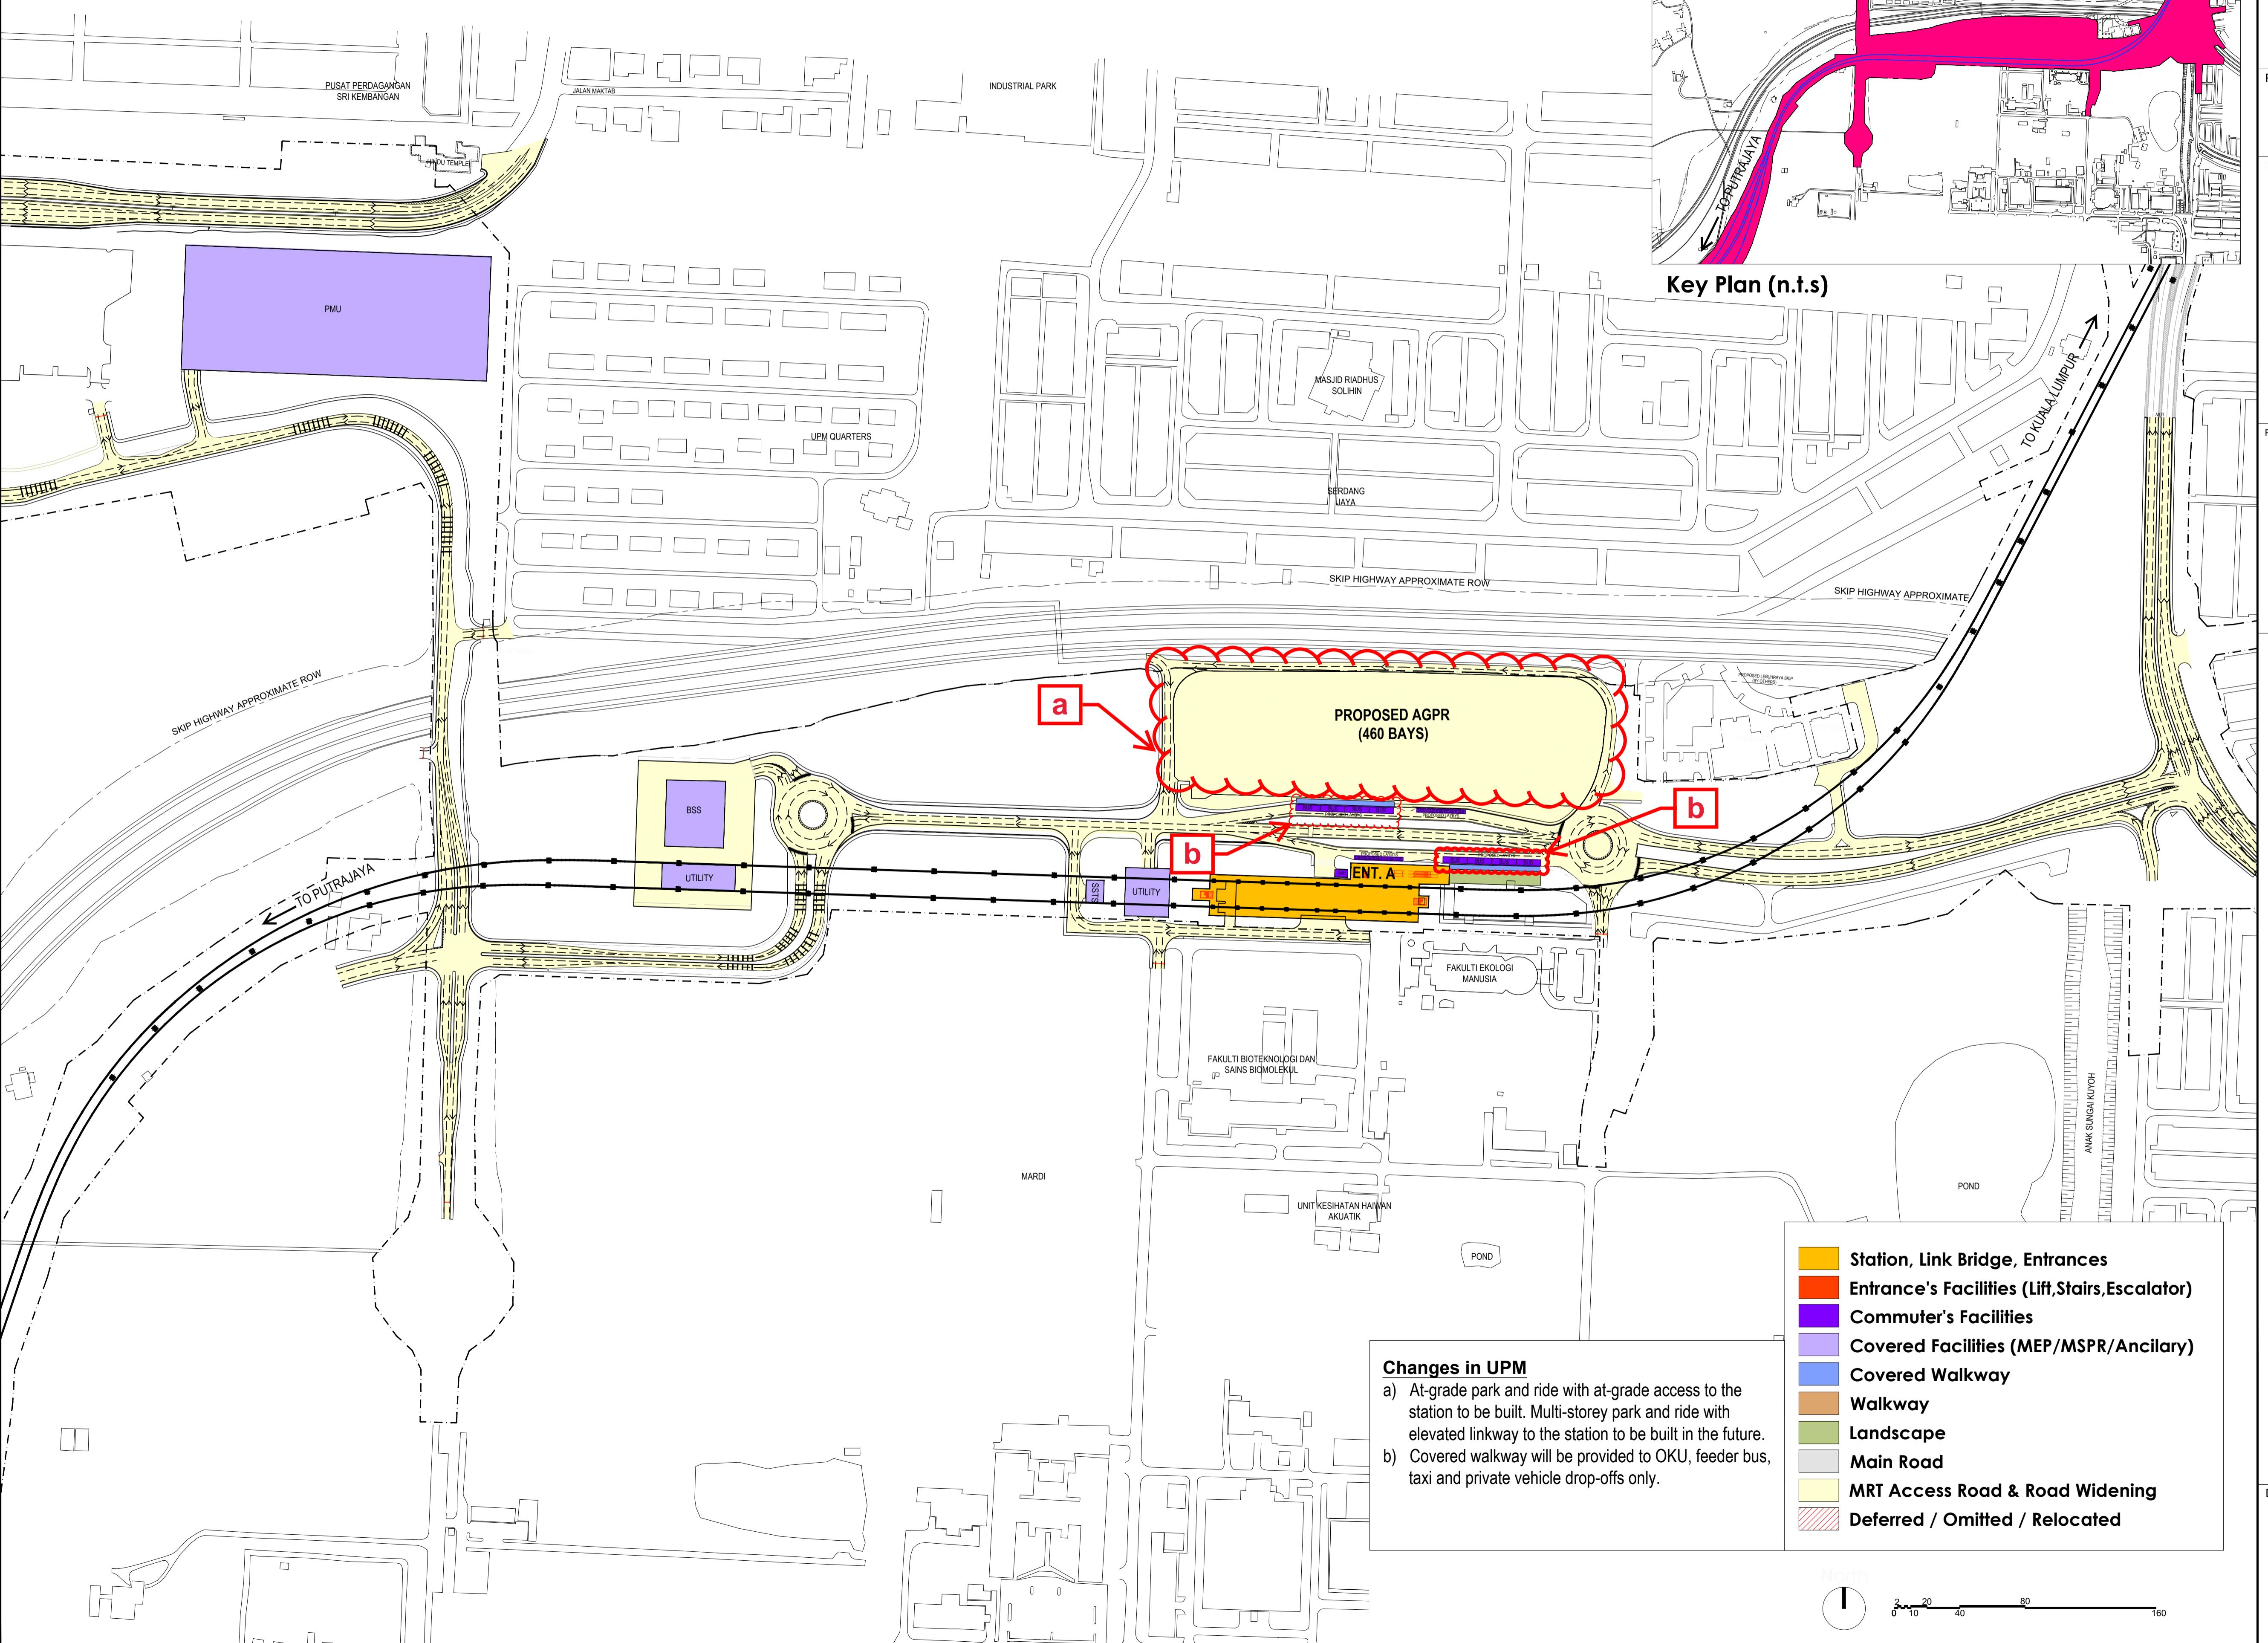

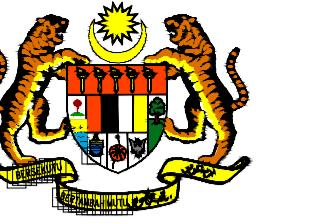

KERAJAAN MALAYSIA

PROJECT TITLE:  
PROJEK MASS RAPID TRANSIT LALUAN 2:  
PUTRAJAYA LINE  
(formerly known as PROJEK MRT LALUAN 2:  
SG BULOH - SERDANG - PUTRAJAYA (SSP))


PROJECT PACKAGE:  
ELEVATED SOUTH


SUPERVISING AGENCY :  
 AGENSI PENGANGKUTAN AWAM DARAT (APAD)  
LAND PUBLIC TRANSPORT AGENCY (APAD)

AGENSI PENGANGKUTAN AWAM DARAT  
(A.P.A.D.)

ARAS G, M DAN 20, MENARA TUN ISMAIL MOHAMED ALI,  
NO. 25, JALAN RAJA LAUT, 50350 KUALA LUMPUR,  
MALAYSIA.  
TEL (ARAS G): 603-2603 6700 / TEL (ARAS 20): 603-2603 6600

PROJECT OWNER :  
 MRT CORP  
Mass Rapid Transit Corporation Sdn Bhd  
(902884-V)  
5th FLOOR MENARA I&P 1,  
JALAN DUNGUN, DAMANSARA HEIGHTS,  
50490 KUALA LUMPUR.

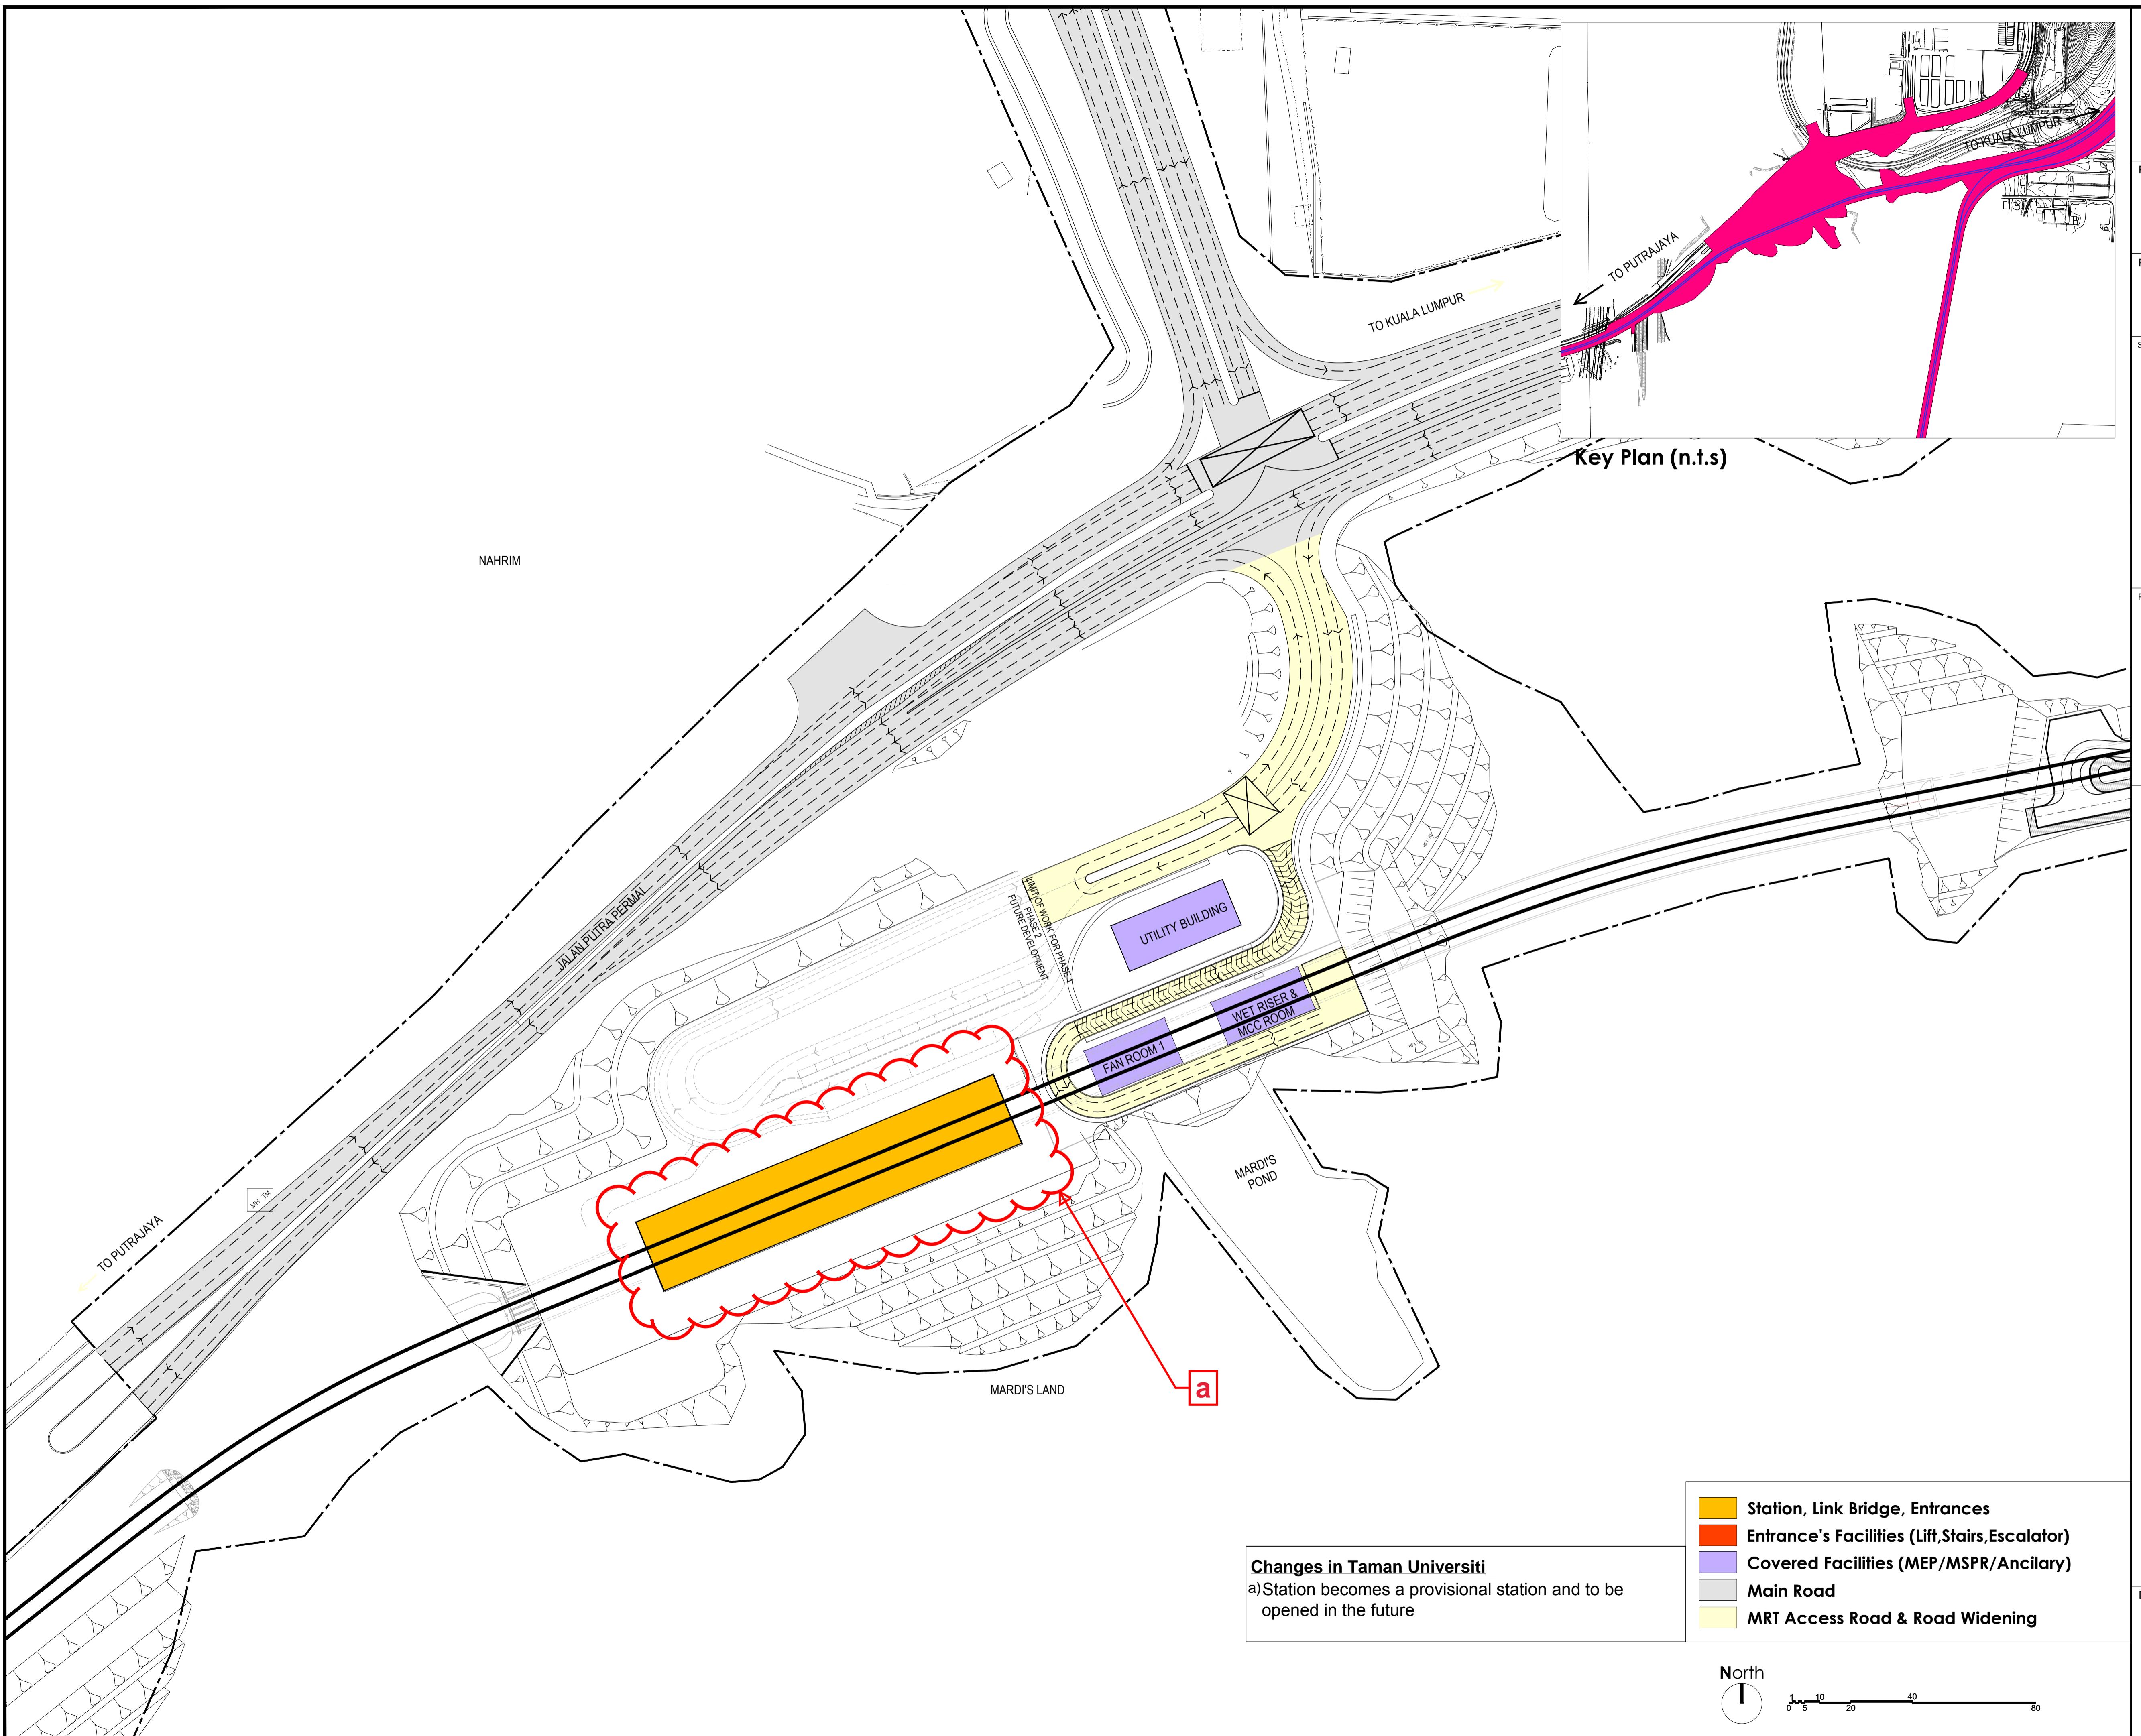

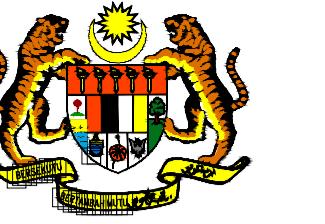

KERAJAAN MALAYSIA

PROJECT TITLE:  
PROJEK MASS RAPID TRANSIT LALUAN 2:  
PUTRAJAYA LINE  
(formerly known as PROJEK MRT LALUAN 2:  
SG BULOH - SERDANG - PUTRAJAYA (SSP))

PROJECT PACKAGE:


ELEVATED SOUTH


SUPERVISING AGENCY :  
 AGENSI PENGANGKUTAN AWAM DARAT (APAD)  
LAND PUBLIC TRANSPORT AGENCY (APAD)

AGENSI PENGANGKUTAN AWAM DARAT  
(A.P.A.D.)

ARAS G, M DAN 20, MENARA TUN ISMAIL MOHAMED ALI,  
NO. 25, JALAN RAJA LAUT, 50350 KUALA LUMPUR,  
MALAYSIA.  
TEL (ARAS G): 603-2603 6700 / TEL (ARAS 20): 603-2603 6600

PROJECT OWNER :  
 MRT CORP  
Mass Rapid Transit Corporation Sdn Bhd  
(902884-V)  
5th FLOOR MENARA I&P 1,  
JALAN DUNGUN, DAMANSARA HEIGHTS,  
50490 KUALA LUMPUR.

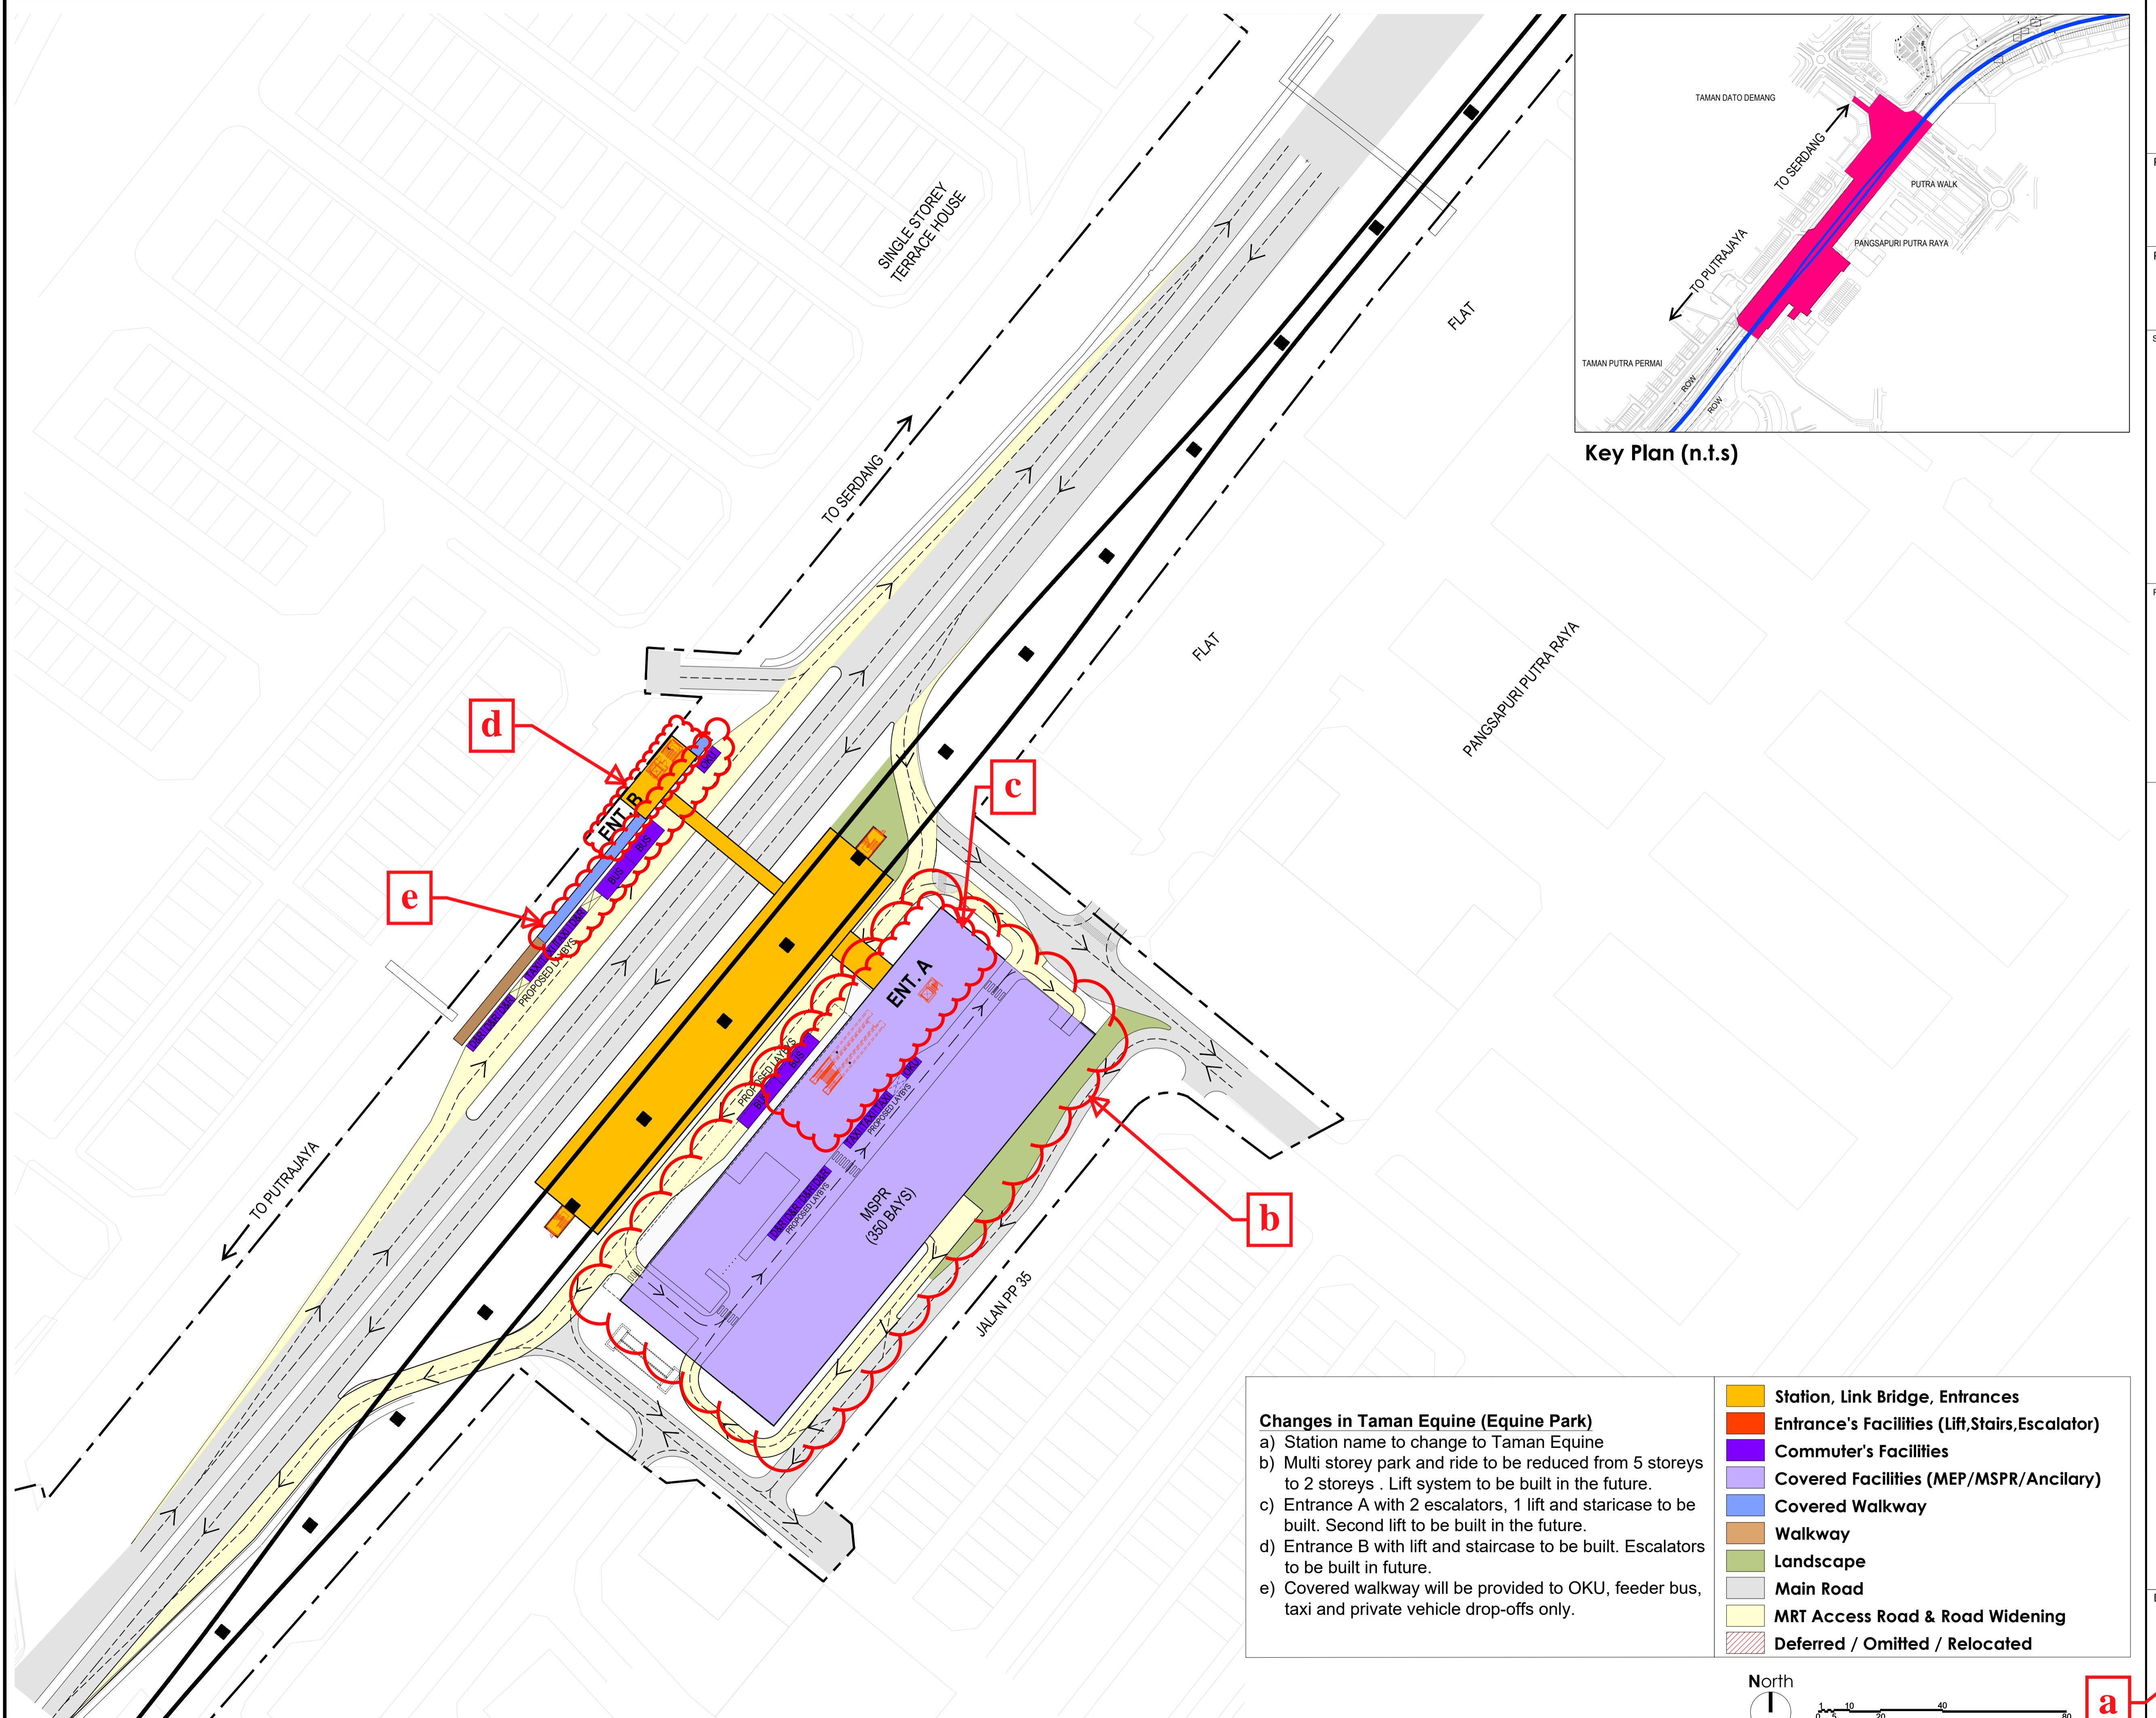

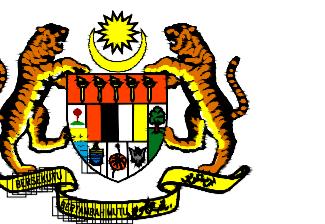

KERAJAAN MALAYSIA


PROJECT TITLE:  
PROJEK MASS RAPID TRANSIT LALUAN 2:  
PUTRAJAYA LINE  
(formerly known as PROJEK MRT LALUAN 2:  
SG BULOH - SERDANG - PUTRAJAYA (SSP))

PROJECT PACKAGE:  
SERDANG - PUTRAJAYA


SUPERVISING AGENCY :  
**AGENSI PENGANGKUTAN AWAM DARAT (APAD)**  
LAND PUBLIC TRANSPORT AGENCY (APAD)  
AGENSI PENGANGKUTAN AWAM DARAT (A.P.A.D.)

ARAS G, M DAN 20, MENARA TUN ISMAIL MOHAMED ALI,  
NO. 25, JALAN RAJA LAUT, 50350 KUALA LUMPUR,  
MALAYSIA.  
TEL (ARAS G): 603-2603 6700 / TEL (ARAS 20): 603-2603 6600

PROJECT OWNER :  
**MRT CORP**  
Mass Rapid Transit Corporation Sdn Bhd  
(902884-V)  
5th FLOOR MENARA I&P 1,  
JALAN DUNGUN, DAMANSARA HEIGHTS,  
50490 KUALA LUMPUR.

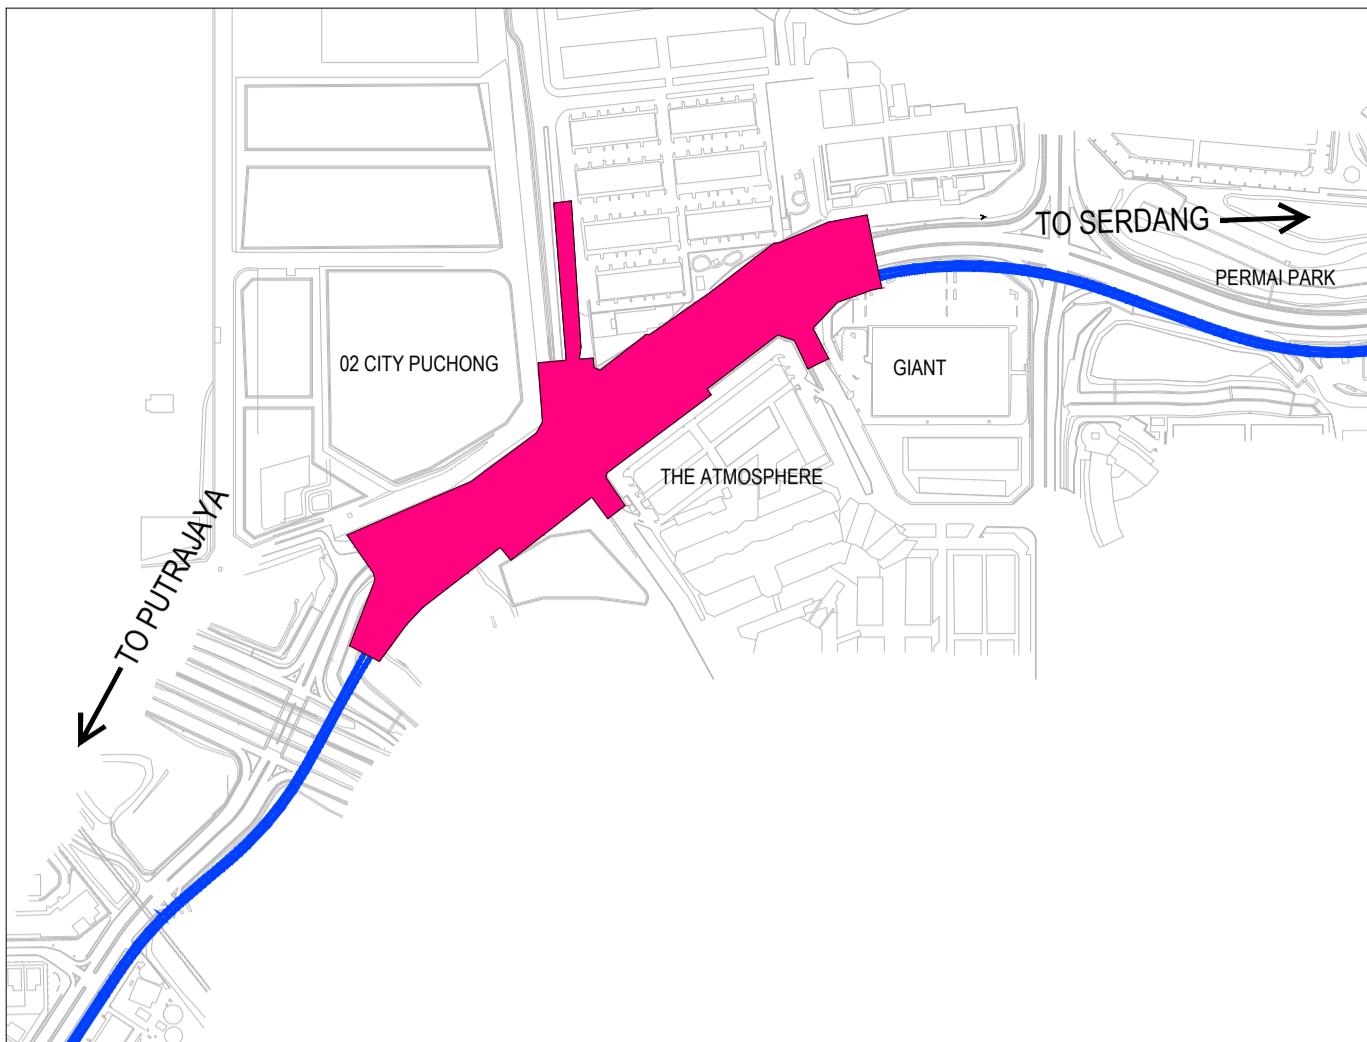

Key Plan (n.t.s)

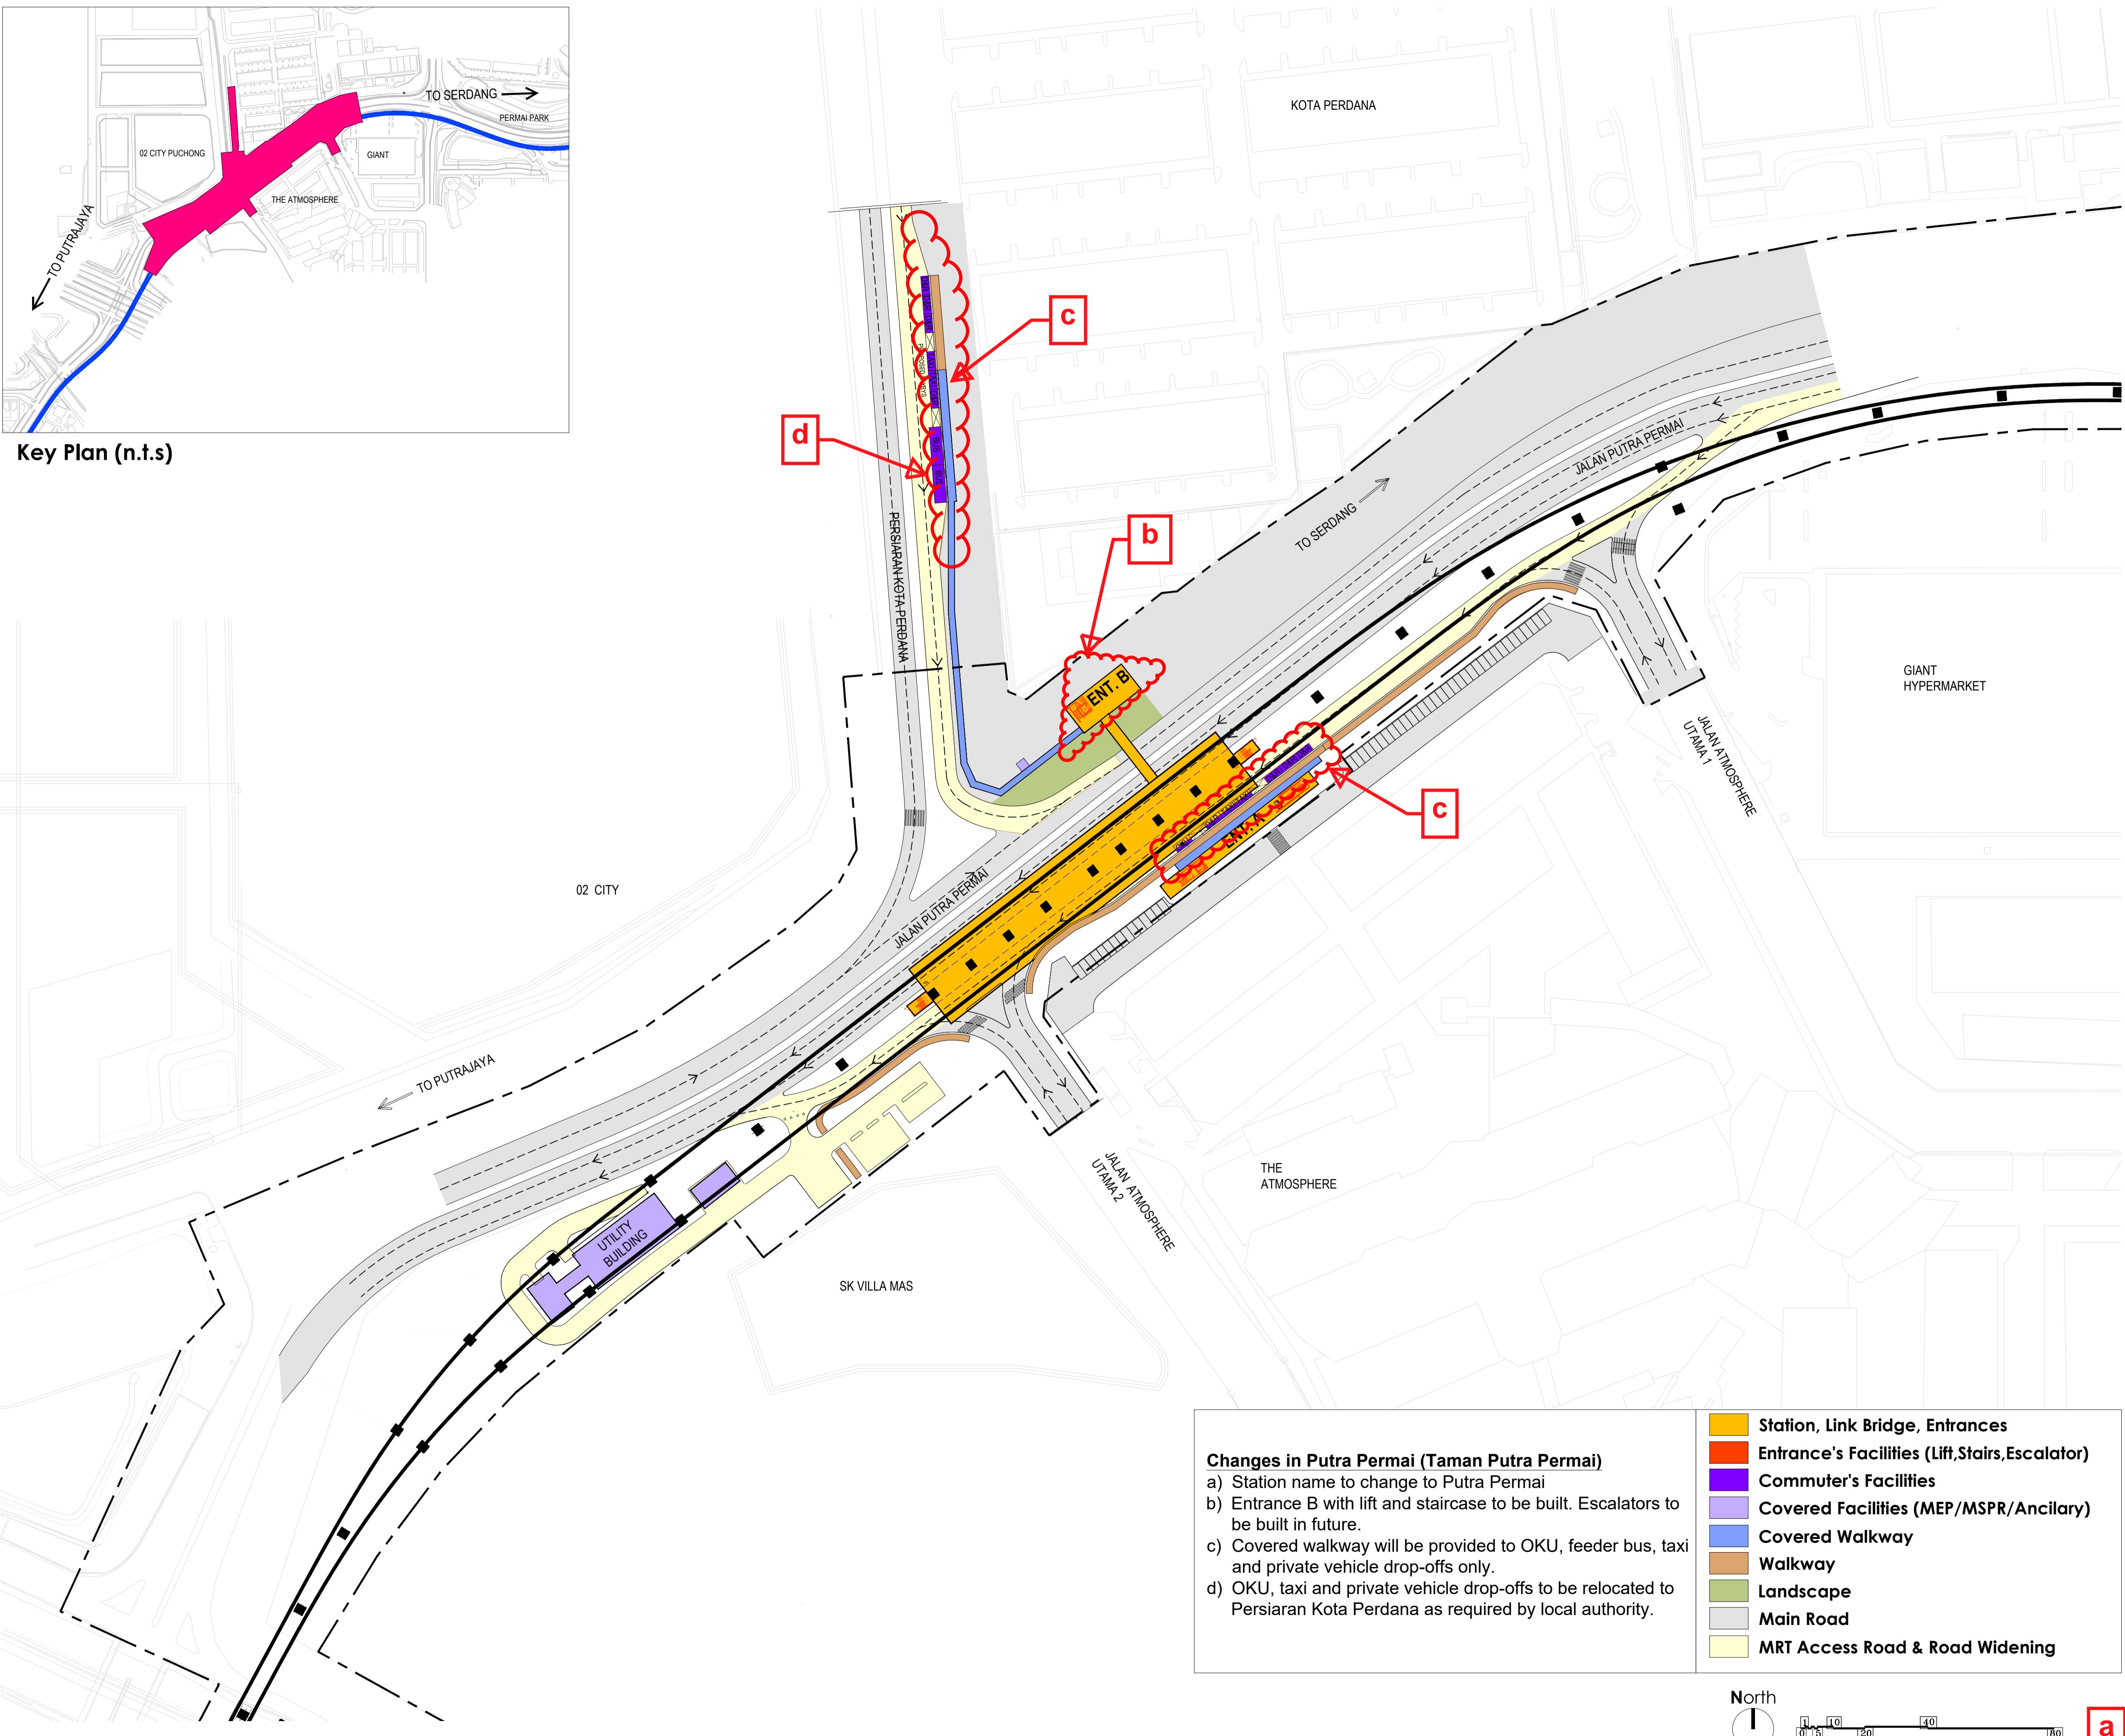


**Changes in Putra Permai (Taman Putra Permai)**

- a) Station name to change to Putra Permai
- b) Entrance B with lift and staircase to be built. Escalators to be built in future.
- c) Covered walkway will be provided to OKU, feeder bus, taxi and private vehicle drop-offs only.
- d) OKU, taxi and private vehicle drop-offs to be relocated to Persiaran Kota Perdana as required by local authority.

<b>Station, Link Bridge, Entrances</b>
<b>Entrance's Facilities (Lift,Stairs,Escalator)</b>
<b>Commuter's Facilities</b>
<b>Covered Facilities (MEP/MSPR/Ancillary)</b>
<b>Covered Walkway</b>
<b>Walkway</b>
<b>Landscape</b>
<b>Main Road</b>
<b>MRT Access Road &amp; Road Widening</b>

North

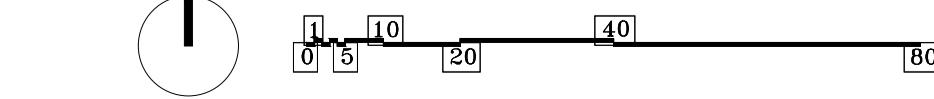

Drawing Title:  
**S37**  
**PUTRA PERMAI**  
(PREVIOUSLY KNOWN AS  
TAMAN PUTRA PERMAI)

a



# KERAJAAN MALAYSIA

**PROJECT TITLE:**  
**PROJEK MASS RAPID TRANSIT LALUAN 2:  
PUTRAJAYA LINE**  
(formerly known as PROJEK MRT LALUAN 2:  
SG BULOH - SERDANG - PUTRAJAYA (SSP))

## PROJECT PACKAGE: ELEVATED SOUTH

SUPERVISING AGENCY :

 **AGENSI PENGANGKUTAN AWAM DARAT (APAD)**

---

**LAND PUBLIC TRANSPORT AGENCY (APAD)**


ARAS G, M DAN 20, MENARA TUN ISMAIL MOHAMED ALI,  
NO. 25, JALAN RAJA LAUT, 50350 KUALA LUMPUR,  
MALAYSIA.  
TEL (ARAS G): 603-2603 6700 / TEL (ARAS 20): 603-2603 6600

The image contains the MRT Corp logo, which features a stylized blue and orange swoosh above the letters "MRT" in red, with "CORP" in smaller blue letters below it. Below the logo, the text "Mass Rapid Transit Corporation Sdn Bhd" is written in large black capital letters, followed by the registration number "(902884-V)" in parentheses.

PROJECT OWNER :

**Mass Rapid Transit Corporation Sdn Bhd**  
(902884-V)

## **Key Plan (n.t.s)**

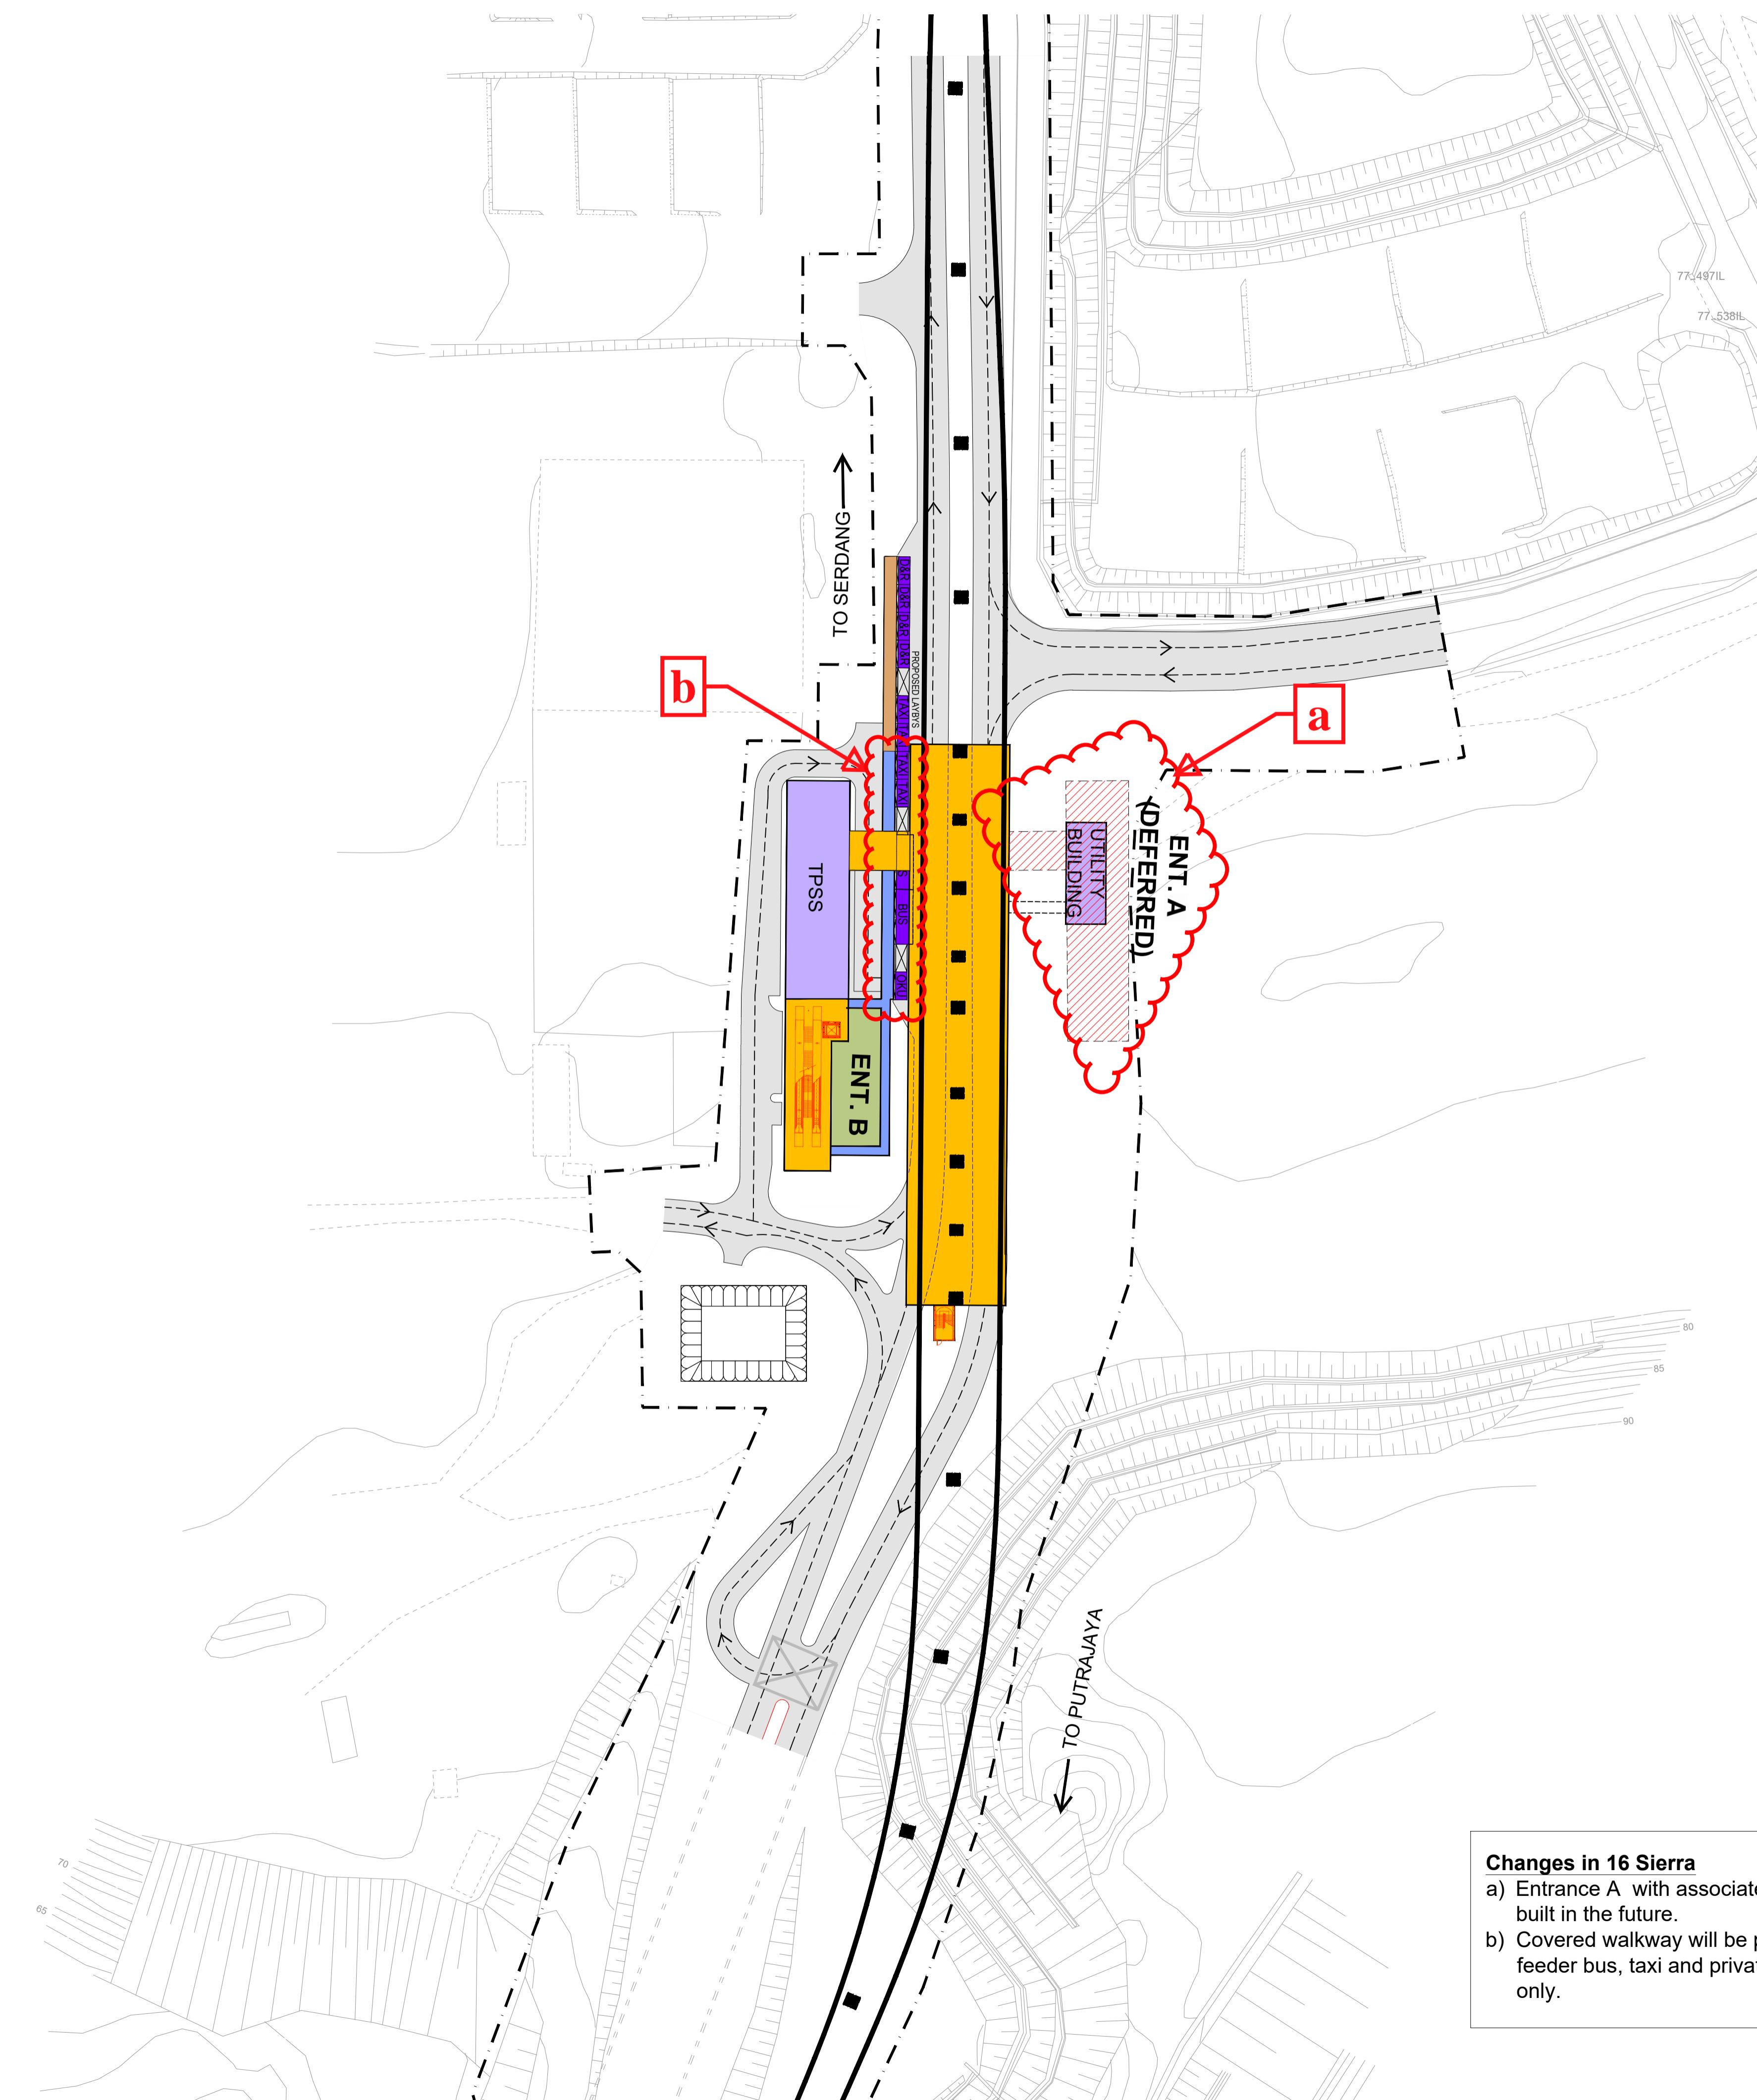

### **Changes in 16 Sigma**


- Changes in 16 Sierra**

  - a) Entrance A with associated linkway to be built in the future.
  - b) Covered walkway will be provided to OKU, feeder bus, taxi and private vehicle drop-offs only.



Drawing Title :

S38  
16 SIERRA

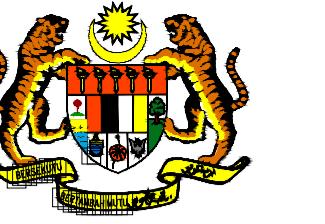

**KERAJAAN MALAYSIA**

PROJECT TITLE:  
PROJEK MASS RAPID TRANSIT LALUAN 2:  
PUTRAJAYA LINE  
(formerly known as PROJEK MRT LALUAN 2:  
SG BULOH - SERDANG - PUTRAJAYA (SSP))


PROJECT PACKAGE:  
SERDANG - PUTRAJAYA


SUPERVISING AGENCY :  
**AGENSI PENGANGKUTAN AWAM DARAT (APAD)**  
LAND PUBLIC TRANSPORT AGENCY (APAD)

**AGENSI PENGANGKUTAN AWAM DARAT (A.P.A.D.)**

ARAS G, M DAN 20, MENARA TUN ISMAIL MOHAMED ALI,  
NO. 25, JALAN RAJA LAUT, 50350 KUALA LUMPUR,  
MALAYSIA.  
TEL (ARAS G): 603-2603 6700 / TEL (ARAS 20): 603-2603 6600

PROJECT OWNER :  
**MRT CORP**  
Mass Rapid Transit Corporation Sdn Bhd  
(902884-V)  
5th FLOOR MENARA I&P 1,  
JALAN DUNGUN, DAMANSARA HEIGHTS,  
50490 KUALA LUMPUR.

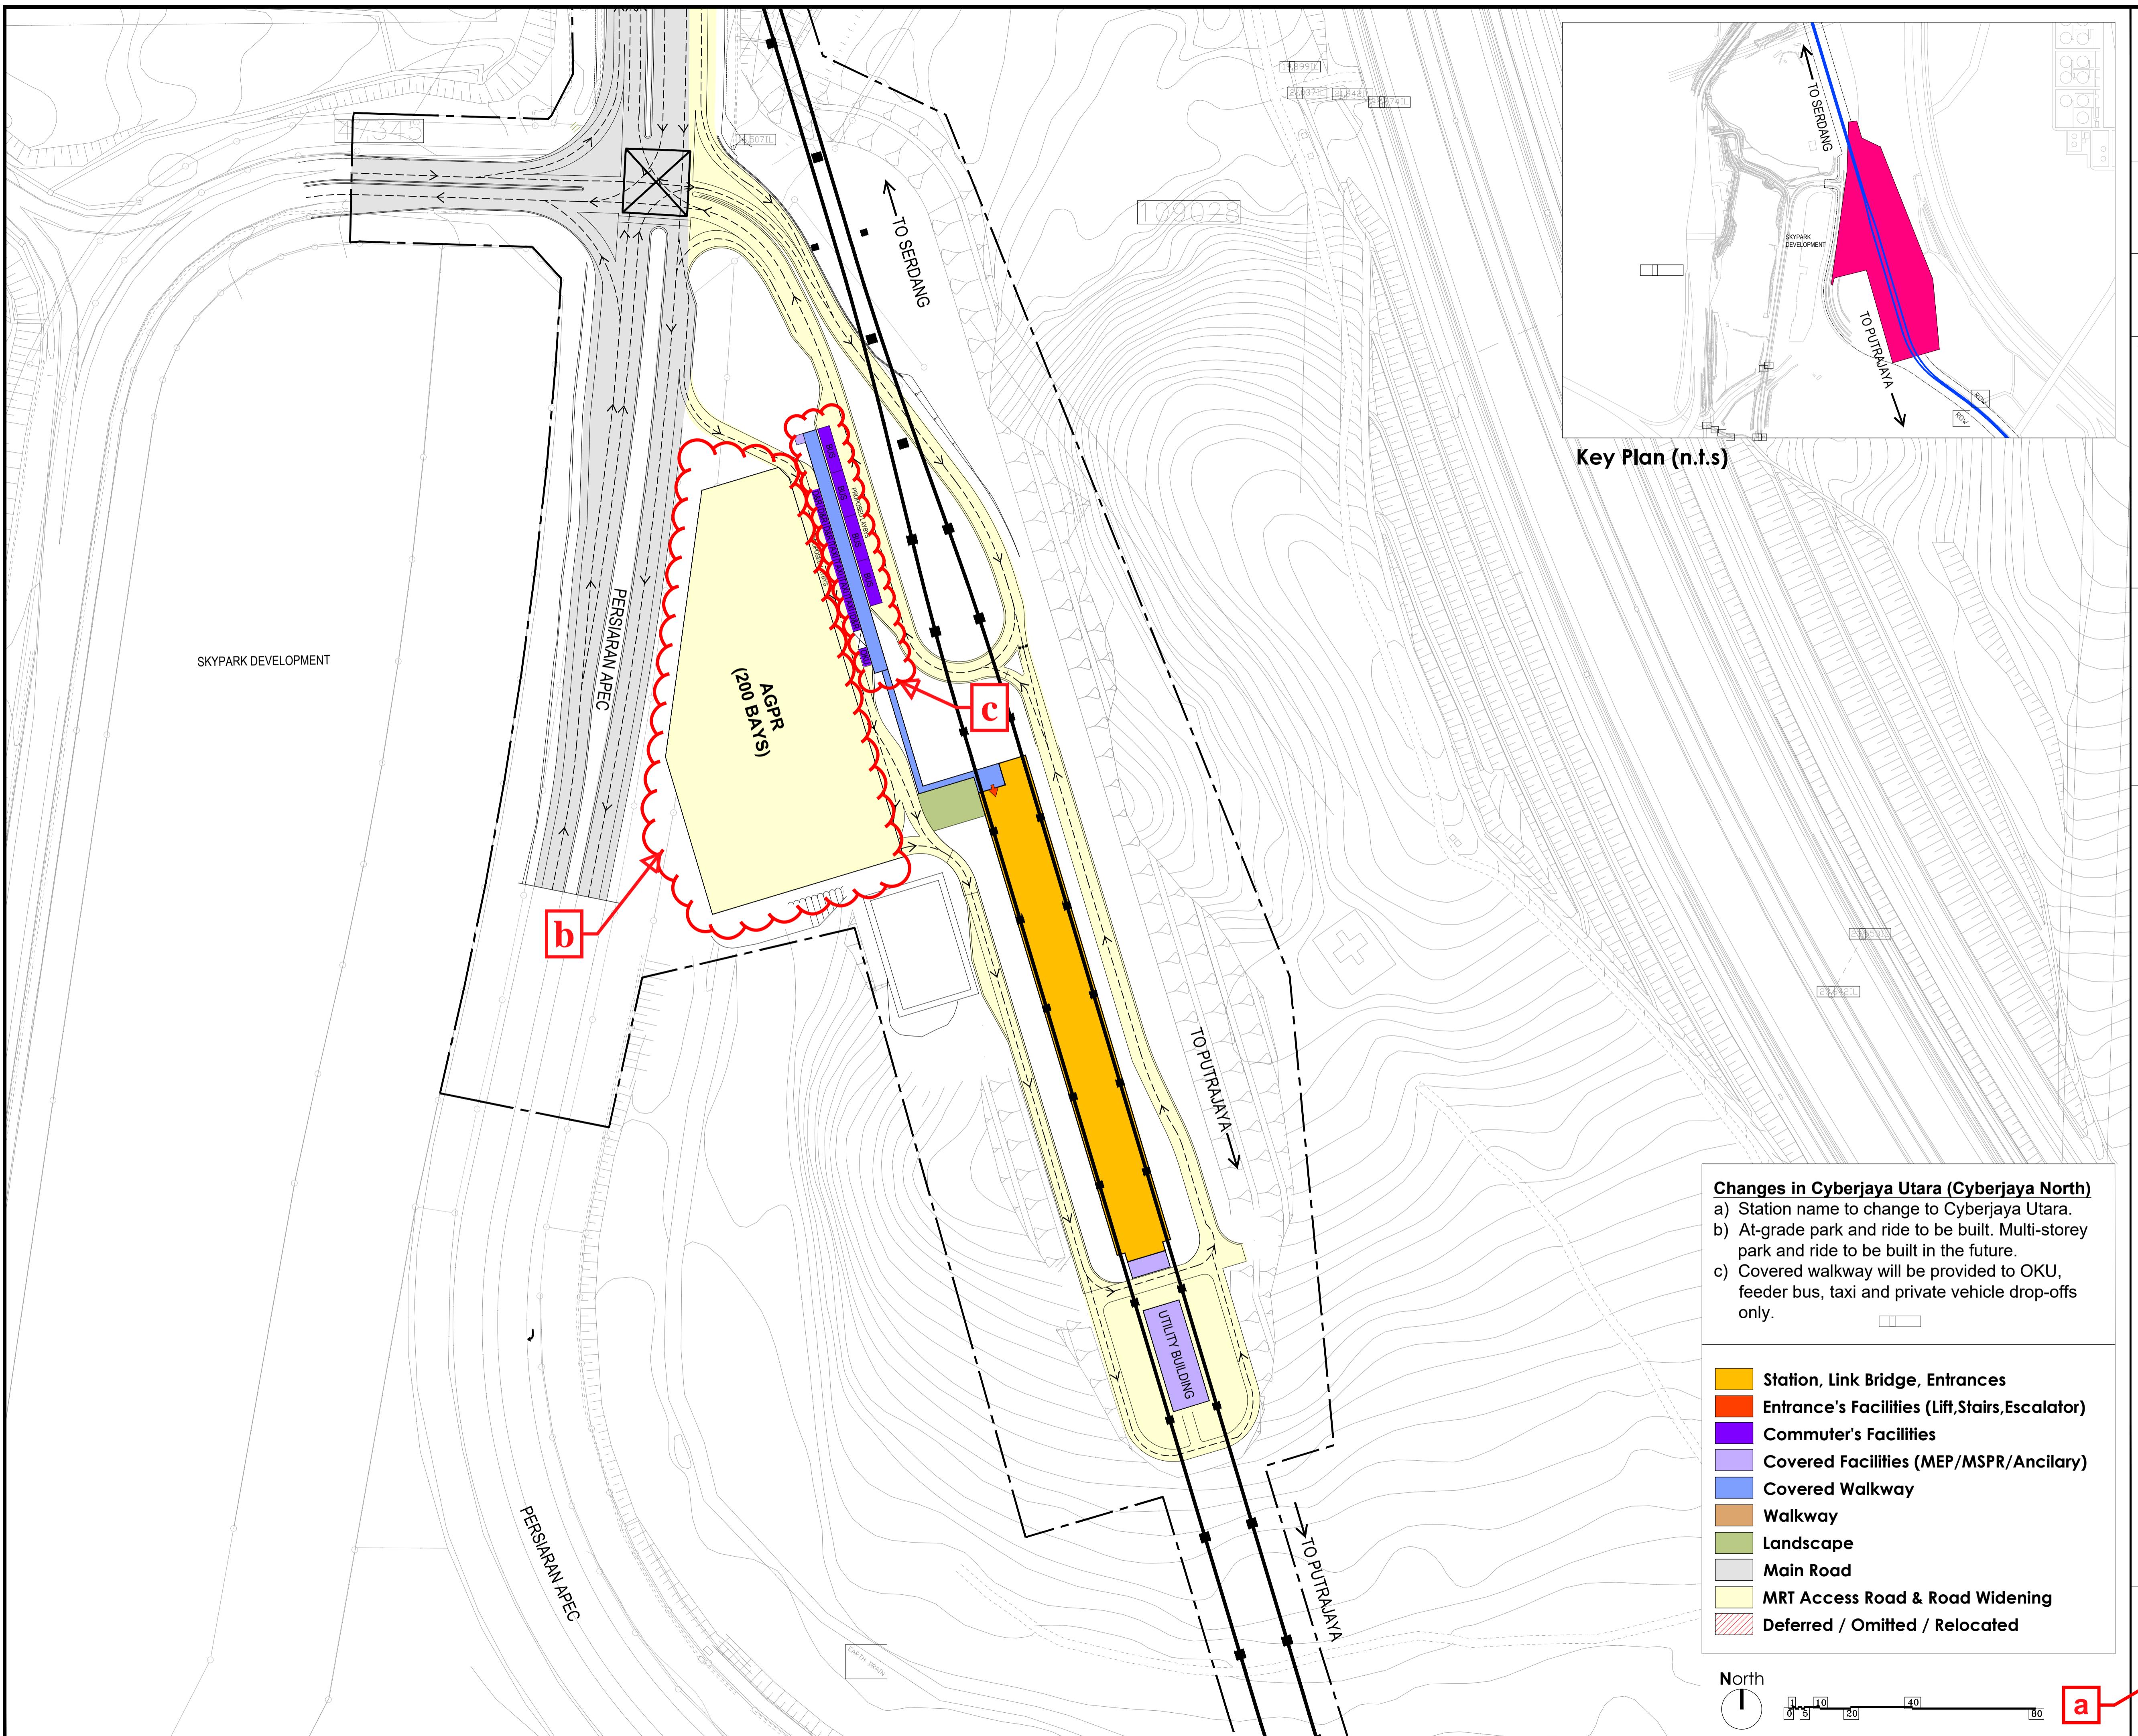

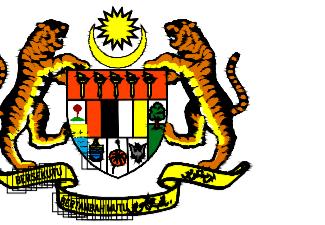

**KERAJAAN MALAYSIA**

PROJECT TITLE:  
PROJEK MASS RAPID TRANSIT LALUAN 2:  
PUTRAJAYA LINE  
(formerly known as PROJEK MRT LALUAN 2:  
SG BULOH - SERDANG - PUTRAJAYA (SSP))


PROJECT PACKAGE:  
SERDANG - PUTRAJAYA

SUPERVISING AGENCY :  
**AGENSI PENGANGKUTAN AWAM DARAT (APAD)**  
LAND PUBLIC TRANSPORT AGENCY (APAD)


**AGENSI PENGANGKUTAN AWAM DARAT (A.P.A.D.)**

ARAS G, M DAN 20, MENARA TUN ISMAIL MOHAMED ALI,  
NO. 25, JALAN RAJA LAUT, 50350 KUALA LUMPUR,  
MALAYSIA.  
TEL (ARAS G): 603-2603 6700 / TEL (ARAS 20): 603-2603 6600

PROJECT OWNER :  
**MRT CORP**  
Mass Rapid Transit Corporation Sdn Bhd  
(902884-V)  
5th FLOOR MENARA I&P 1,  
JALAN DUNGUN, DAMANSARA HEIGHTS,  
50490 KUALA LUMPUR.

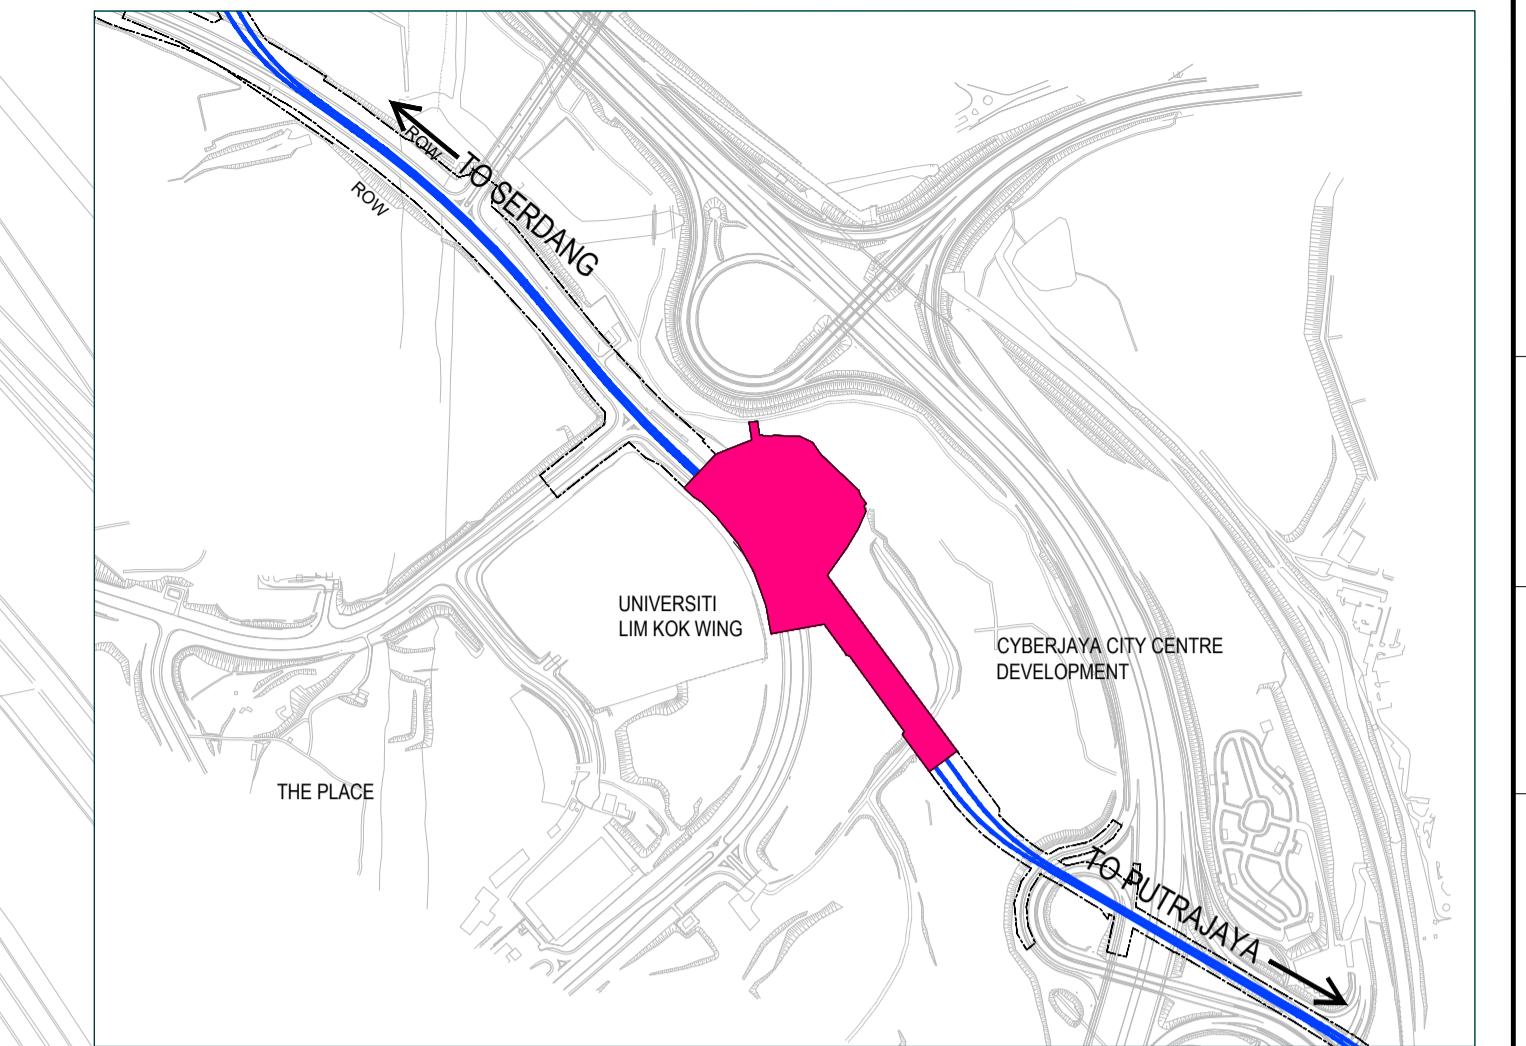

**Key Plan (n.t.s)**

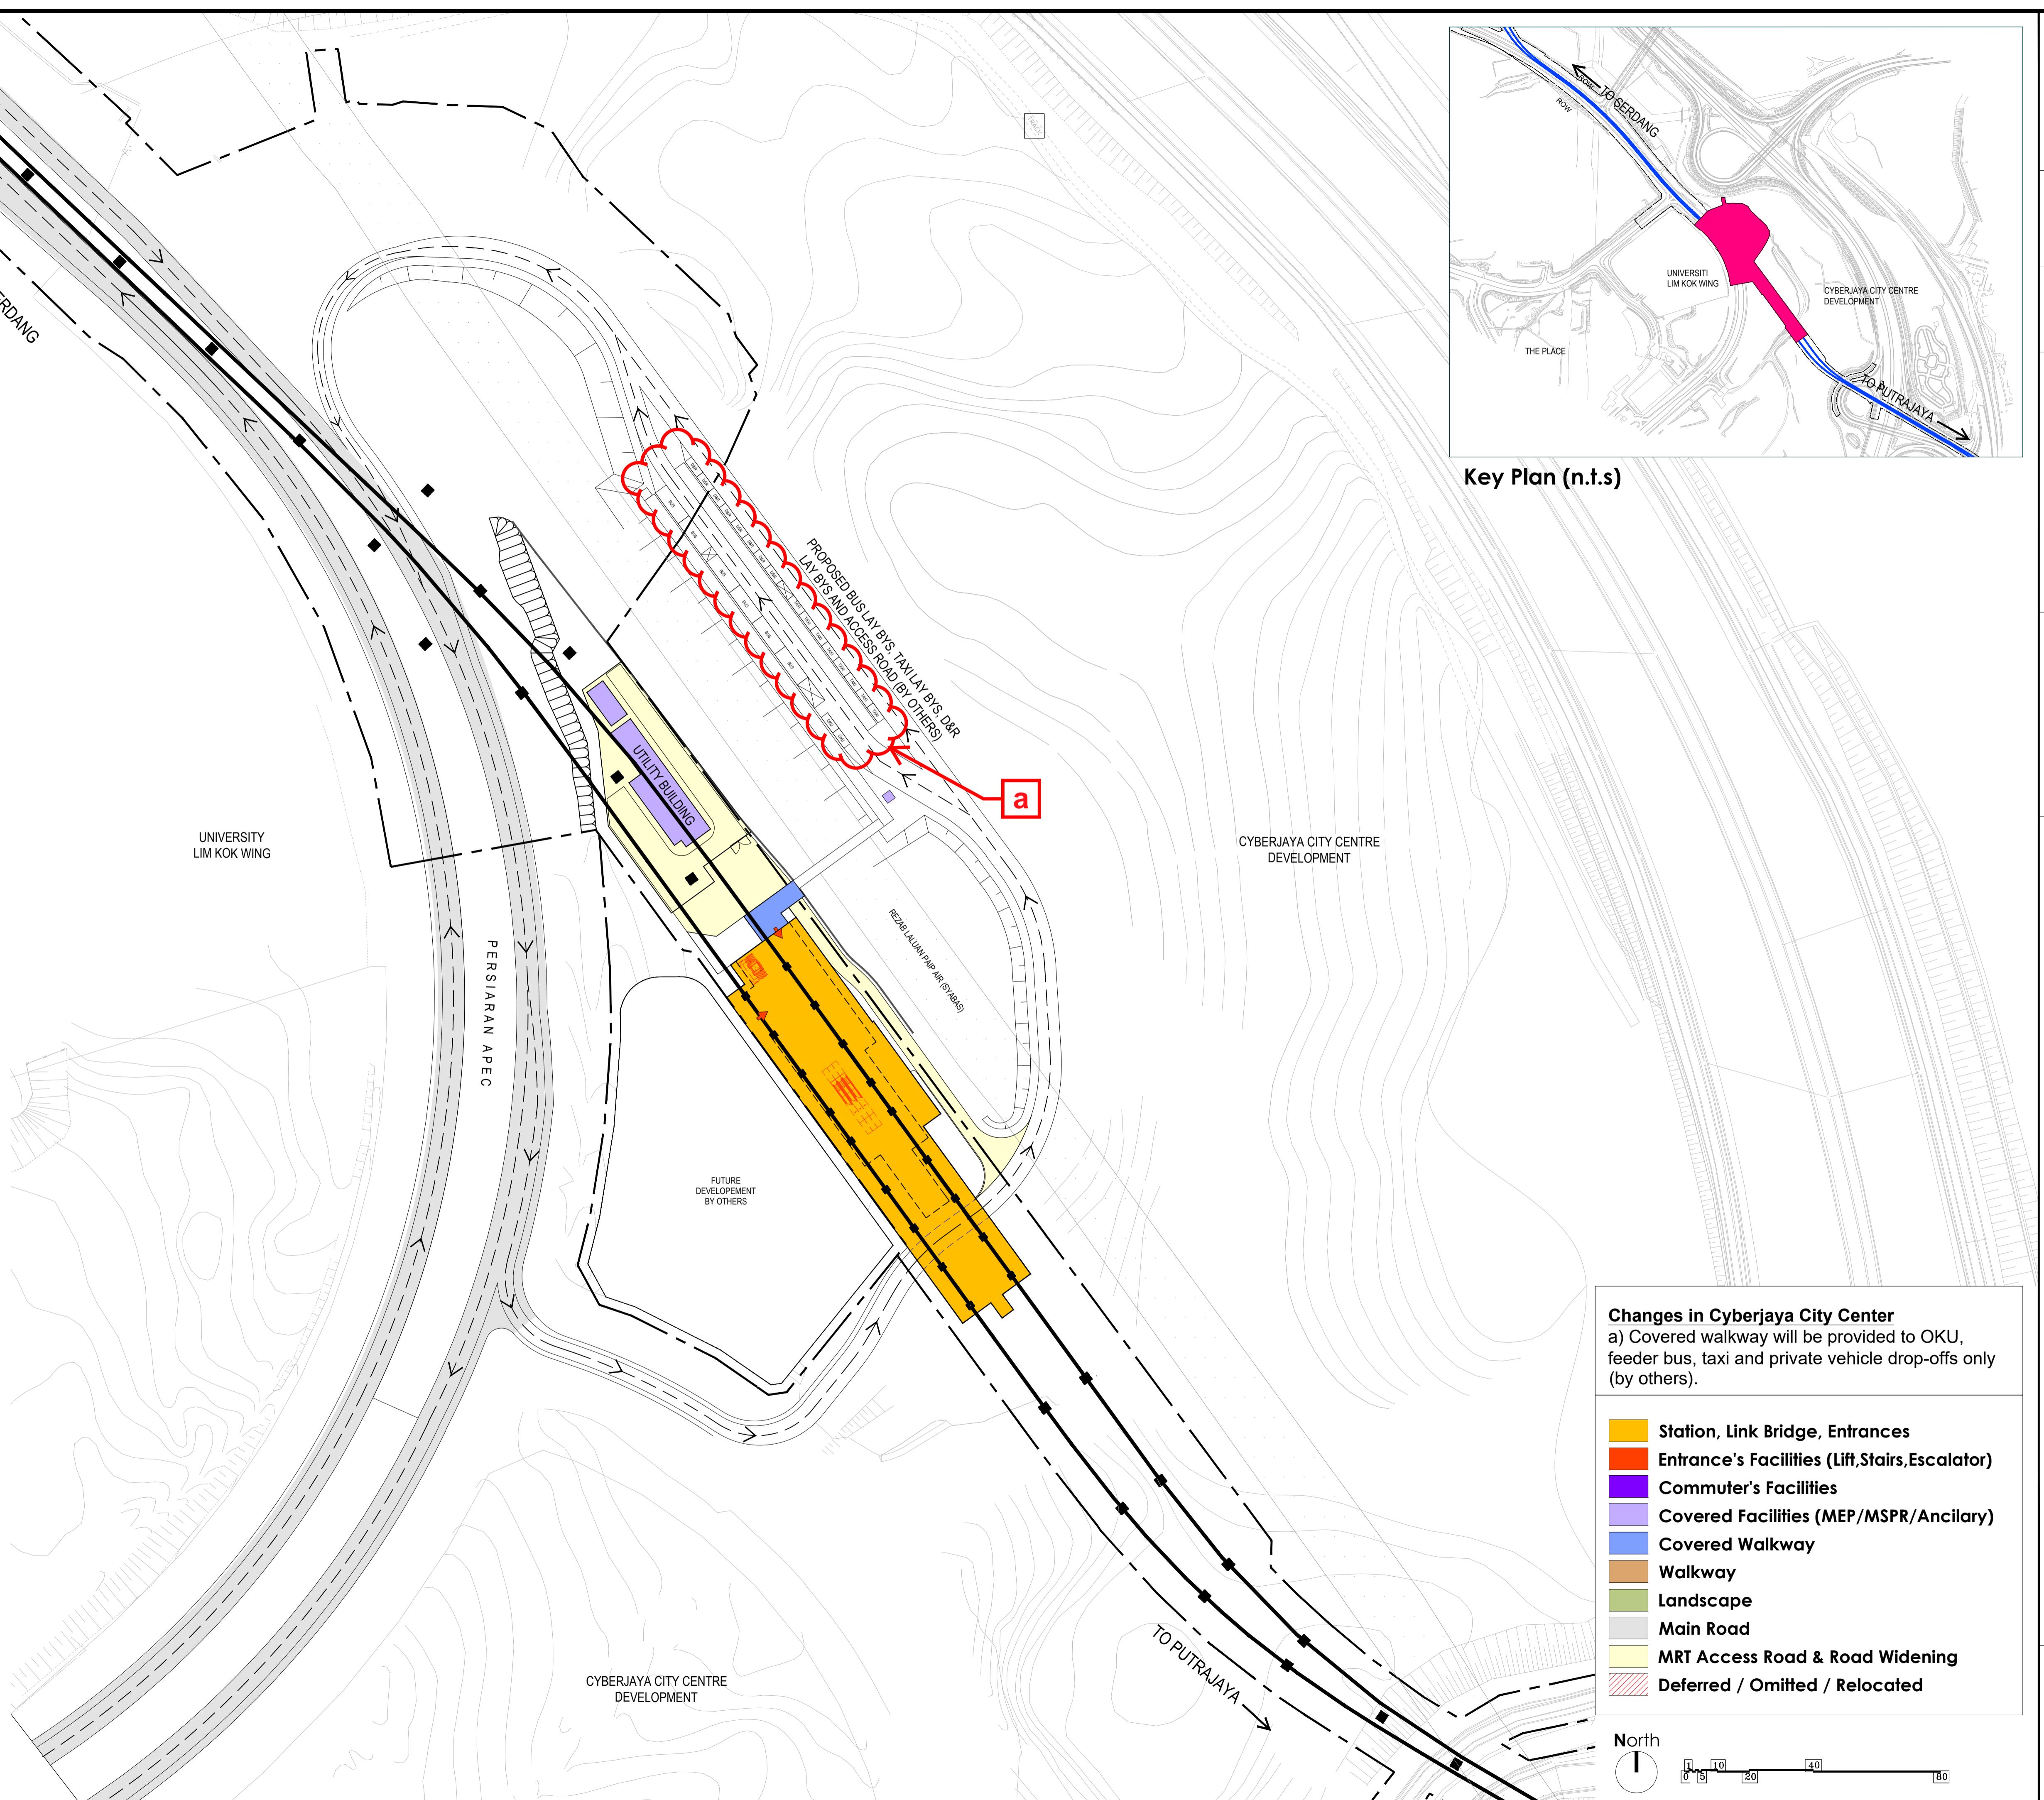

**Changes in Cyberjaya City Center**


a) Covered walkway will be provided to OKU, feeder bus, taxi and private vehicle drop-offs only (by others).

- Station, Link Bridge, Entrances
- Entrance's Facilities (Lift, Stairs, Escalator)
- Commuter's Facilities
- Covered Facilities (MEP/MSPR/Ancillary)
- Covered Walkway
- Walkway
- Landscape
- Main Road
- MRT Access Road & Road Widening
- Deferred / Omitted / Relocated

North

10 20 30 40 50 60

Drawing Title :  
S40  
CYBERJAYA CITY CENTRE

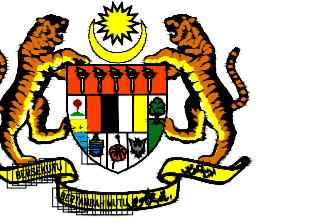

KERAJAAN MALAYSIA

PROJECT TITLE:  
PROJEK MASS RAPID TRANSIT LALUAN 2:  
PUTRAJAYA LINE  
(formerly known as PROJEK MRT LALUAN 2:  
SG BULOH - SERDANG - PUTRAJAYA (SSP))

PROJECT PACKAGE:


SERDANG - PUTRAJAYA

SUPERVISING AGENCY :  
  
AGENSI PENGANGKUTAN AWAM DARAT (APAD)  
LAND PUBLIC TRANSPORT AGENCY (APAD)

AGENSI PENGANGKUTAN AWAM DARAT  
(A.P.A.D.)

ARAS G, M DAN 20, MENARA TUN ISMAIL MOHAMED ALI,  
NO. 25, JALAN RAJA LAUT, 50350 KUALA LUMPUR,  
MALAYSIA.  
TEL (ARAS G): 603-2603 6700 / TEL (ARAS 20): 603-2603 6600

PROJECT OWNER :  
  
Mass Rapid Transit Corporation Sdn Bhd  
(902884-V)  
5th FLOOR MENARA I&P 1,  
JALAN DUNGUN, DAMANSARA HEIGHTS,  
50490 KUALA LUMPUR.

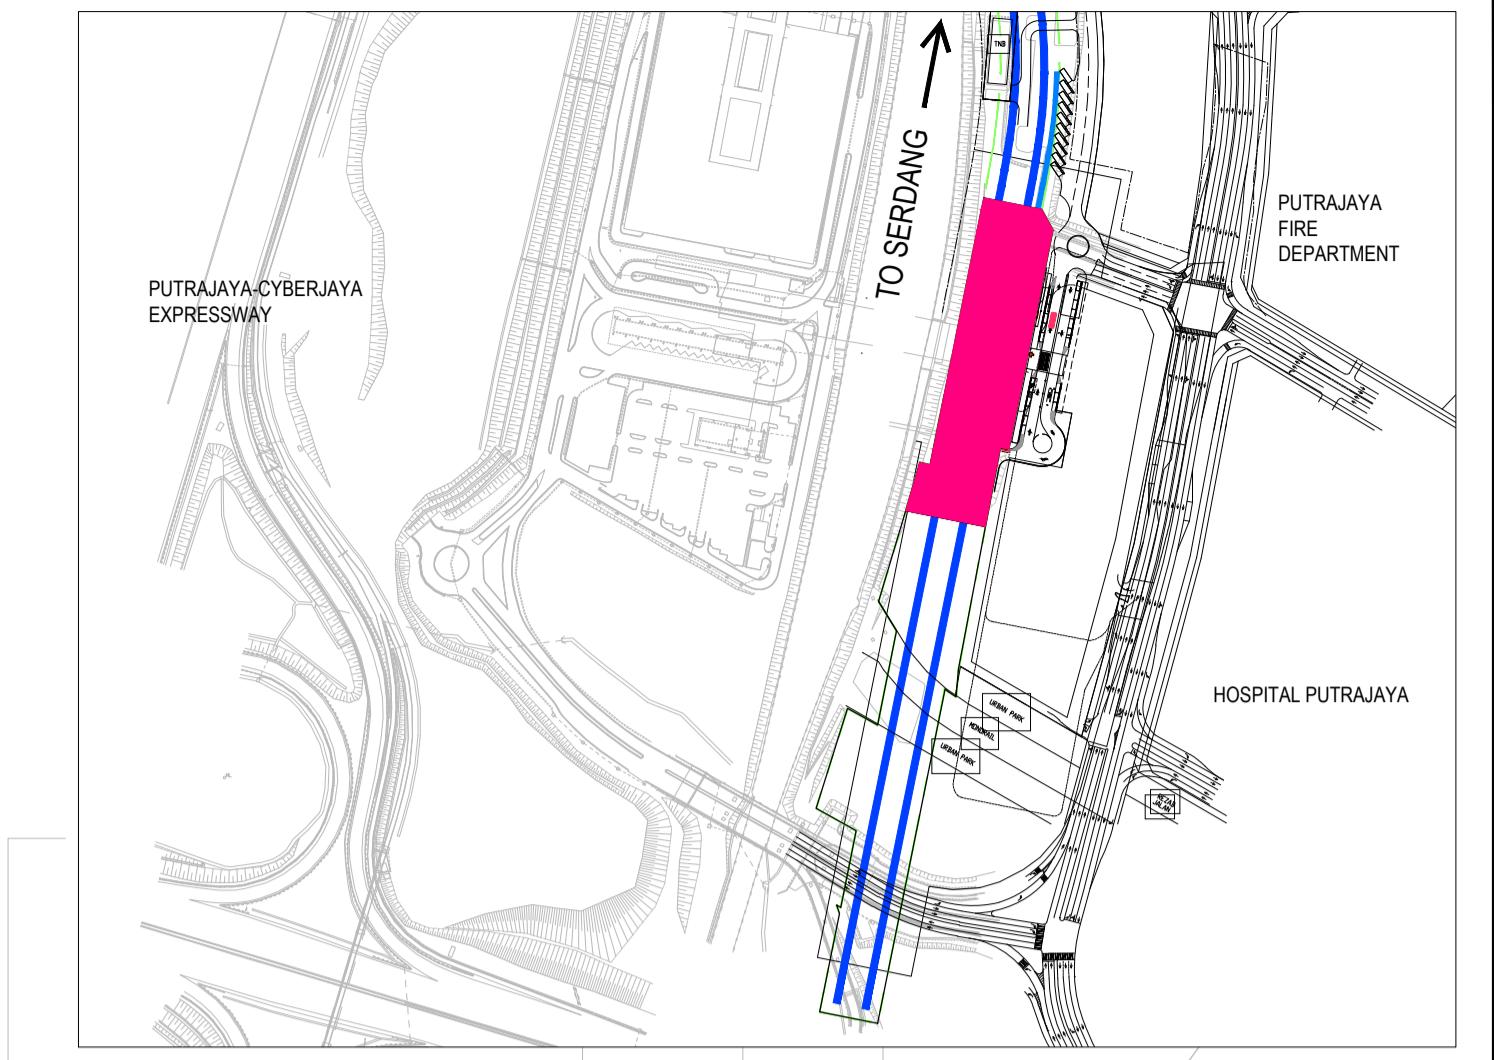

Key Plan (n.t.s)

